
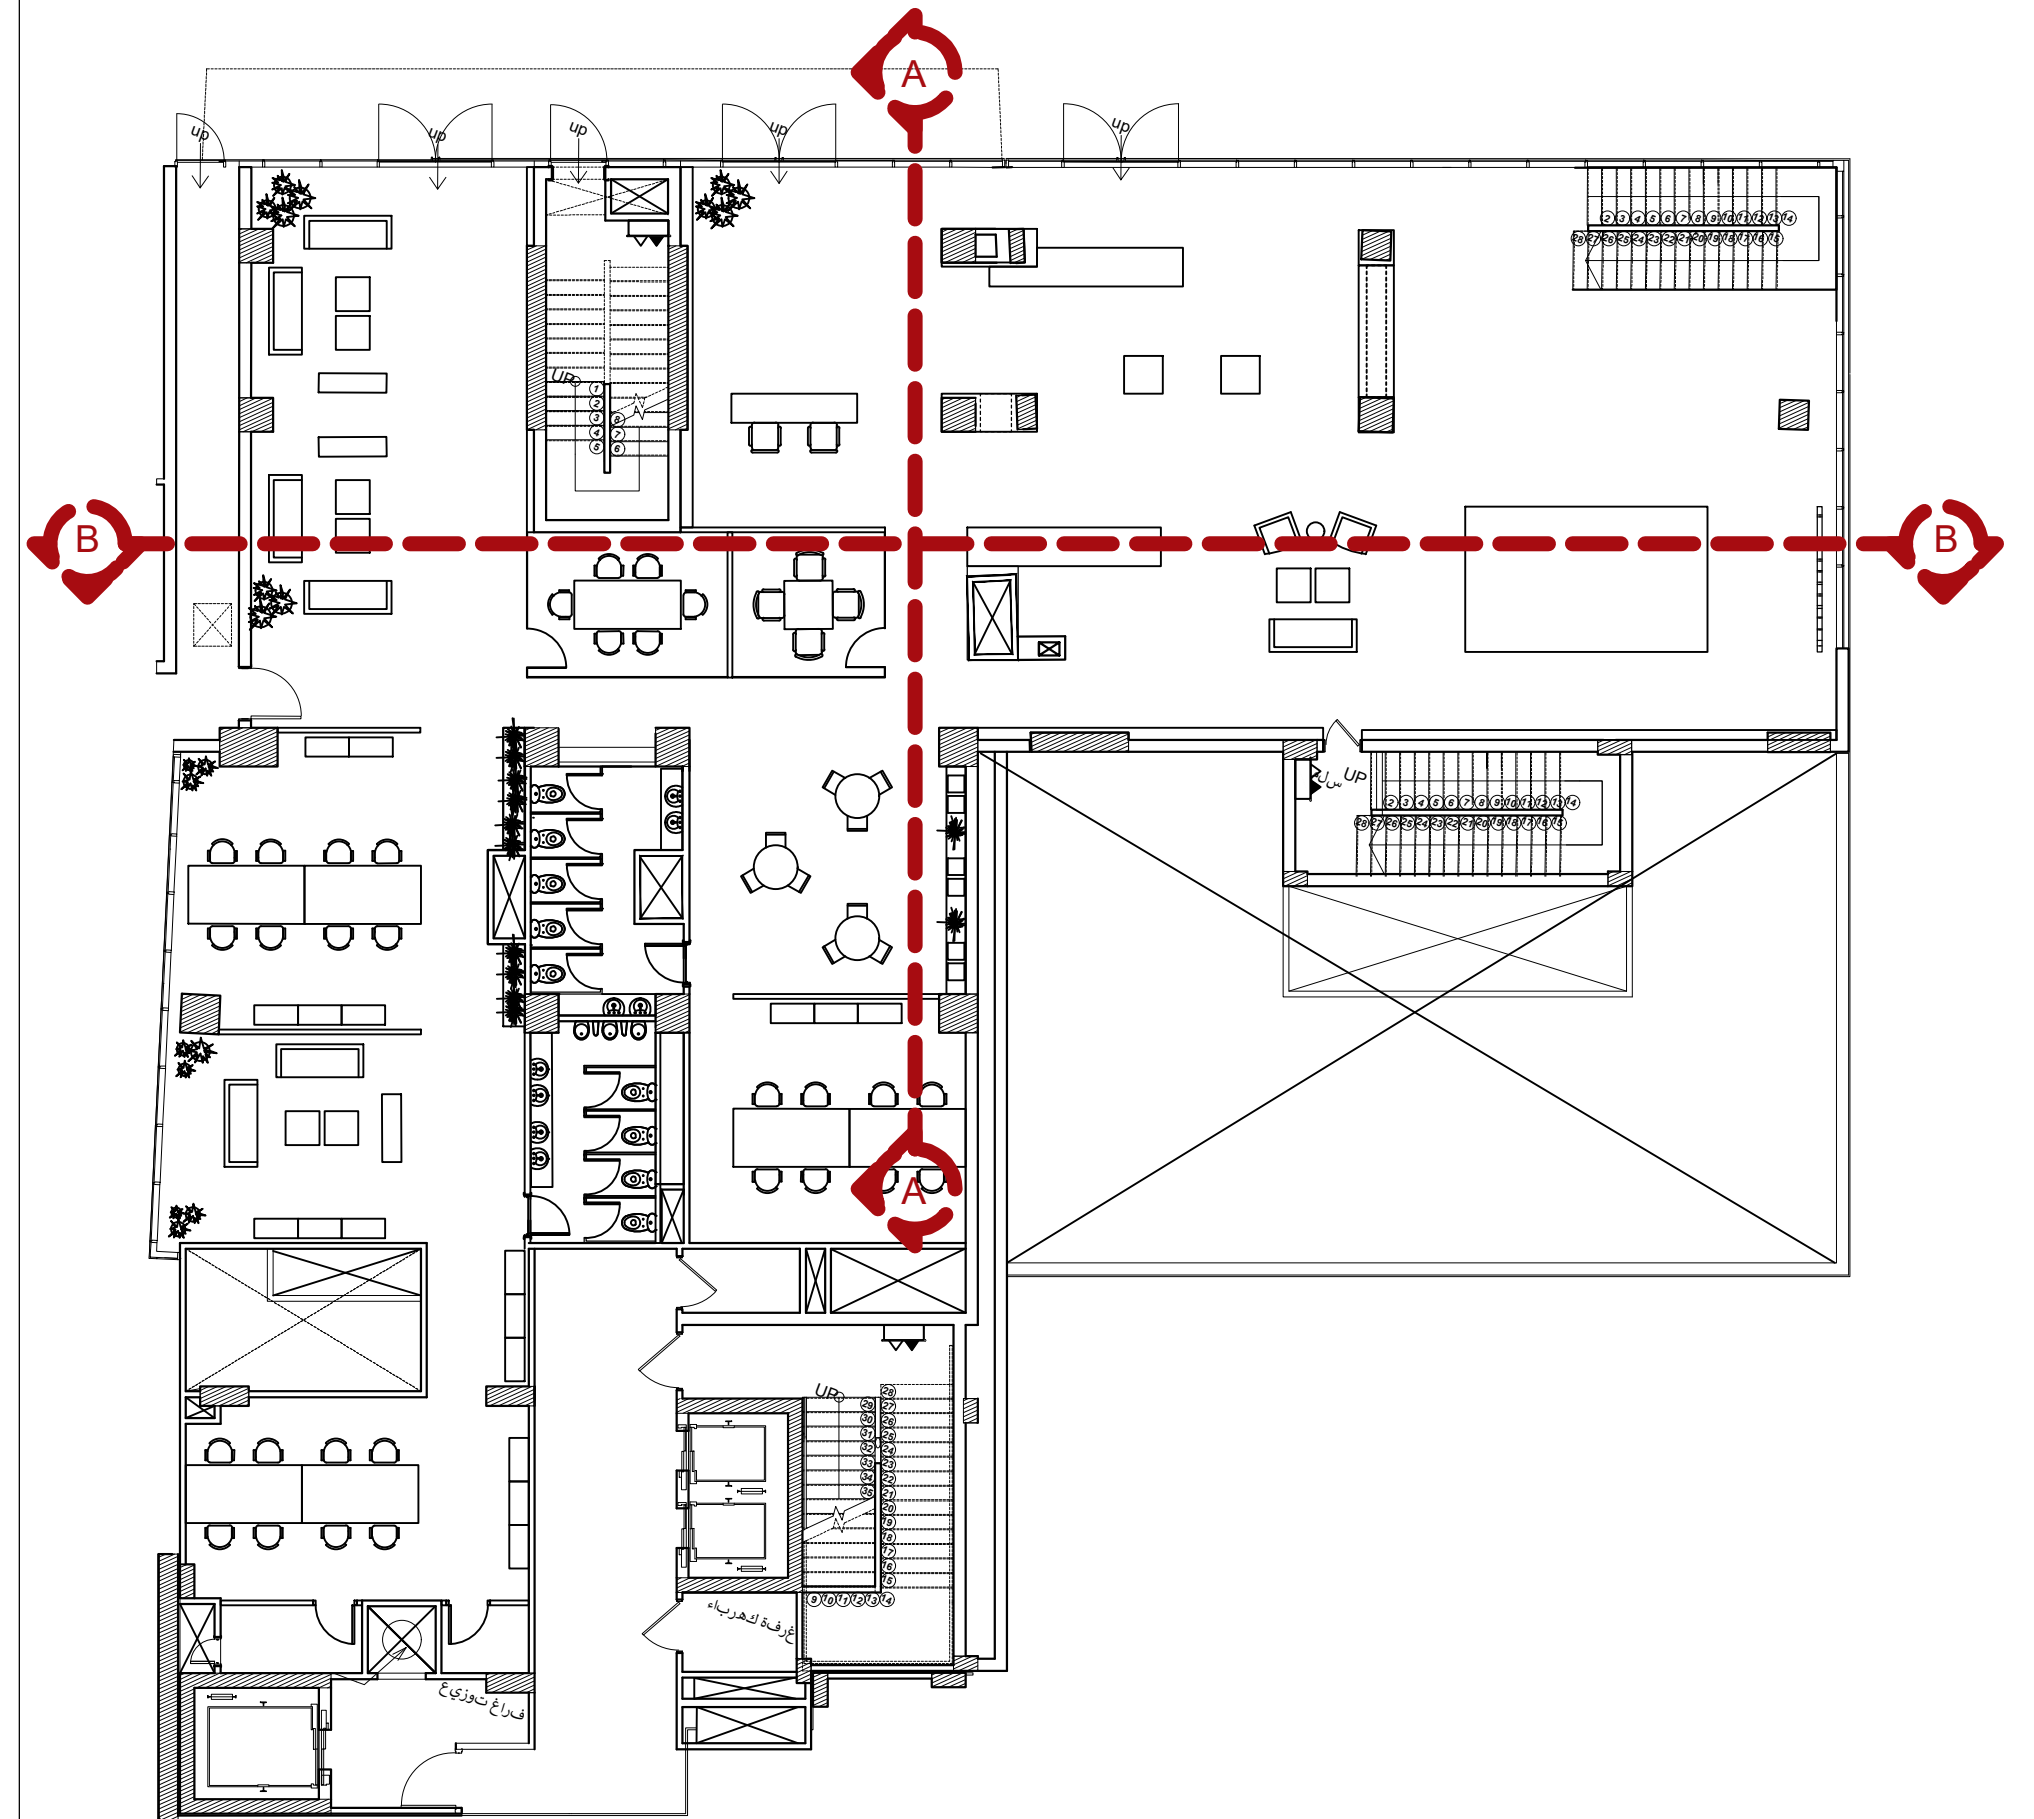


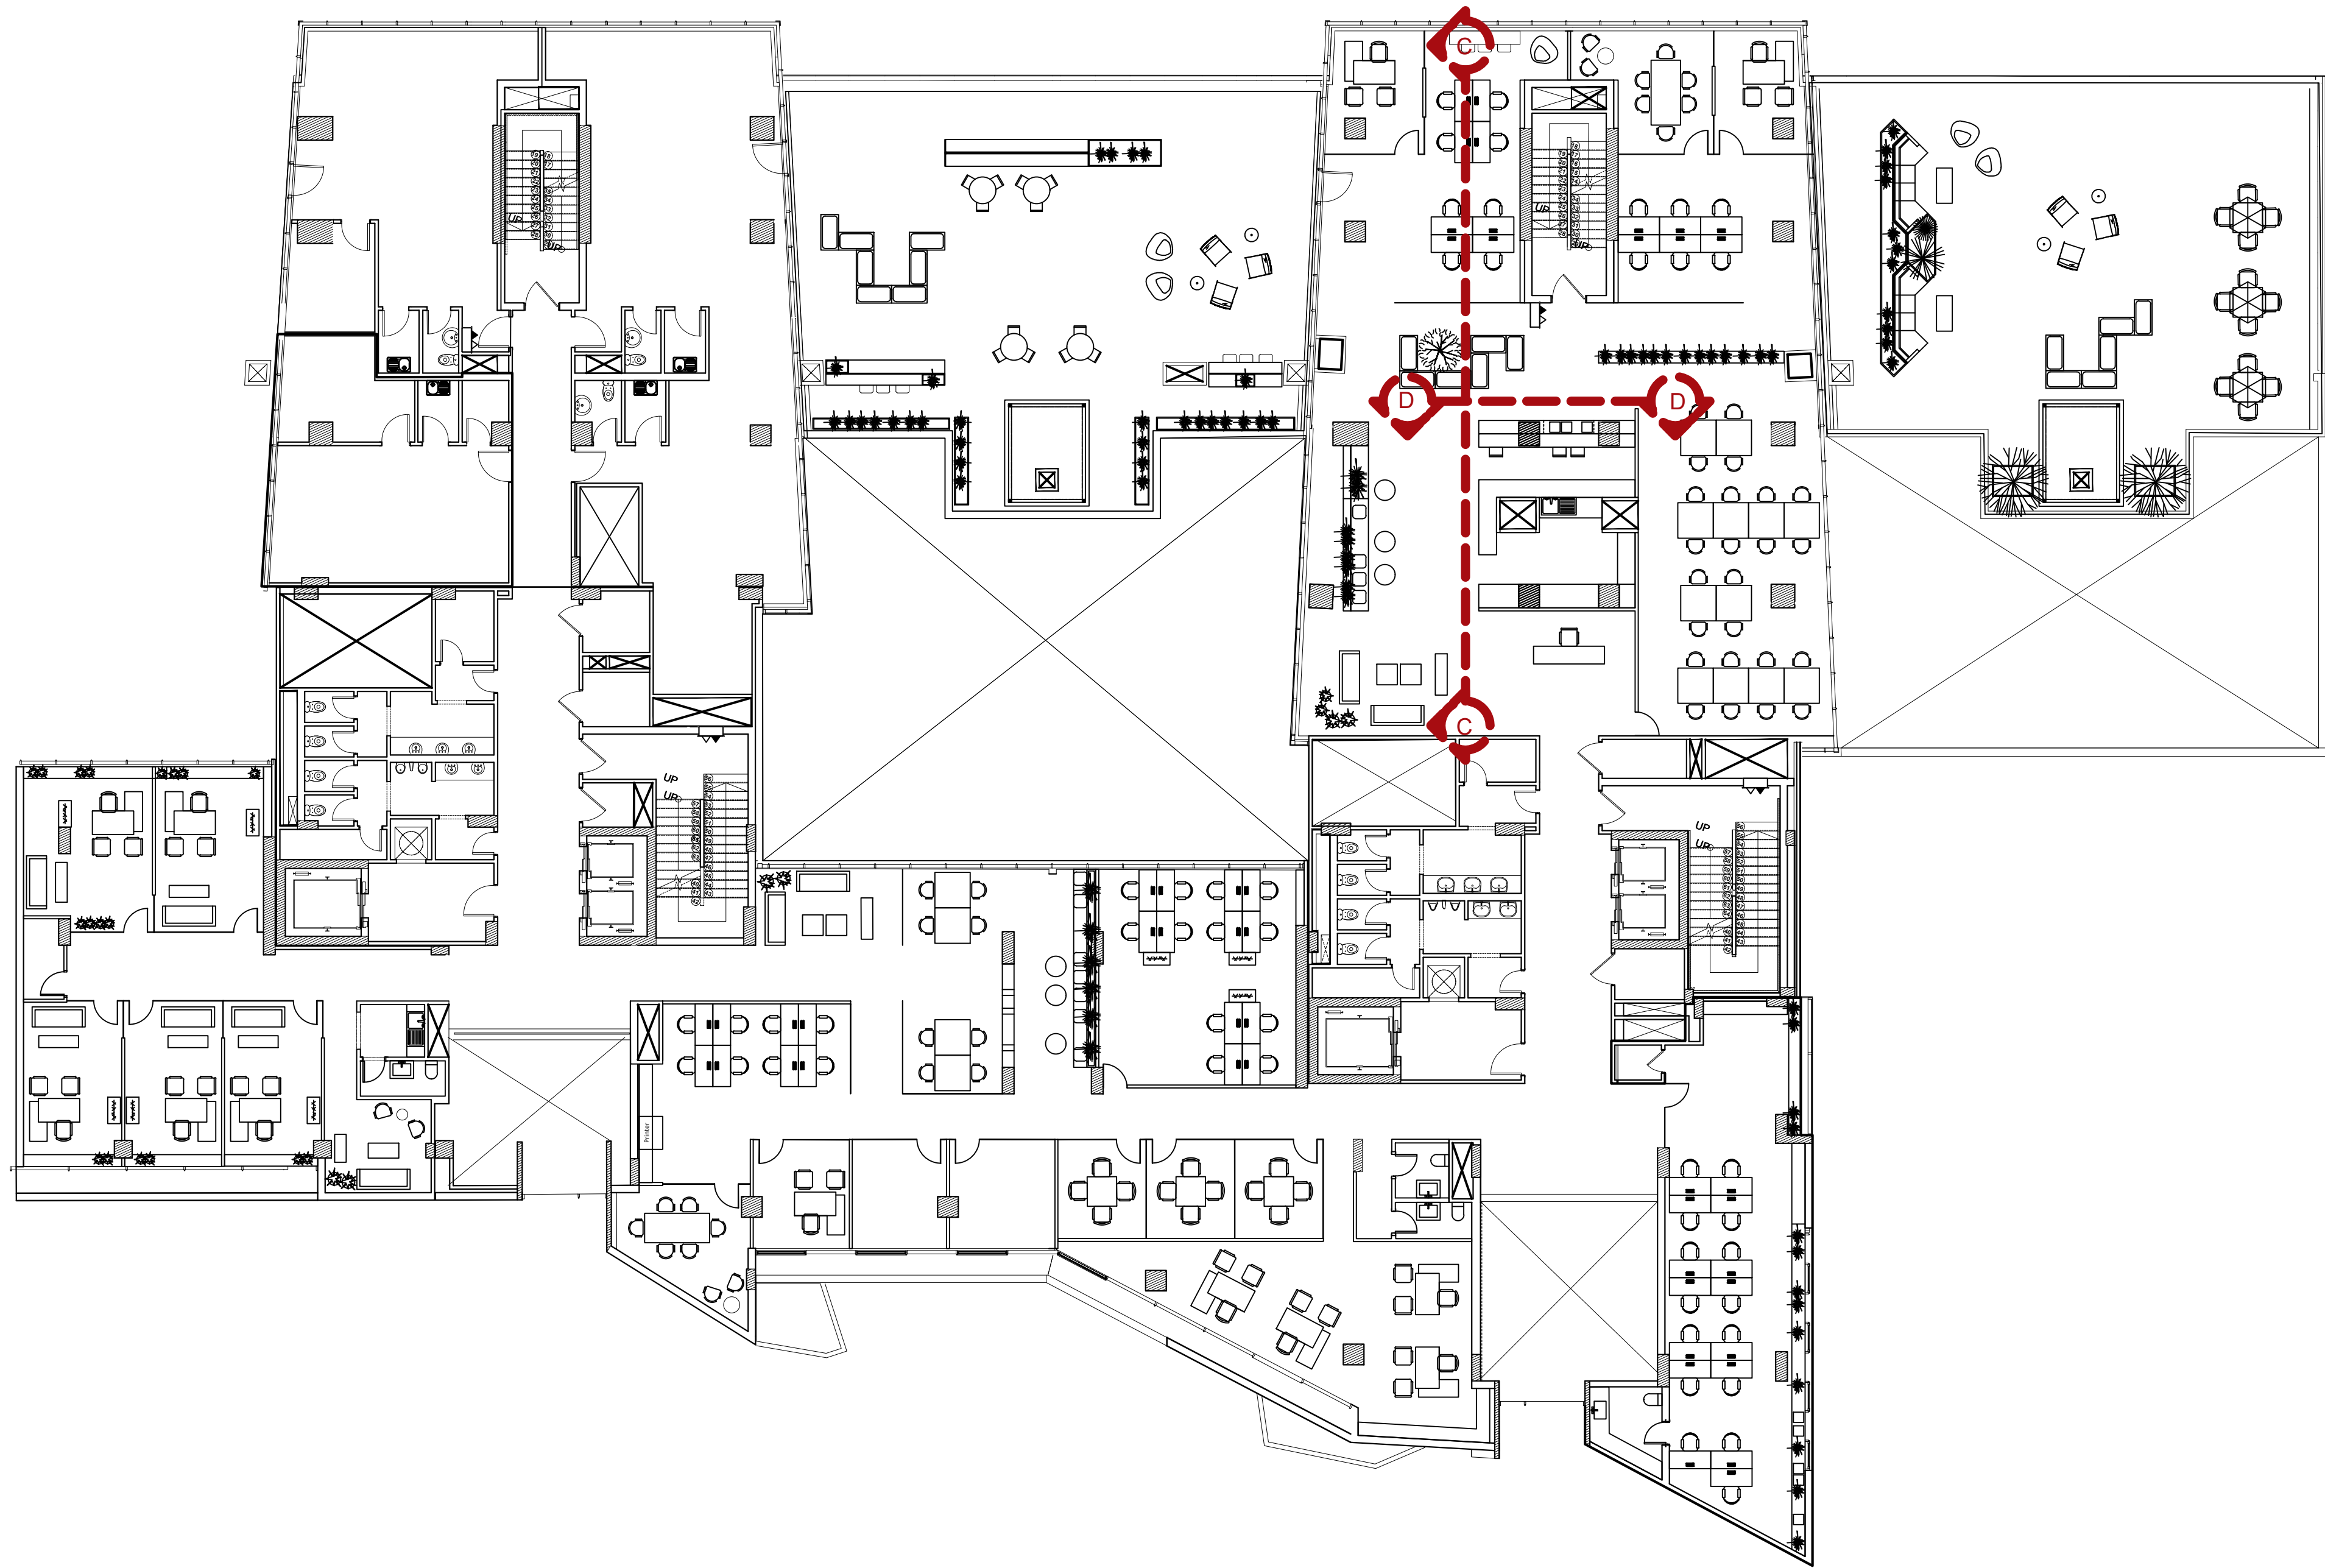


A
113.1

ELEVATION KEY PLANS

Project	Client	Design by
Etapa Square HQ & Sales Center		Fine Touch CONTRACTORS

©Copyright 2018, FINE TOUCH CONTRACTORS, 11 Off Omar Ibn ELKhatTab str.- Apart.603 - Ramu Buildings - Heliopolis 11341-Cairo - Egypt.

NOTES:			SHEET TITLE			
- THIS DRAWING IS COPY RIGHT PROTECTED AND CAN NOT BE REPRODUCED WITHOUT THE WRITTEN APPROVAL OF THE ARCHITECT. - ALL DIMENSIONS ARE IN CENTIMETERS UNLESS OTHERWISE MENTIONED. ALL DIMENSIONS MUST BE REVISED BY CONTRACTOR ON SITE.			ELEVATION KEY PLAN			
01	11-08-2023	FOR REVIEW	A-113.1			
Rev.	DATE	DESCRIPTION				
Concept Design Submission						
CAD DWG File	113.Etappo-A-Elevations		Date	12 . 08 . 2023	Rev.	01
Drawn by	SB		Scale	1/50		
Checked by						
Sheet No.						

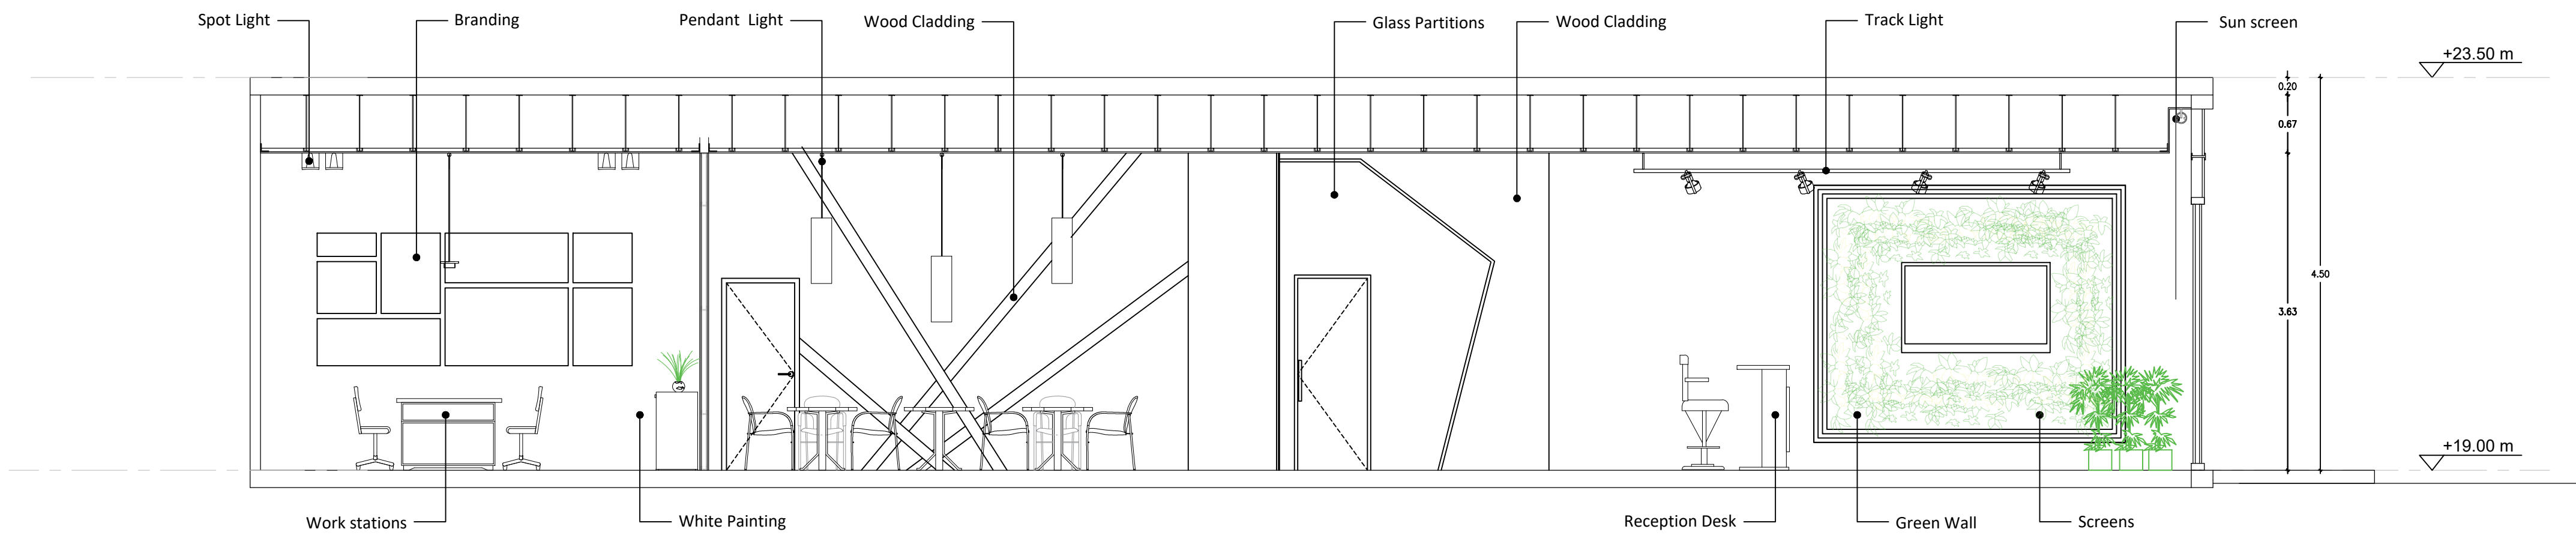

A
113.2


Elevation A-A



A
113.2

Elevation A-A

Project	Client	Design by	NOTES:			SHEET TITLE			
Etapa Square HQ & Sales Center		Fine Touch CONTRACTORS	- THIS DRAWING IS COPY RIGHT PROTECTED AND CAN NOT BE REPRODUCED WITHOUT THE WRITTEN APPROVAL OF THE ARCHITECT.			ELEVATION A-A			
			- ALL DIMENSIONS ARE IN CENTIMETERS UNLESS OTHERWISE MENTIONED. ALL DIMENSIONS MUST BE REVISED BY CONTRACTOR ON SITE.						
			01	11-08-2023	FOR REVIEW				
			Rev.	DATE	DESCRIPTION				
			Concept Design Submission			A-113.2			
			CAD DWG File	113.Etapa-A-Elevations		Date	12 .08 . 2023	Rev.	01
			Drawn by	SB					
			Checked by						
			Sheet No.			Scale 1/50			

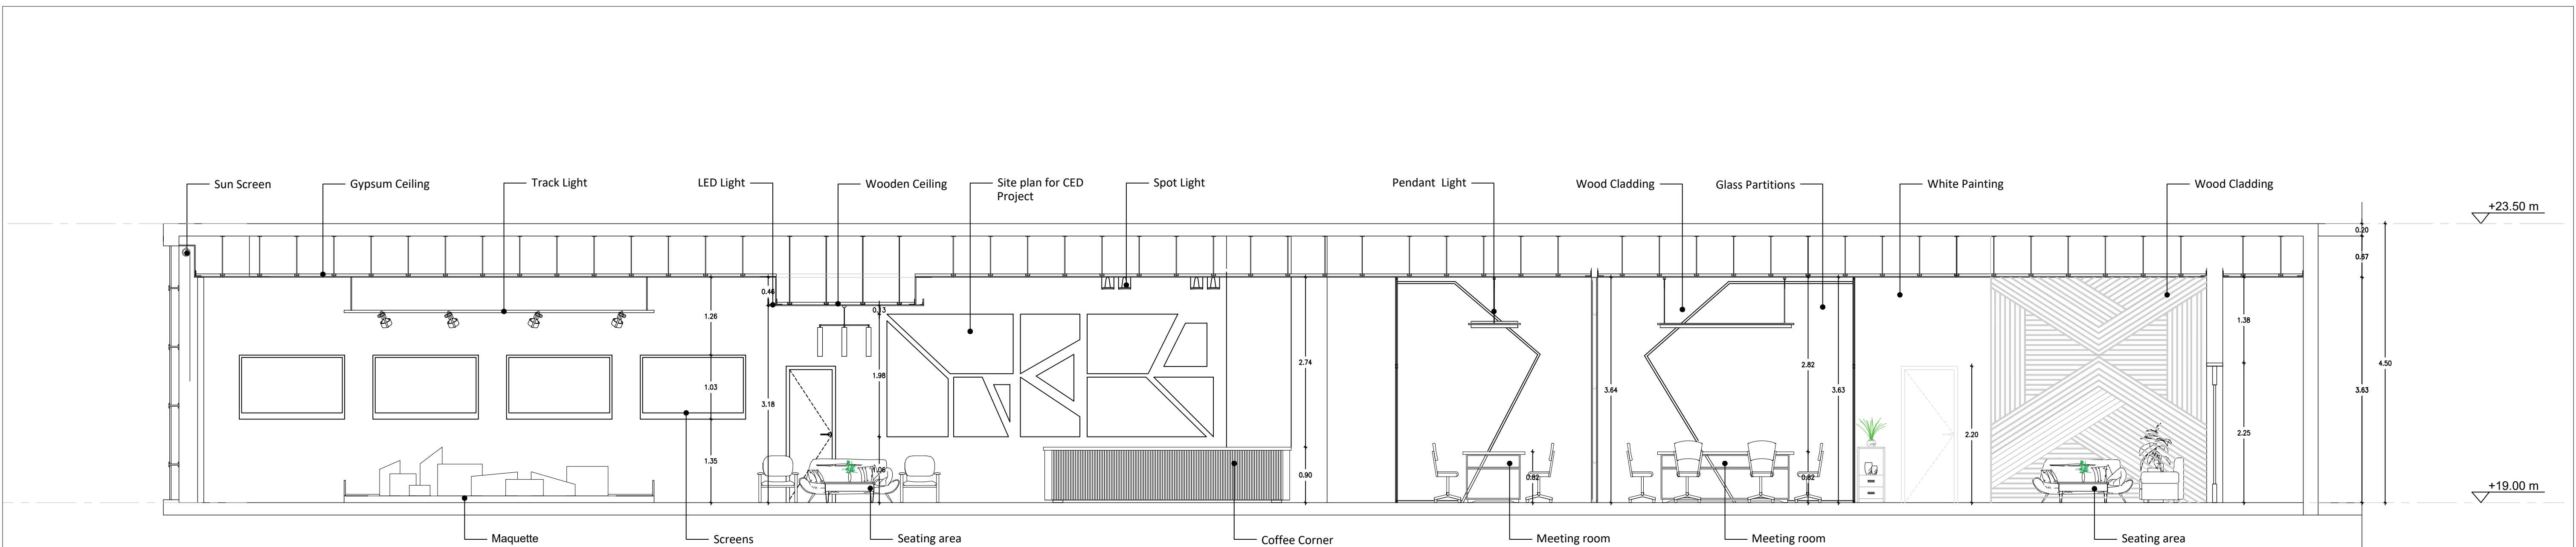

A
113.3


Elevation B-B



A
113.3

Elevation B-B

Project	Client	Design by	NOTES:	SHEET TITLE			
Etapa Square HQ & Sales Center		Fine Touch CONTRACTORS	- THIS DRAWING IS COPY RIGHT PROTECTED AND CAN NOT BE REPRODUCED WITHOUT THE WRITTEN APPROVAL OF THE ARCHITECT. - ALL DIMENSIONS ARE IN CENTIMETERS UNLESS OTHERWISE MENTIONED. ALL DIMENSIONS MUST BE REVISED BY CONTRACTOR ON SITE.	ELEVATION B-B			
				A-113.2			
				Concept Design Submission			
				CAD DWG File 113.Etapa-A-Elevations			
				Date 12 . 08 . 2023 Rev. 01			
				Scale 1/50			
				Drawn by SB			
				Checked by			
				Sheet No.			

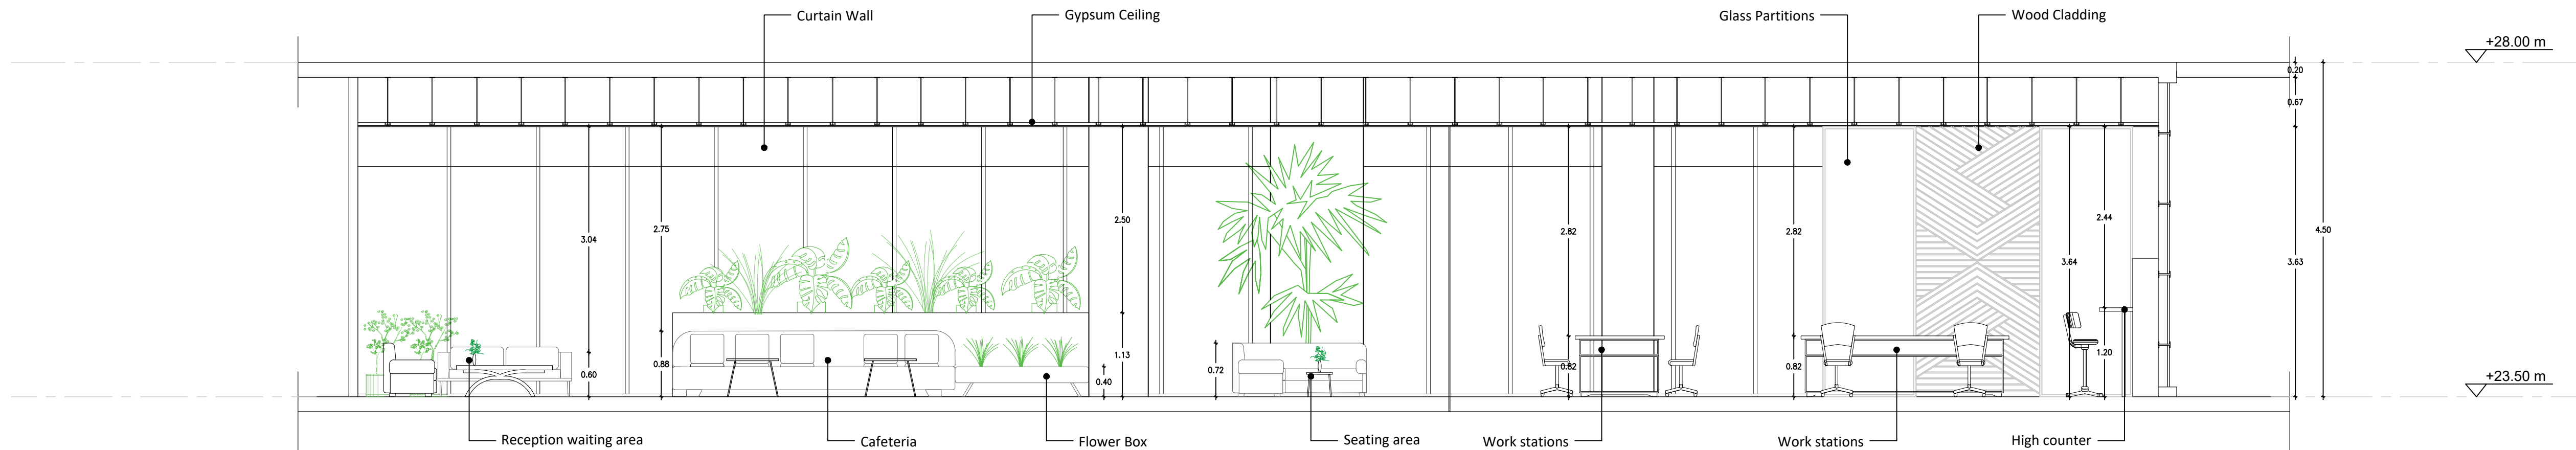


A
113.4



A
113.4

Elevation C-C

Project	Client	Design by	NOTES:										SHEET TITLE				
Etapa Square HQ & Sales Center		Fine Touch CONTRACTORS	- THIS DRAWING IS COPY RIGHT PROTECTED AND CAN NOT BE REPRODUCED WITHOUT THE WRITTEN APPROVAL OF THE ARCHITECT. - ALL DIMENSIONS ARE IN CENTIMETERS UNLESS OTHERWISE MENTIONED. ALL DIMENSIONS MUST BE REVISED BY CONTRACTOR ON SITE.										ELEVATION C-C				
			01	11-08-2023	FOR REVIEW												
			Rev.	DATE	DESCRIPTION												
			Concept Design Submission										A-113.4				
			CAD DWG File		113.Etapa-A-Elevations								Date	12 . 08 . 2023		Rev.	01
			Drawn by		SB												
Checked by										Scale 1/50							
Sheet No.																	

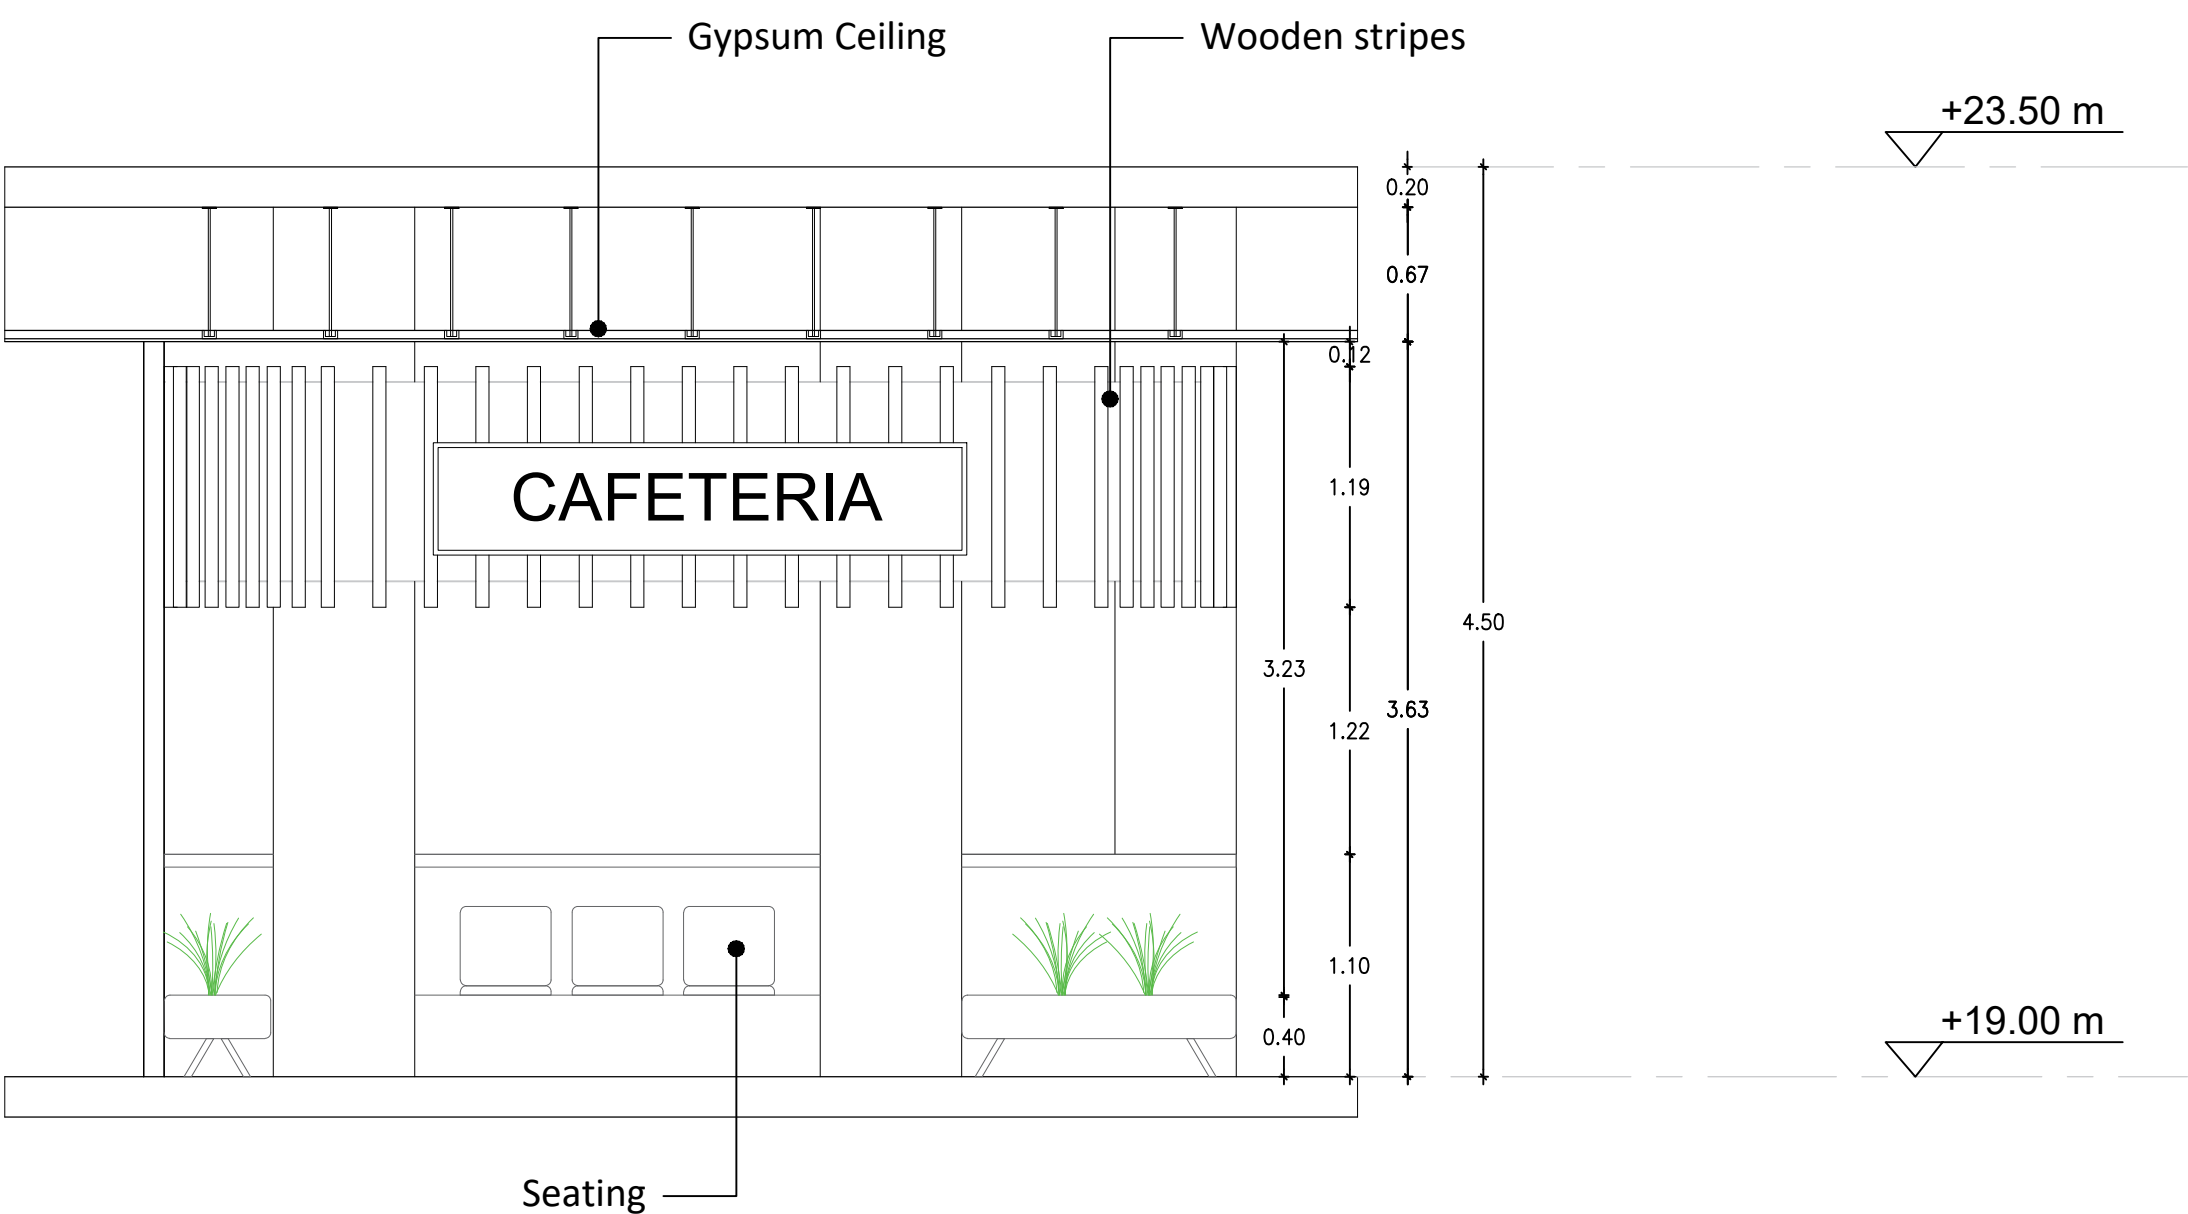

A

113.5

Elevation D-D



A

113.5

Elevation D-D

Project	Client	Design by	NOTES:										SHEET TITLE								
Etapu Square HQ & Sales Center		Fine Touch CONTRACTORS	- THIS DRAWING IS COPY RIGHT PROTECTED AND CAN NOT BE REPRODUCED WITHOUT THE WRITTEN APPROVAL OF THE ARCHITECT.										ELEVATION D-D								
			- ALL DIMENSIONS ARE IN CENTIMETERS UNLESS OTHERWISE MENTIONED, ALL DIMENSIONS MUST BE REVISED BY CONTRACTOR ON SITE.																		
			01	11-08-2023	FOR REVIEW																
			Rev.	DATE	DESCRIPTION																
			Concept Design Submission												A-113.5						
			CAD DWG File:	113.Etapu-A-Elevations													Date	12 . 08 . 2023		Rev.	01
			Drawn by	SB																	
			Checked by																		
Sheet No.														Scale 1/50							