



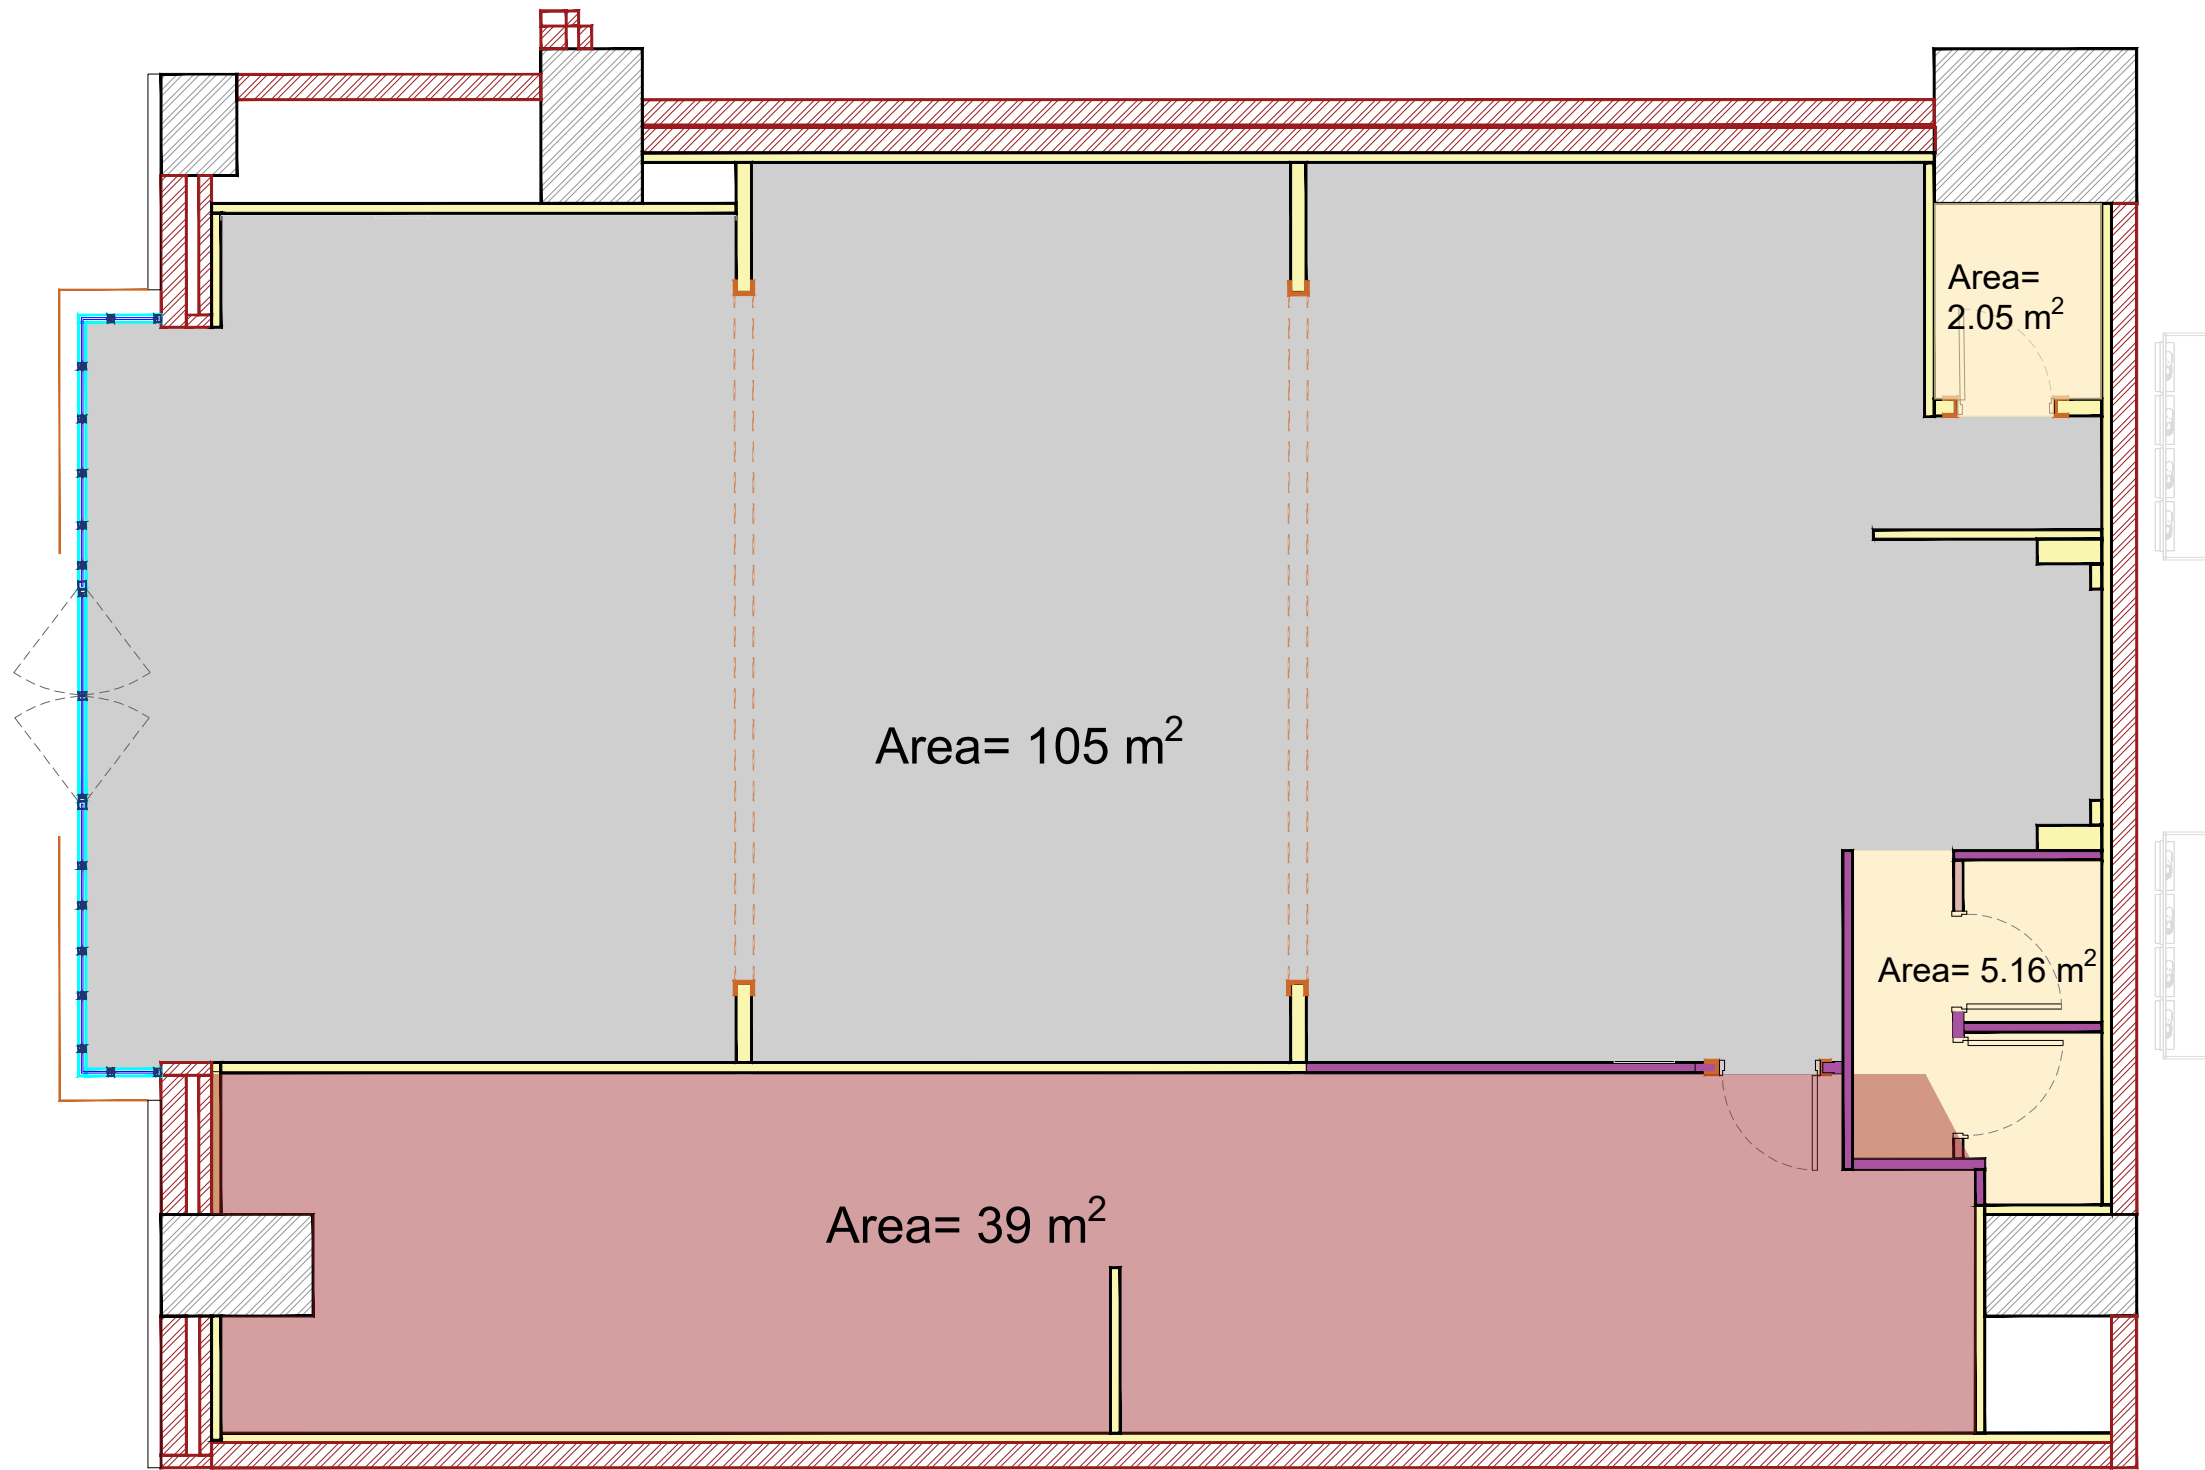

A
102


Zoning plan

Project	Client	General Contractor	Interior Design	Mall											NOTES:											
GURU Open Air mall															- THIS DRAWING IS COPY RIGHT PROTECTED AND CAN NOT BE REPRODUCED WITHOUT THE WRITTEN APPROVAL OF THE ARCHITECT. - ALL DIMENSIONS ARE IN CENTIMETERS UNLESS OTHERWISE MENTIONED. ALL DIMENSIONS MUST BE REVISED BY CONTRACTOR ON SITE.	SHEET-TITLE										
															02	03-12-2025	FOR REVIEW									
															01	03-12-2025	FOR REVIEW									
															00	26-11-2025	FOR REVIEW									
															Rev.	DATE	DESCRIPTION									
															Architecture Design Package						A-102					
															CAD DWG File: 102.GURU-Open Air mall Zoning plan											
										Drawn by: SB						Date	03.12.2025			Rev.	02					
										Checked by: OA																
										Sheet No.						Scale 1/100										

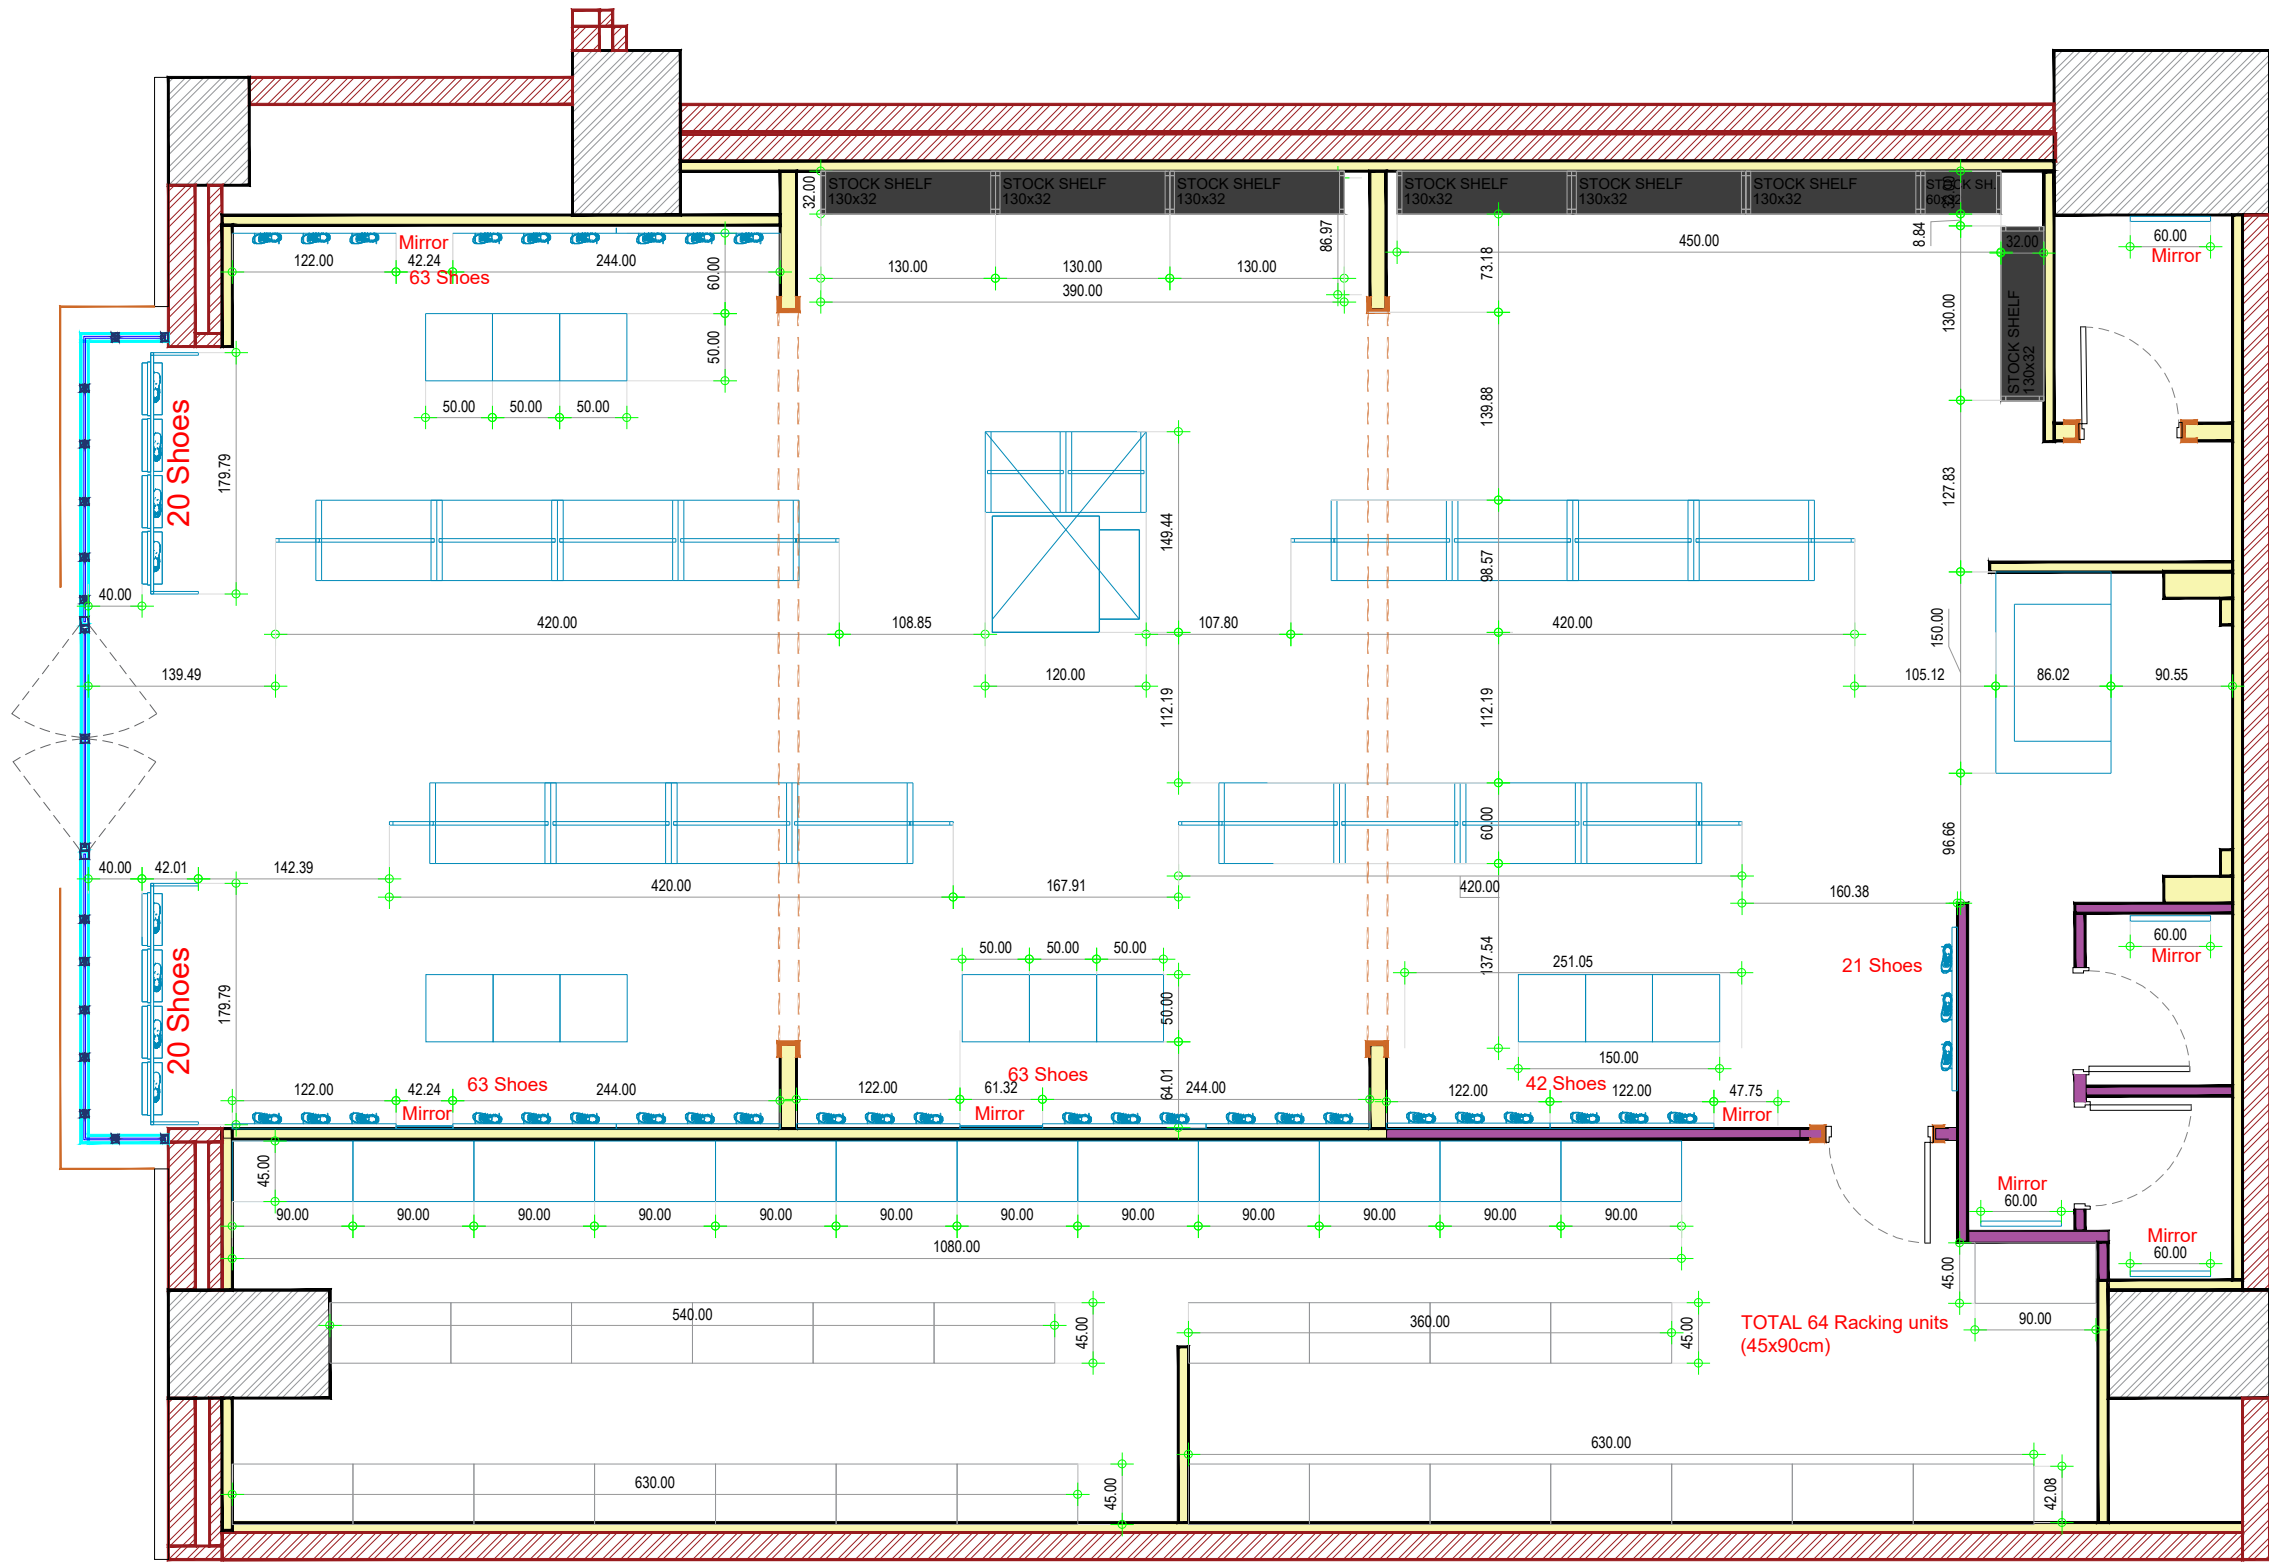

A
105
Fixture Layout


Project	Client	General Contractor	Interior Design	Mall	NOTES:	SHEET TITLE							
GURU Open Air mall					- THIS DRAWING IS COPY RIGHT PROTECTED AND CAN NOT BE REPRODUCED WITHOUT THE WRITTEN APPROVAL OF THE ARCHITECT.	Fixture Layout							
					- ALL DIMENSIONS ARE IN CENTIMETERS UNLESS OTHERWISE MENTIONED, ALL DIMENSIONS MUST BE REVISED BY CONTRACTOR ON SITE.								
					01	01-12-2025	FOR REVIEW	A-105					
					00	27-11-2025	FOR REVIEW						
					Rev.	DATE	DESCRIPTION						
					Architecture Design Package								
					CAD DWG File						105.GURU-Open Air mall-Fixture Layout		
Drawn by						SB							
Checked by						OA							
Sheet No.													
						Date	01.12.2025	Rev.	01				
						Scale	1/100						

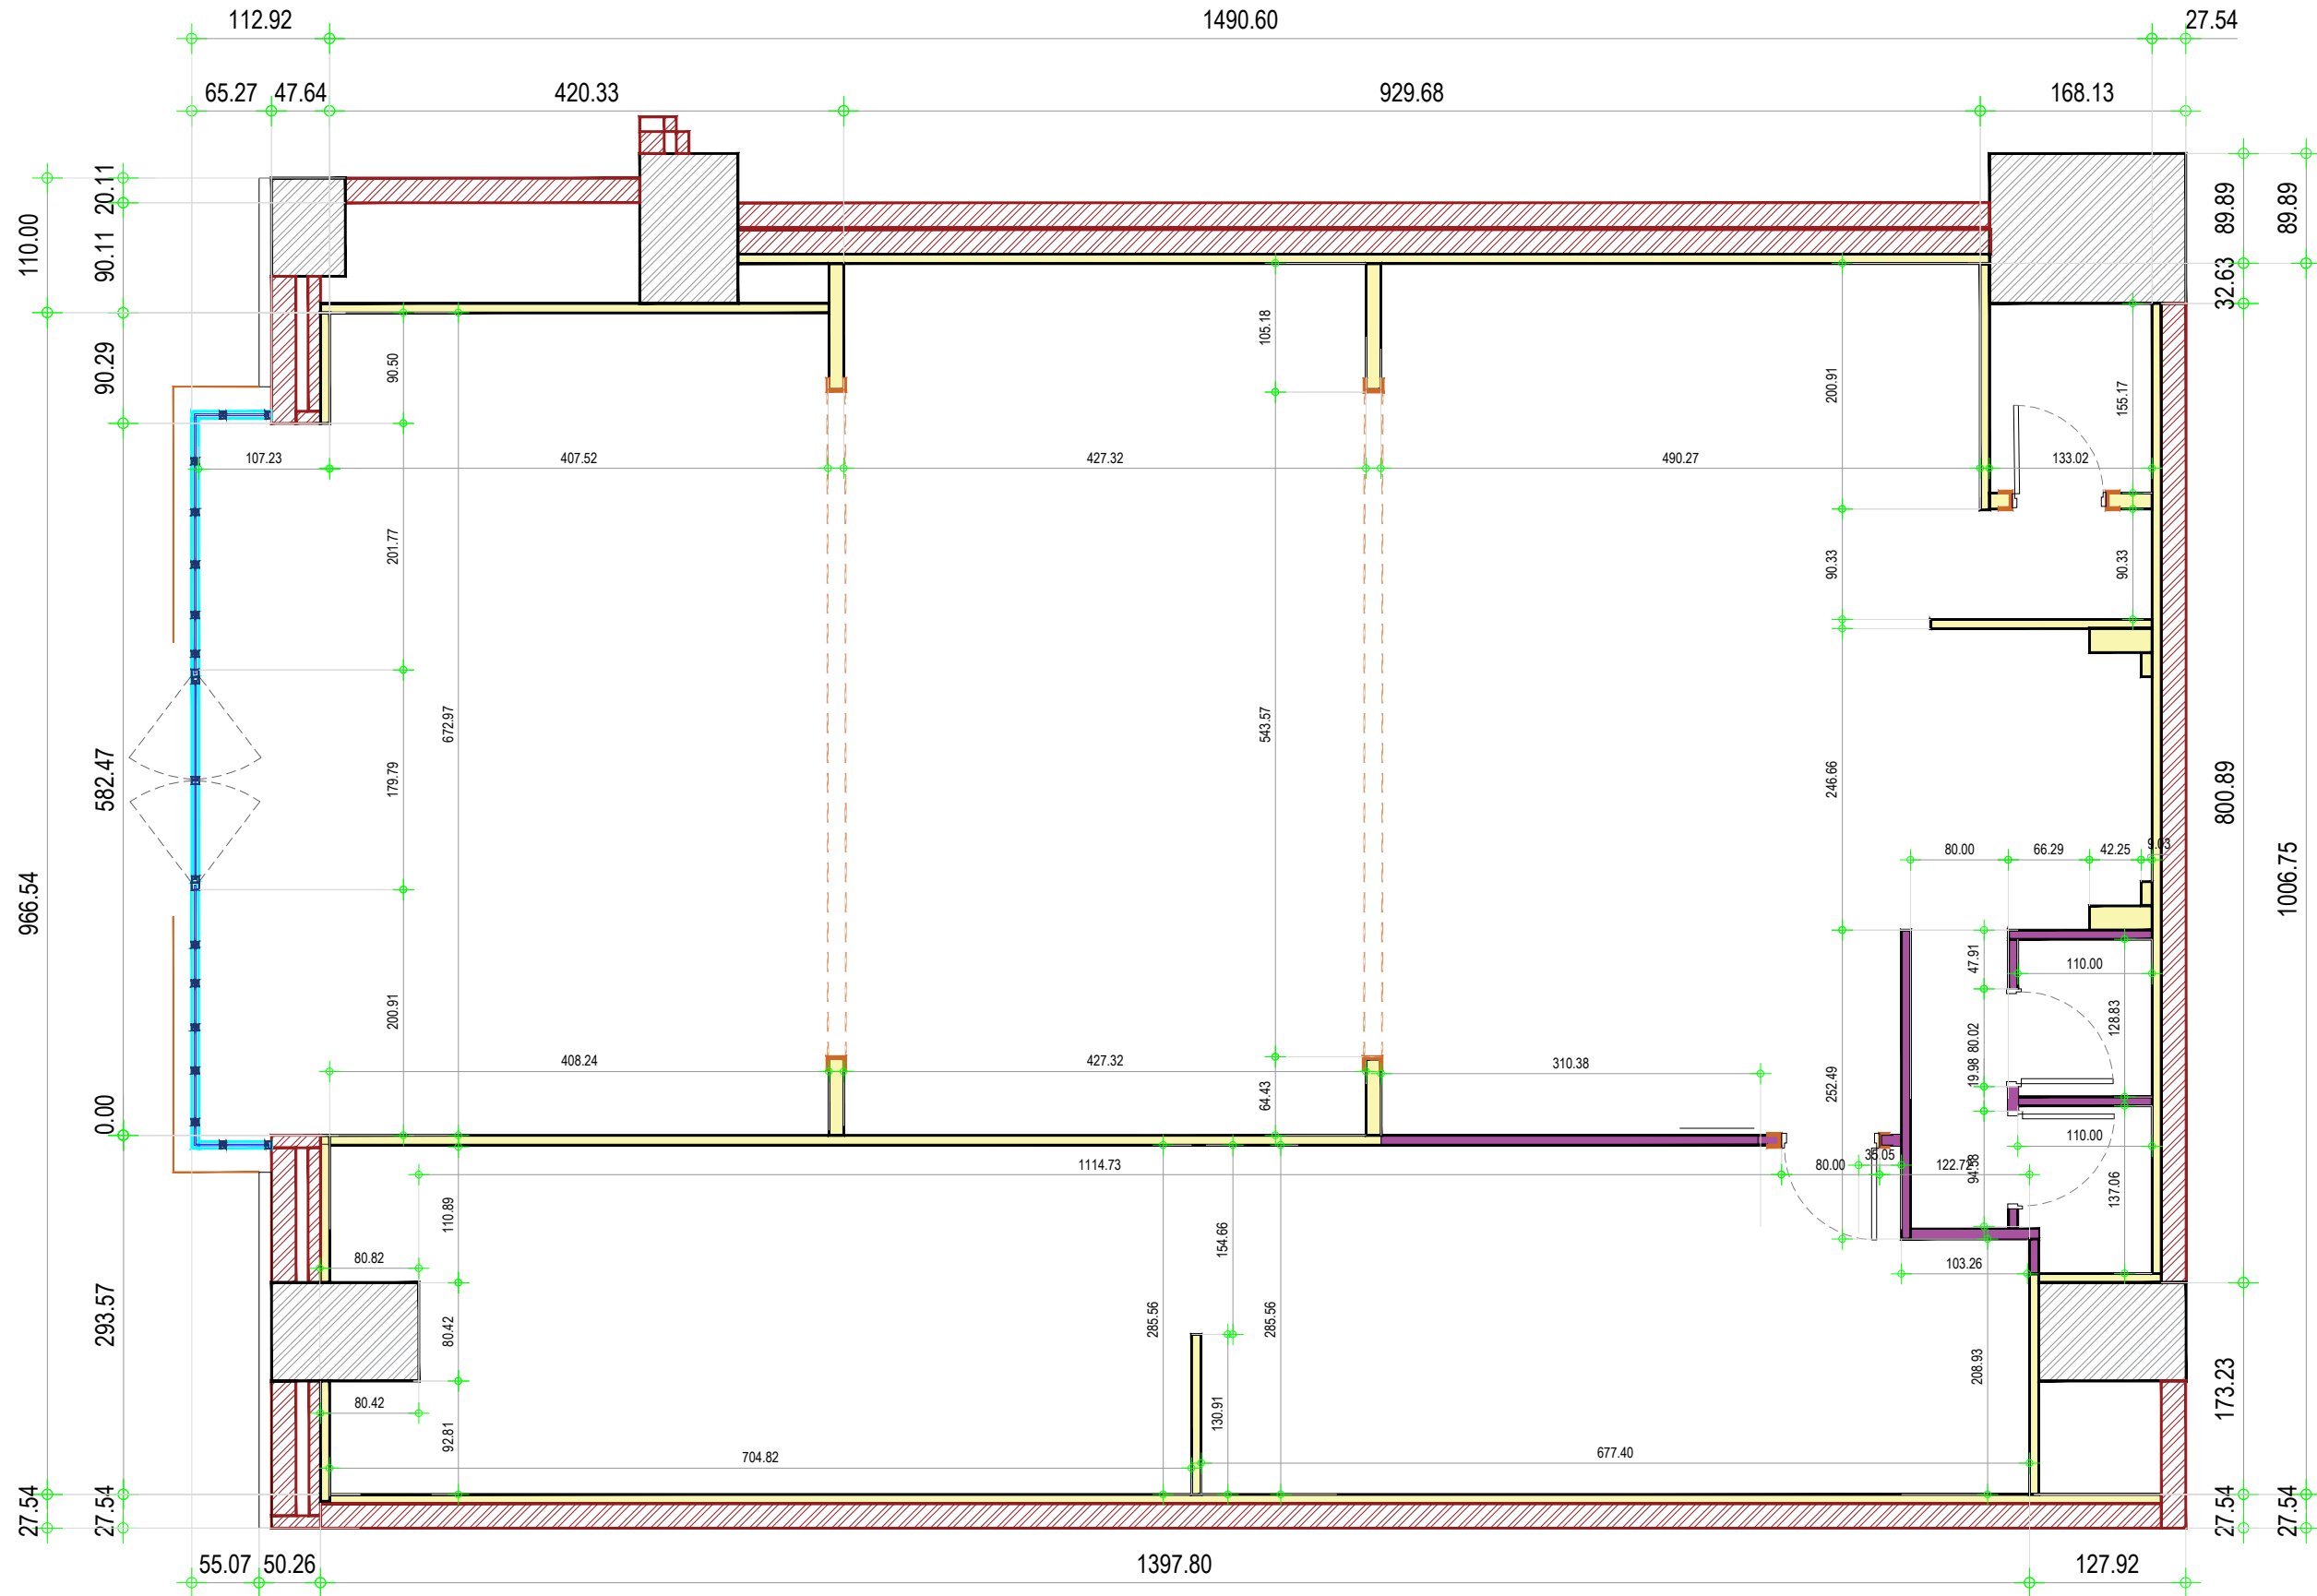

A
106
Construction plan


Project	Client	General Contractor	Interior Design	Mall				NOTES:	SHEET TITLE						
GURU Open Air mall							- THIS DRAWING IS COPY RIGHT PROTECTED AND CAN NOT BE REPRODUCED WITHOUT THE WRITTEN APPROVAL OF THE ARCHITECT. - ALL DIMENSIONS ARE IN CENTIMETERS UNLESS OTHERWISE MENTIONED. ALL DIMENSIONS MUST BE REVISED BY CONTRACTOR ON SITE.				Contraction plan				
								01	01-12-2025	FOR REVIEW					
								00	26-11-2025	FOR REVIEW					
								Rev.	DATE	DESCRIPTION					
								Architecture Design Package							
								CAD DWG File: 106.GURU-Open Air mall-Construction plan							
Drawn By: SB					Date	01.12.2025	Rev.	01							
Checked By: OA					Scale	1/100									
Sheet No.															

LIGHTING	
	CCTV
SPRINKLERS	
	Uprights Sprinkler
	BFC Sprinkler
FIRE ALARM	
	Smoke detector
	Fire alarm panel
	Manual call point
	Hooter Cum Strobe
	Below Smoke Detector
LIGHTING	
	Track Light
	Strip Light
	Passage light
HVAC	
	Return Grill
	Supply Grill

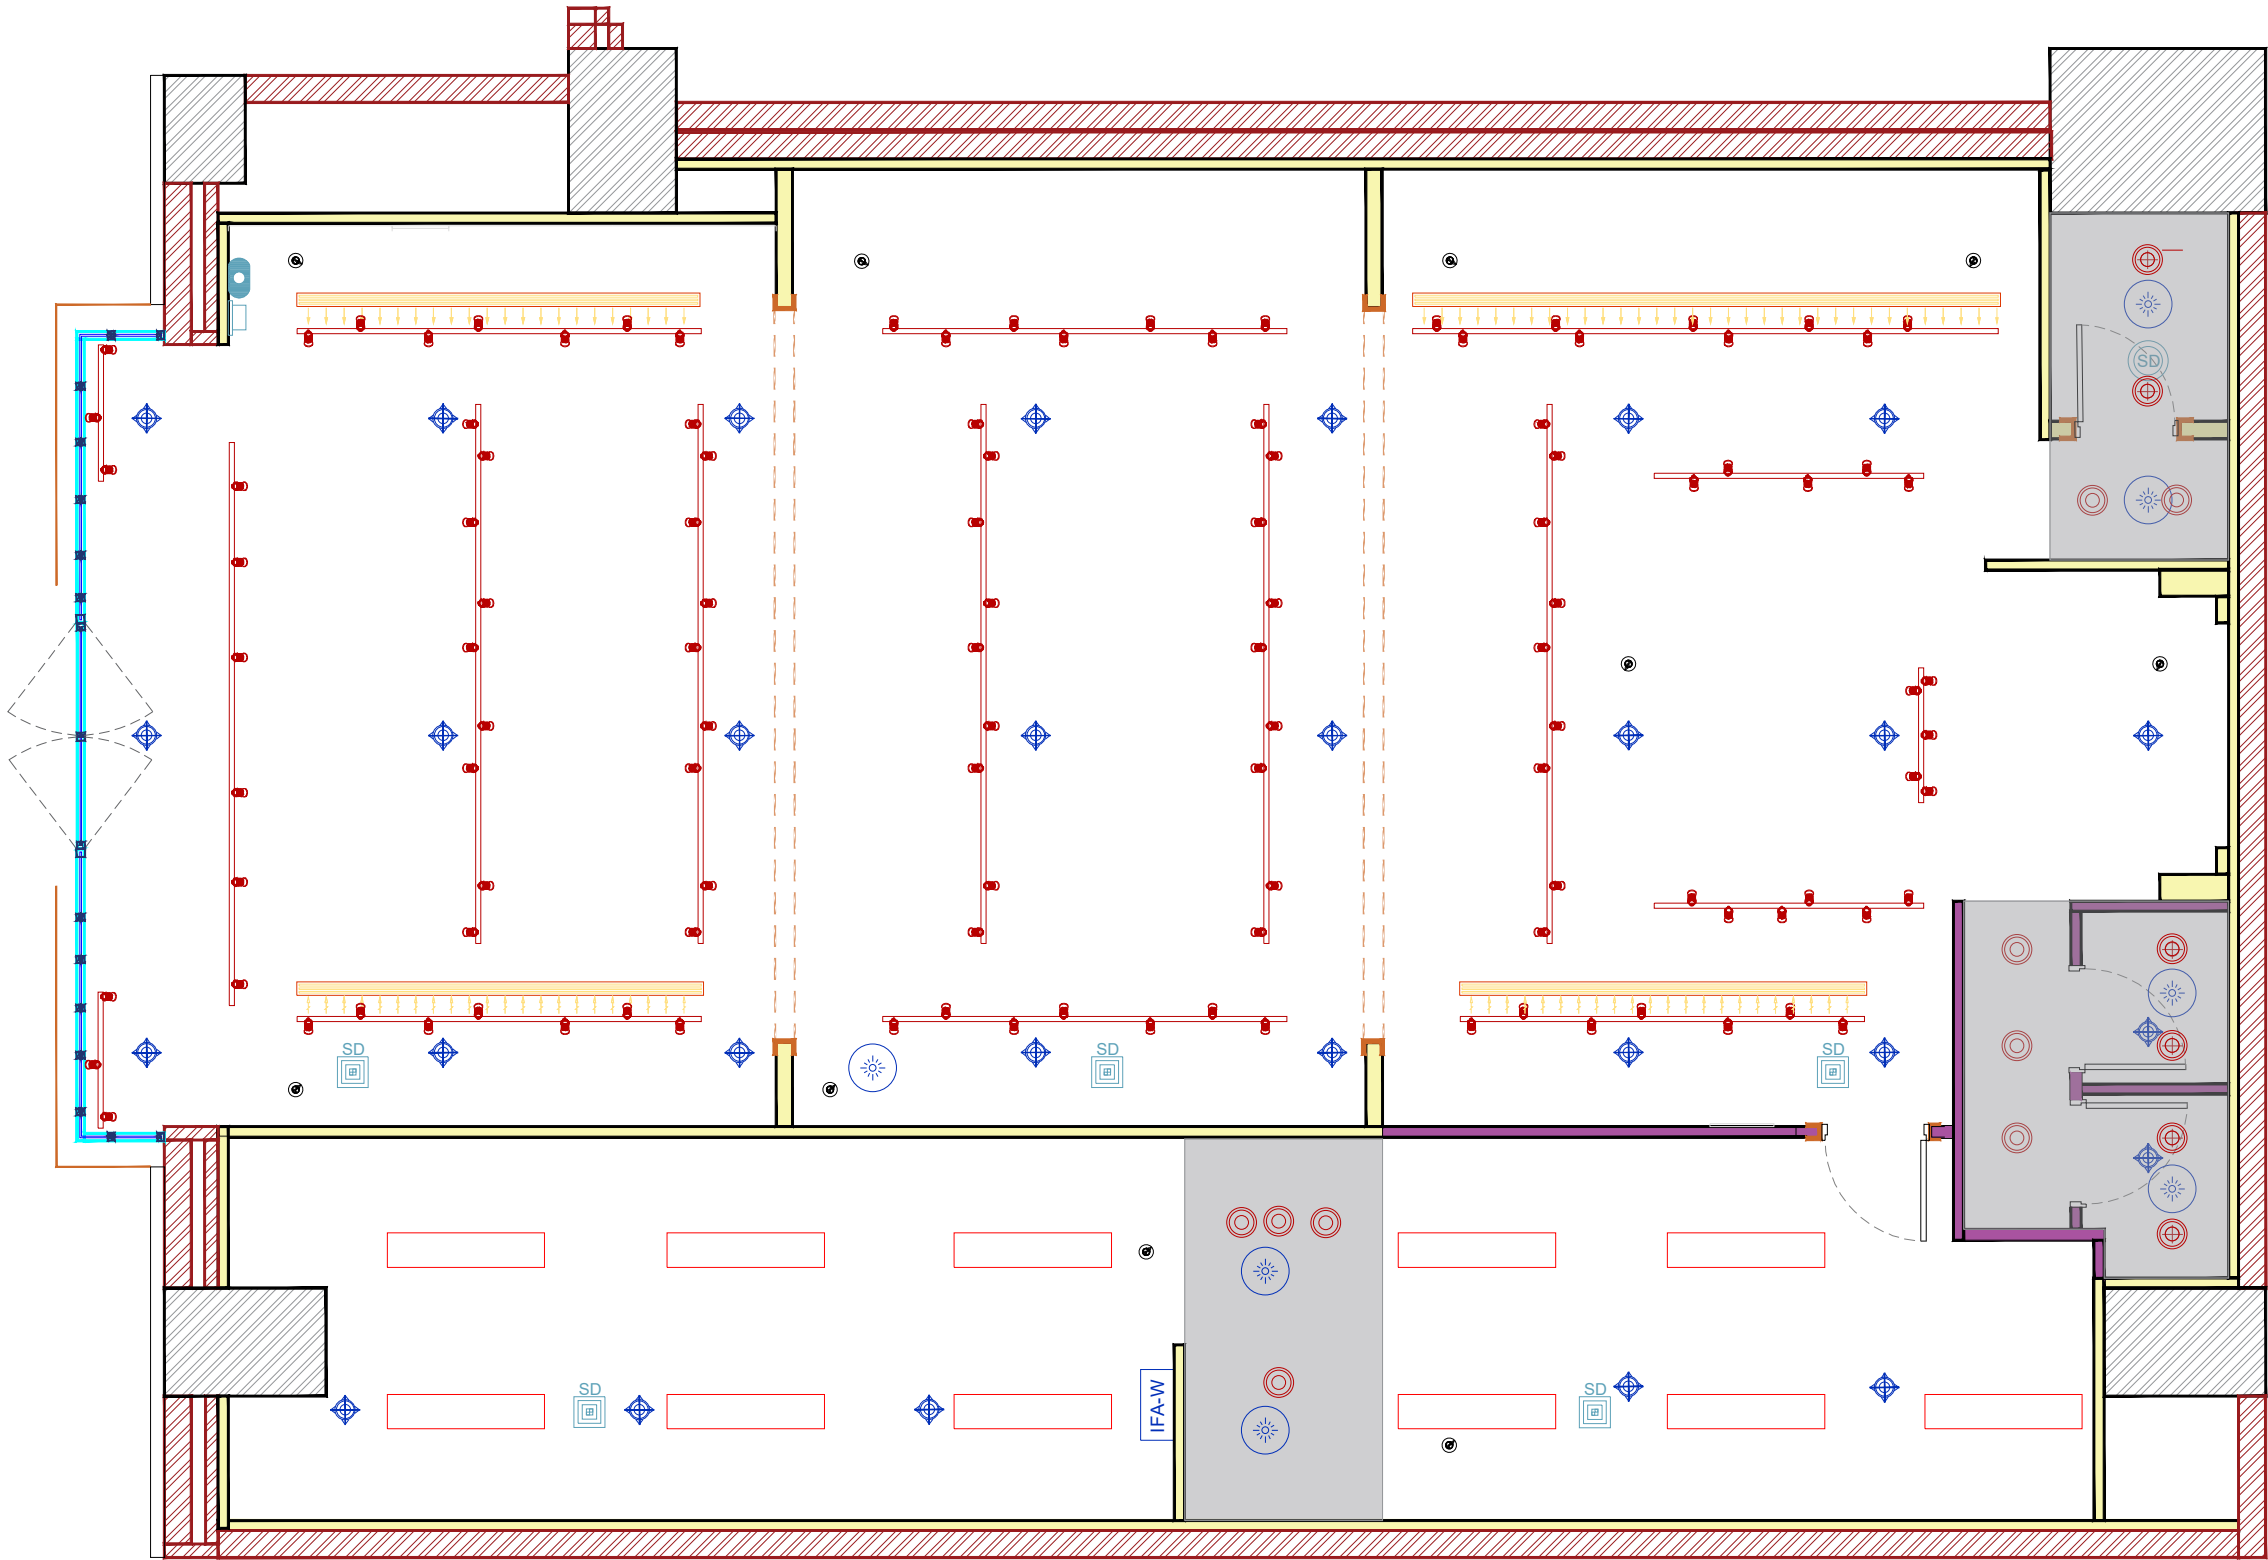


A
105
Fixture Layout

Project	Client	General Contractor	Interior Design	Mall	NOTES:	Rev.	DATE	DESCRIPTION	SHEET TITLE
GURU Open Air mall					THIS DRAWING IS COPY RIGHT PROTECTED AND CAN NOT BE REPRODUCED WITHOUT THE WRITTEN APPROVAL OF THE ARCHITECT. ALL DIMENSIONS ARE IN CENTIMETERS UNLESS OTHERWISE MENTIONED. ALL DIMENSIONS MUST BE REVISED BY CONTRACTOR ON SITE.	00	03-12-2025	FOR REVIEW	Reflected ceiling plan
Architecture Design Package									A-109
CAD DWG File Drawn by: SB Checked by: OA Sheet No.									Date: 03.12.2025 Scale: 1/100 Rev. 00

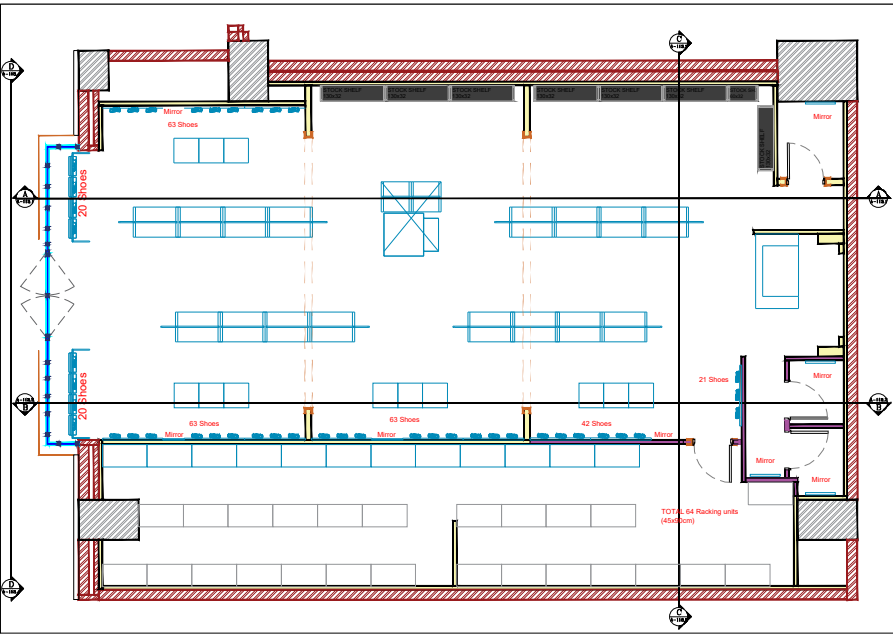

A
113.1


Elevation A-A
Key plan

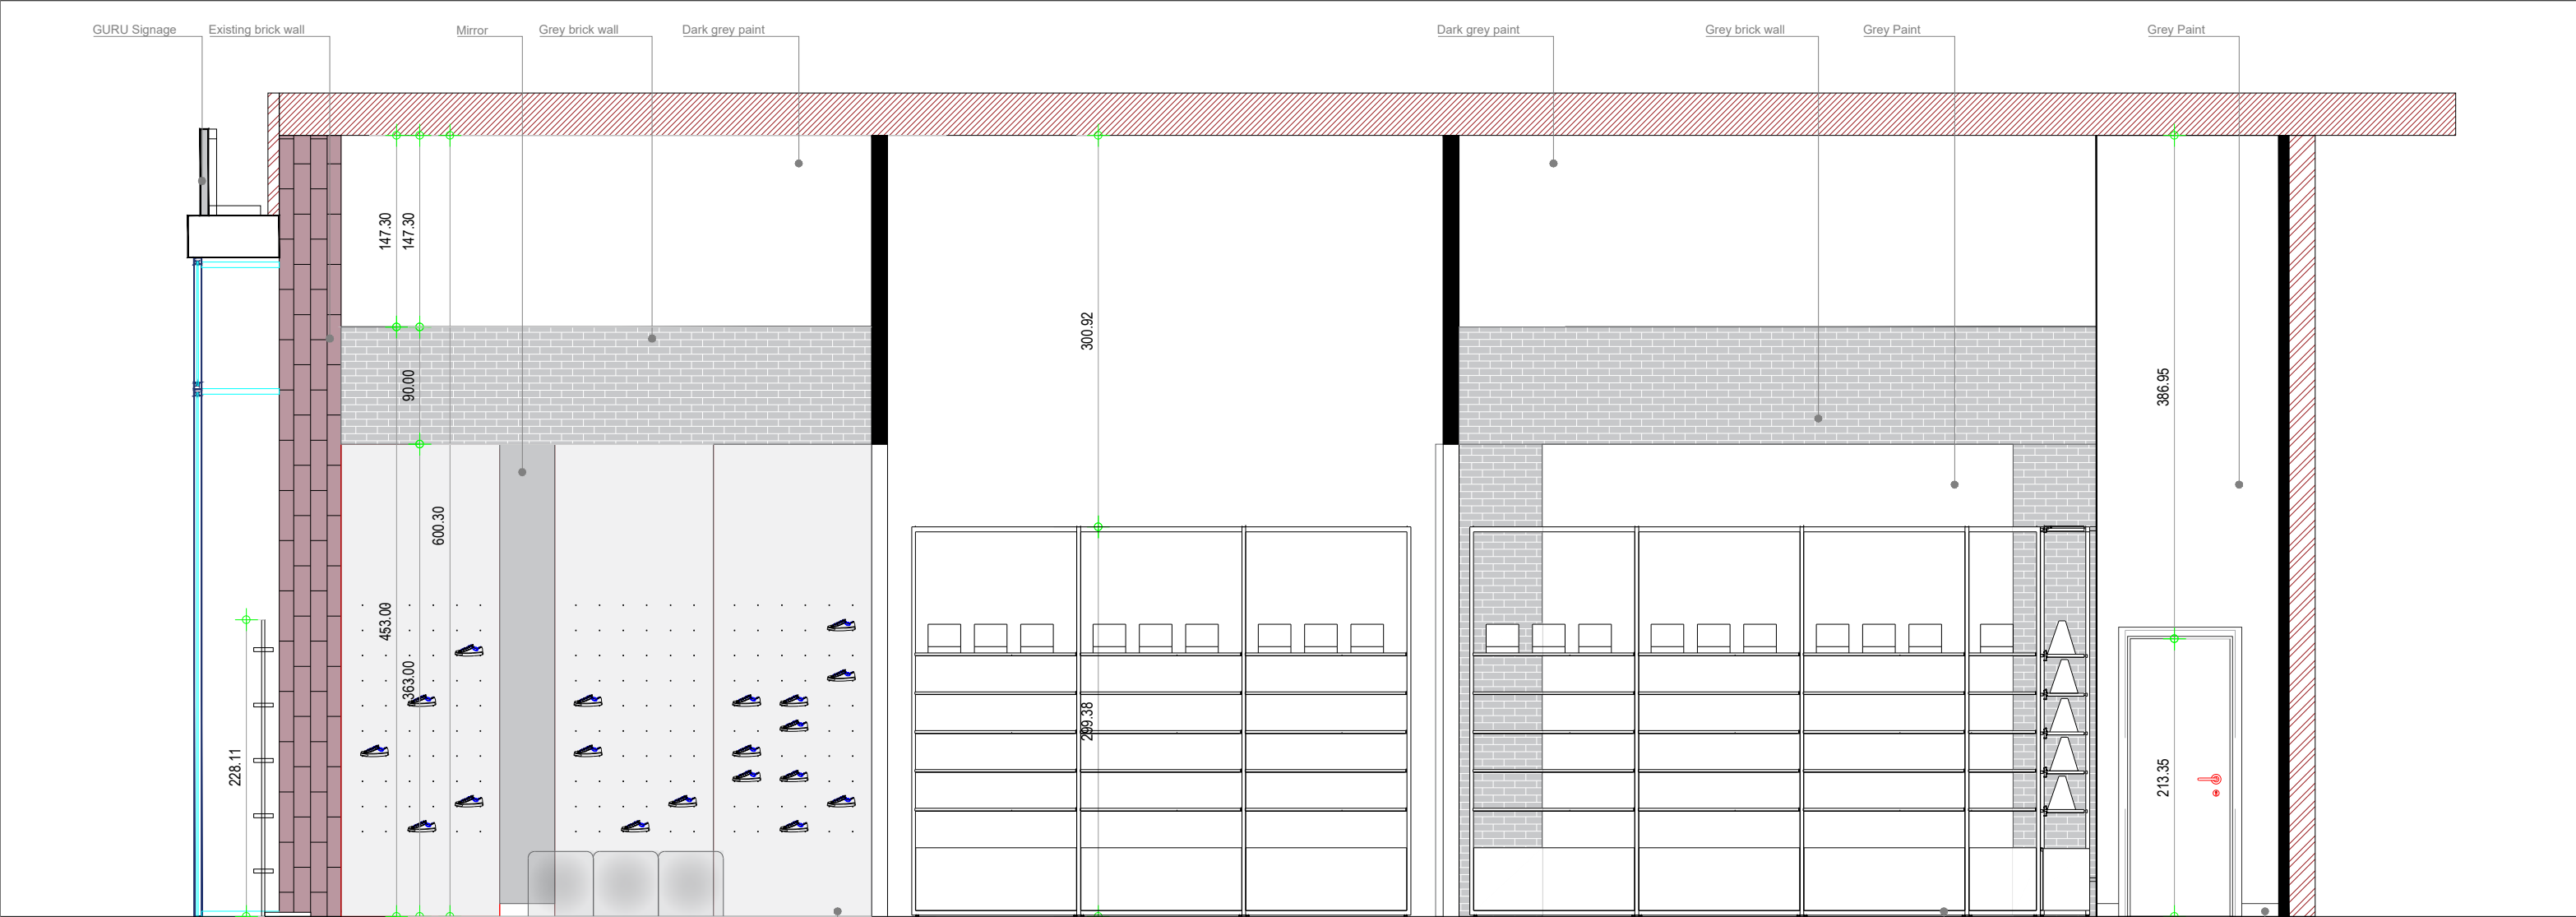

A
113.1


Elevation A-A

Project	Client	General Contractor	Interior Design	Mall	NOTES:	Rev.	DATE	DESCRIPTION	SHEET TITLE
GURU Open Air mall	GURU	sigma CONTRACTORS		OPEN AIR Mall	THIS DRAWING IS COPY RIGHT PROTECTED AND CAN NOT BE REPRODUCED WITHOUT THE WRITTEN APPROVAL OF THE ARCHITECT. ALL DIMENSIONS ARE IN CENTIMETERS UNLESS OTHERWISE MENTIONED, ALL DIMENSIONS MUST BE REVISED BY CONTRACTOR ON SITE.	00	03-12-2025	FOR REVIEW	Elevation A-A
									A-113.1
									Date 03. 12. 2025
									Scale 1/100
									Rev. 00

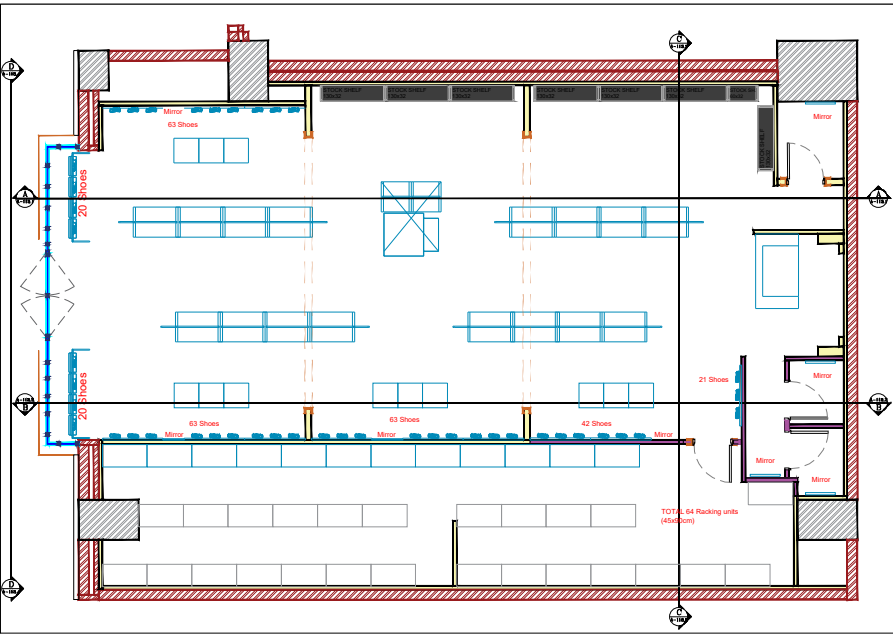

A
113.2


Elevation B-B
Key plan

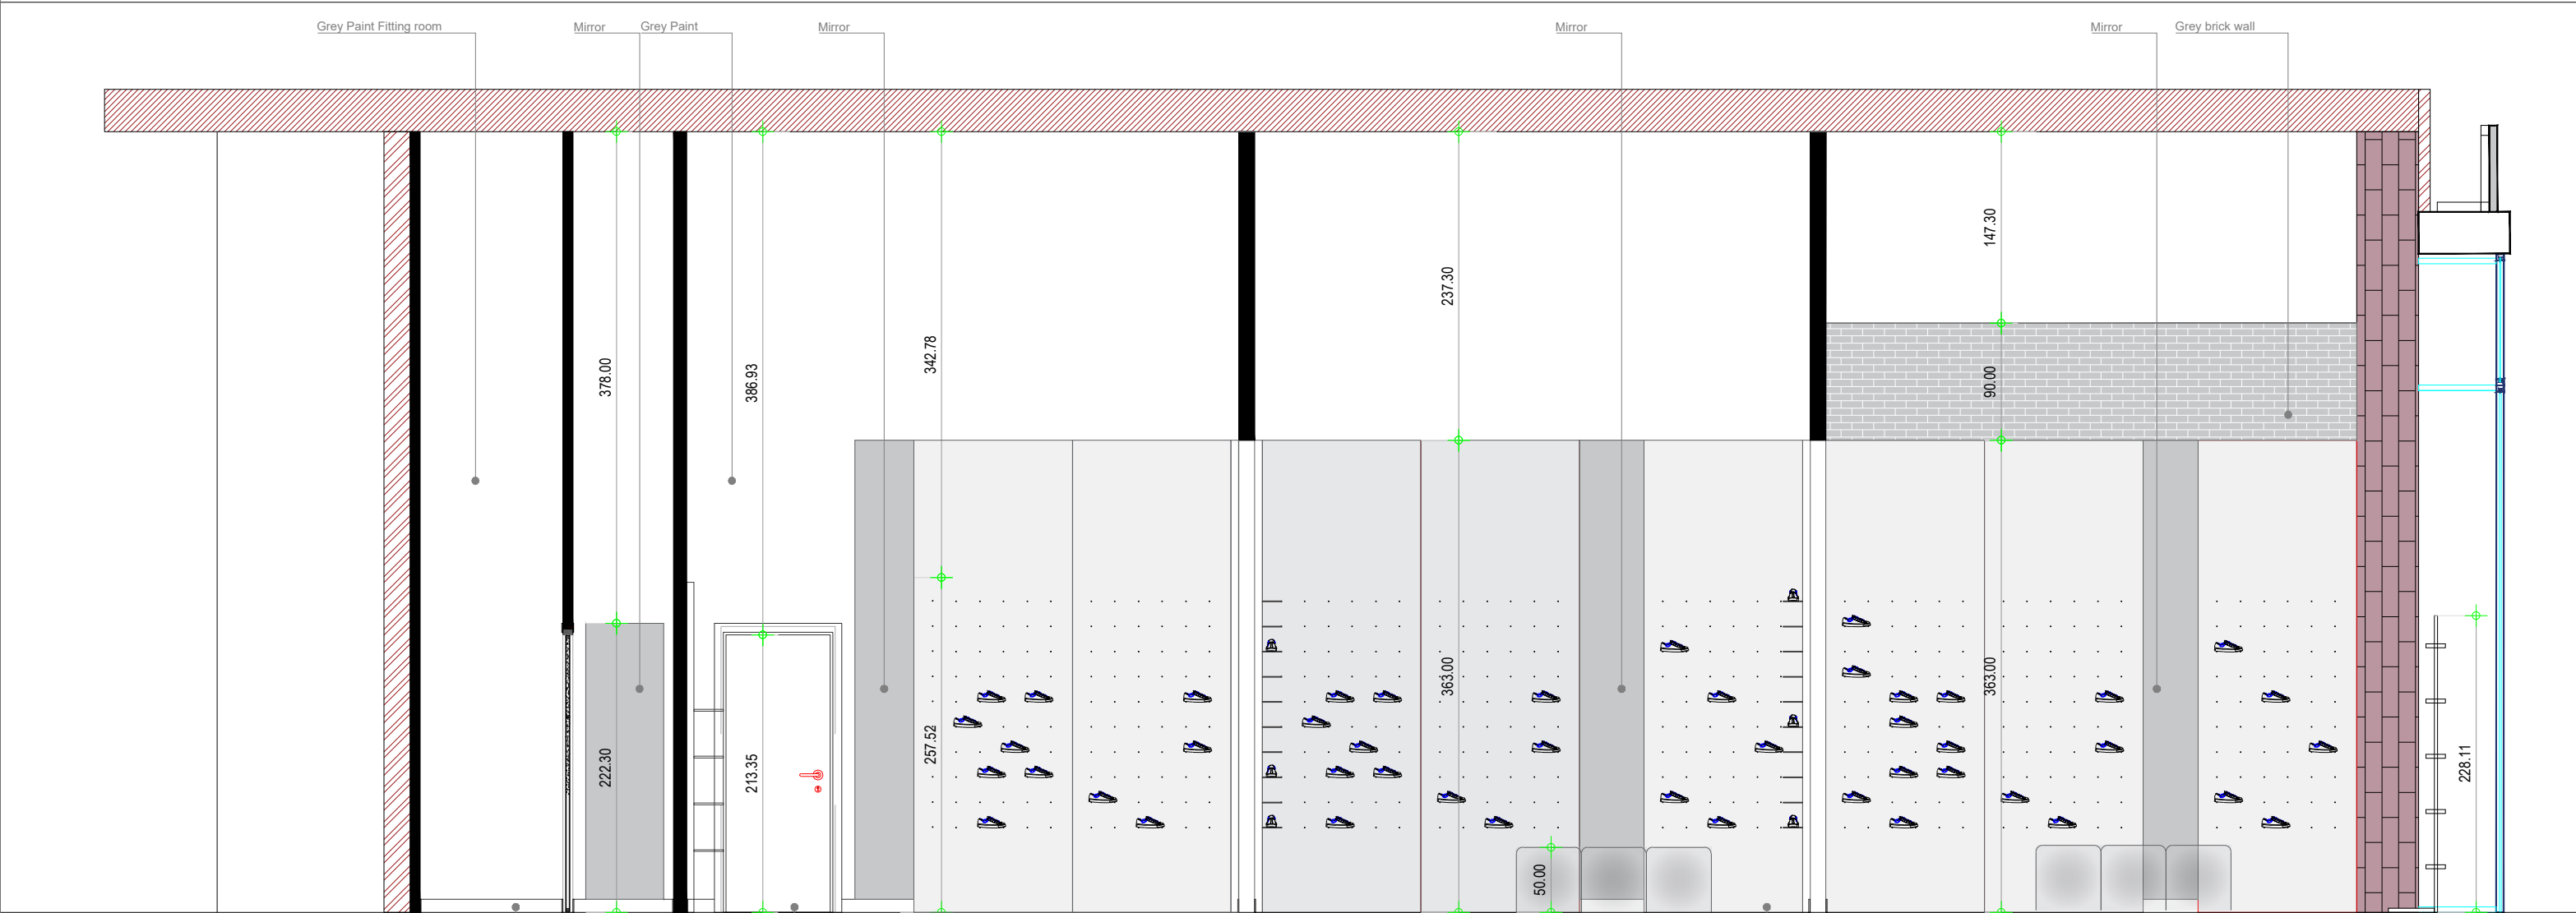

A
113.2


Elevation B-B

Project	Client	General Contractor	Interior Design	Mall	NOTES:	Rev.	DATE	DESCRIPTION	SHEET TITLE
GURU Open Air mall	GURU	sigma CONTRACTORS		OPEN AIR Mall	THIS DRAWING IS COPY RIGHT PROTECTED AND CAN NOT BE REPRODUCED WITHOUT THE WRITTEN APPROVAL OF THE ARCHITECT. ALL DIMENSIONS ARE IN CENTIMETERS UNLESS OTHERWISE MENTIONED, ALL DIMENSIONS MUST BE REVISED BY CONTRACTOR ON SITE.	00	03-12-2025	FOR REVIEW	Elevation B-B
					Architecture Design Package				A-113.2
					CAD DWG File Drawn by Checked by Sheet No.				Date 03. 12. 2025 Scale 1/100
					113.2.GURU-Open Air mall-Elevation B-B DA				Rev. 00

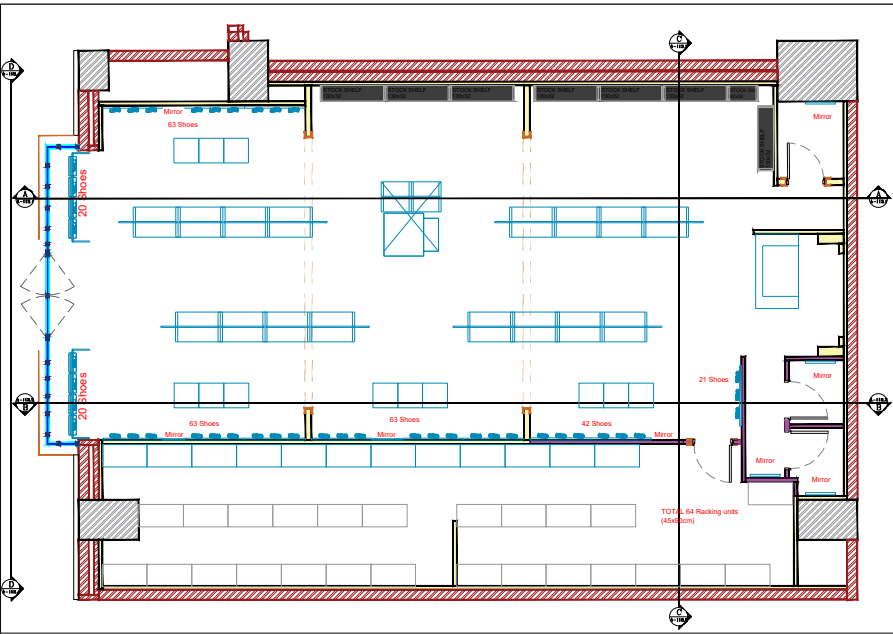

A
113.3


Elevation C-C
Key plan

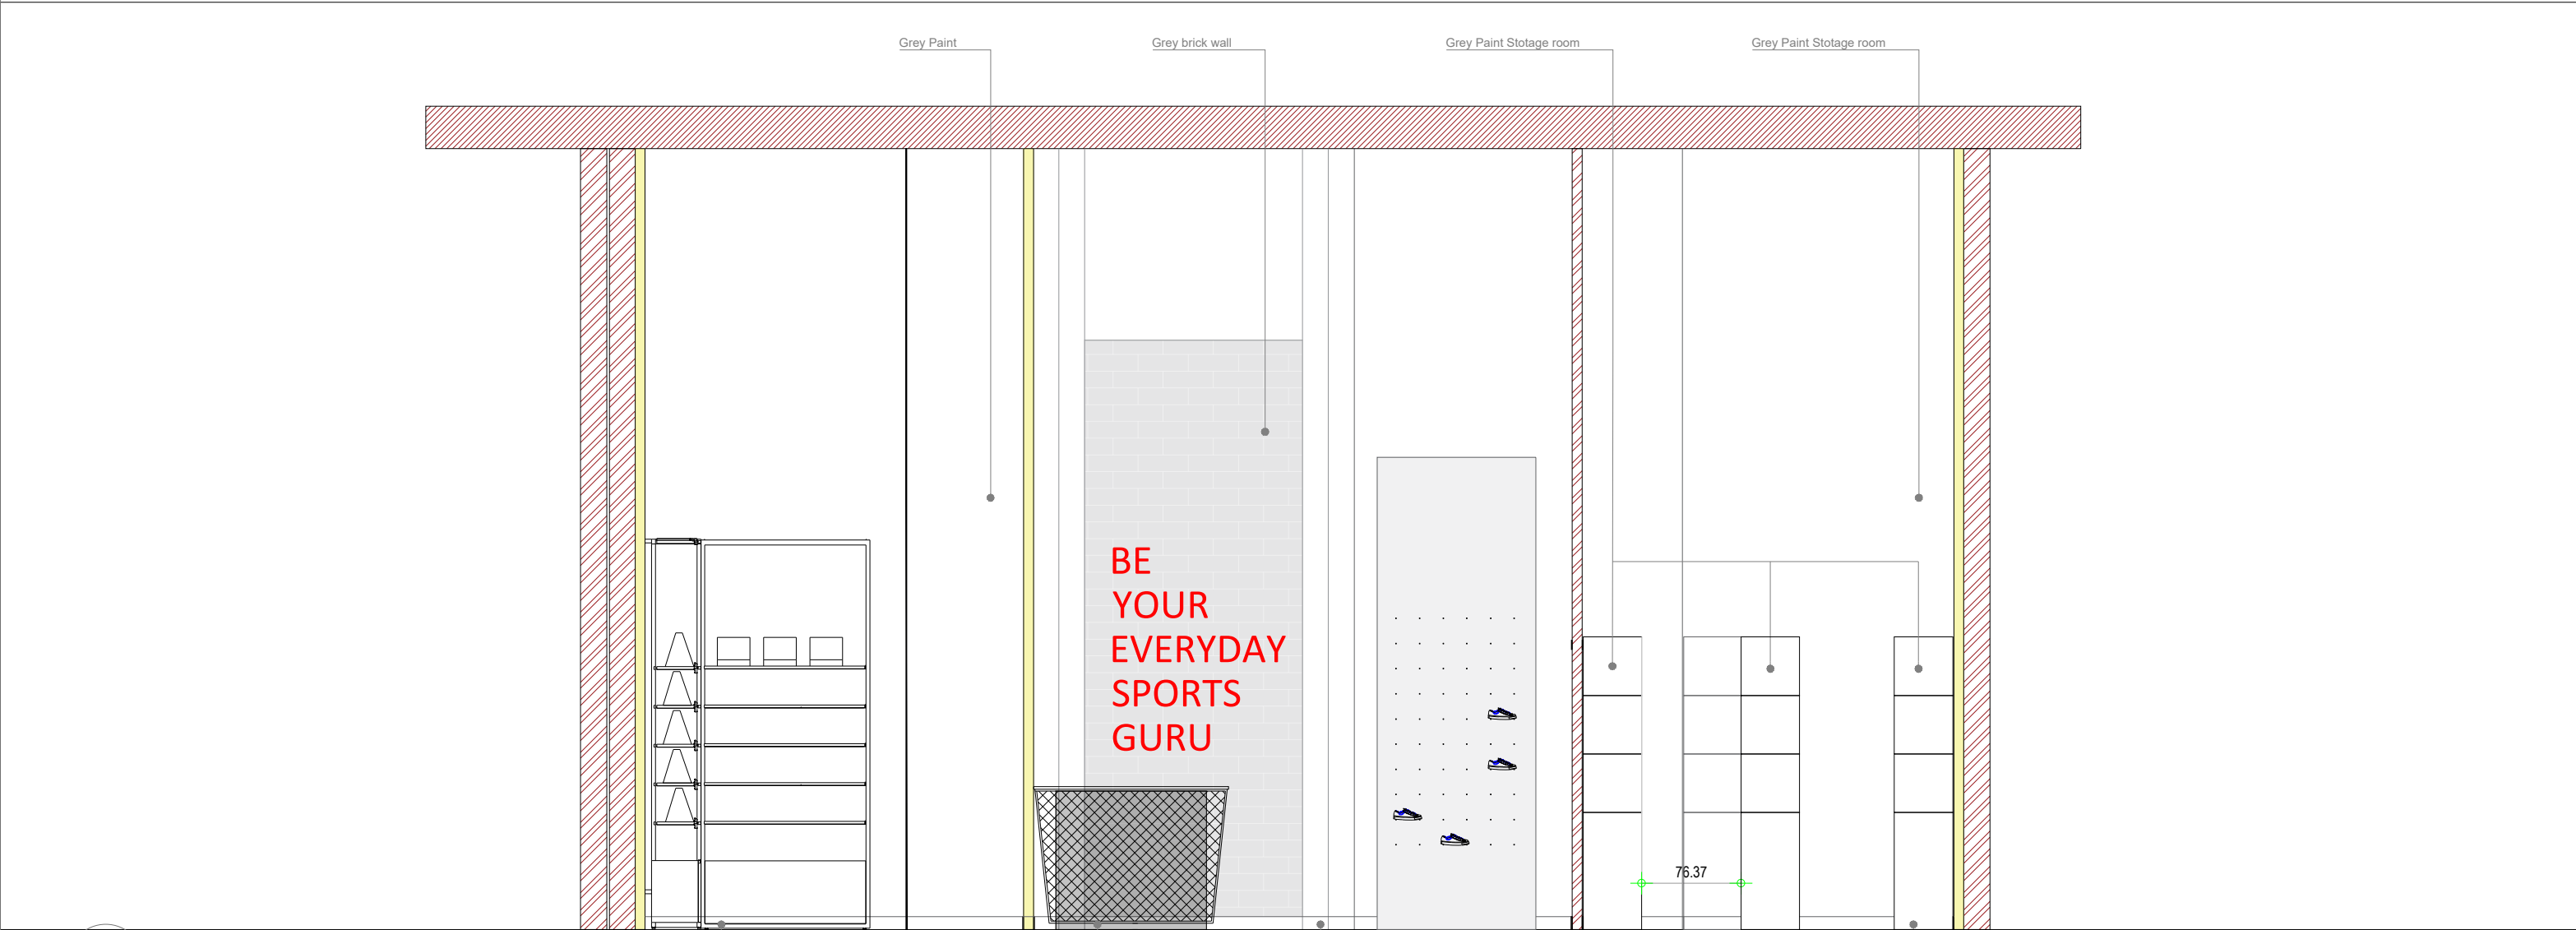

A
113.3


Elevation C-C

Project	Client	General Contractor	Interior Design	Mall	NOTES: - THIS DRAWING IS COPY RIGHT PROTECTED AND CAN NOT BE REPRODUCED WITHOUT THE WRITTEN APPROVAL OF THE ARCHITECT. - ALL DIMENSIONS ARE IN CENTIMETERS UNLESS OTHERWISE MENTIONED, ALL DIMENSIONS MUST BE REVISED BY CONTRACTOR ON SITE.	SHEET TITLE		
GURU Open Air mall						Elevation C-C		
						A-113.3		
						Architecture Design Package		
						CAD DWG File: 113.3.GURU-Open Air mall-Elevation C-C		
						Drawn by: SR		
						Checked by: DA		
						Sheet No:		
						Date: 03. 12. 2025	Rev. 00	
						Scale: 1/100		

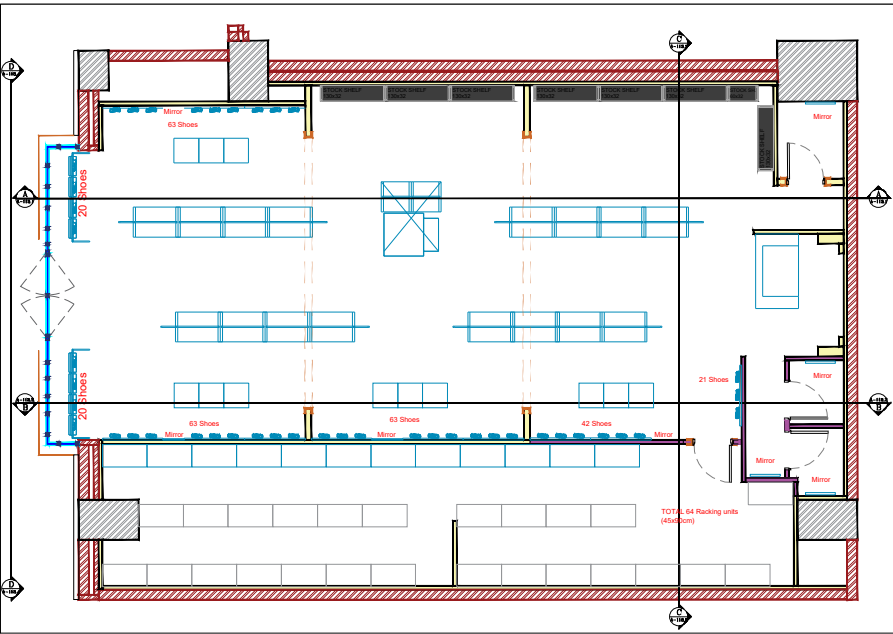

A
113.4

Elevation D-D
Key plan

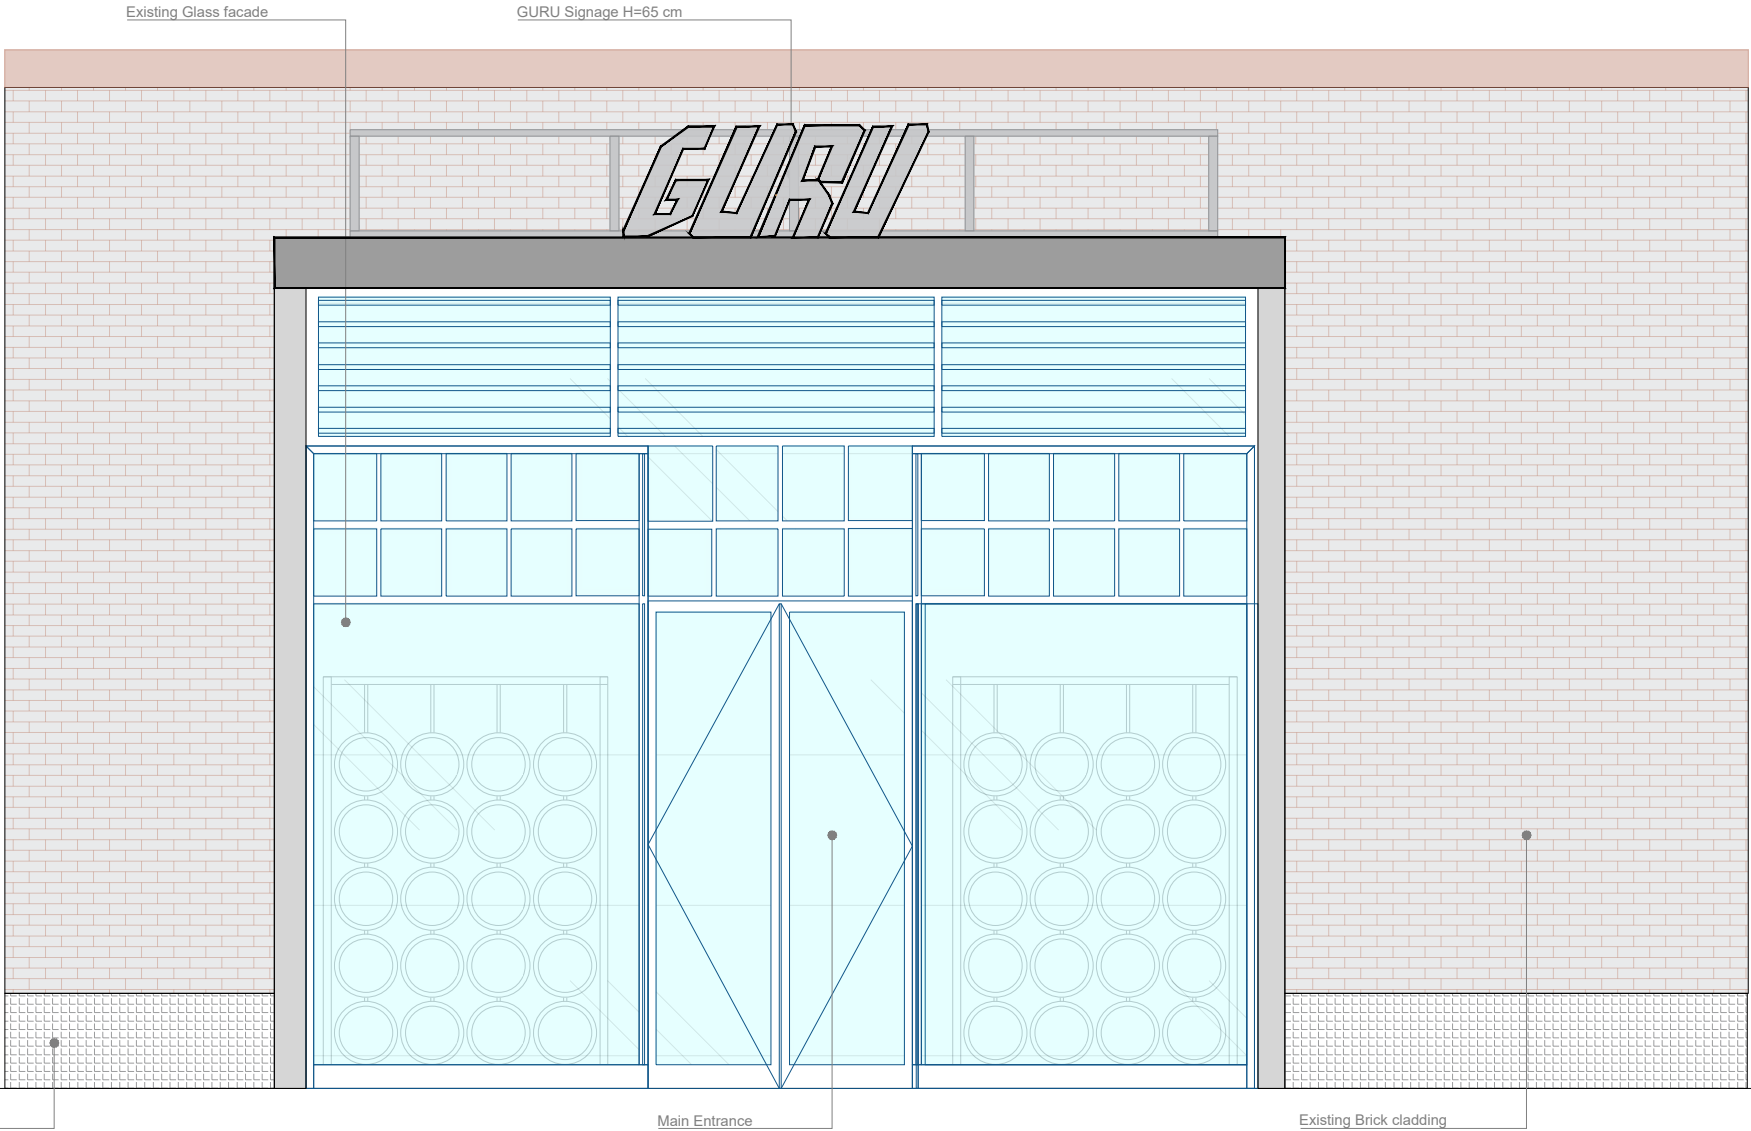

A
113.4

Elevation D-D

Project	Client	General Contractor	Interior Design	Mall	NOTES: - THIS DRAWING IS COPY RIGHT PROTECTED AND CAN NOT BE REPRODUCED WITHOUT THE WRITTEN APPROVAL OF THE ARCHITECT. - ALL DIMENSIONS ARE IN CENTIMETERS UNLESS OTHERWISE MENTIONED, ALL DIMENSIONS MUST BE REVISED BY CONTRACTOR ON SITE.	SHEET TITLE			
GURU Open Air mall						Elevation D-D			
						A-113.4			
						Architecture Design Package			
						CAD DWG File: 113.4.GURU-Open Air mall-Elevation D-D			
						Drawn by: SR			
						Checked by: DA			
						Sheet No.:			
						Date: 03. 12. 2025	Rev.:	00	
						Scale: 1/100			