


 

Patchi New HQ

Cairo Festival City - The Podium Offices - P1

Architectural Concept Design Submission

Wednesday February, **22nd** 2023 - **Rev.04**

ARCHITECTURAL DRAWINGS (CDS)			ISSUED					
No.	SHEET NO. :	DRAWINGS NAMES :	13 Feb	20 Feb	21 Feb	22 Feb		
1	A-101	Cover Page	01	02	03	04		
2	A-102	List Of Drawings	01	02	03	04		
3	A-103.1	Ref. Images	01	02		04		
4	A-103.2	Ref. Images	01	02		04		
5	A-103.3	Ref. Images	01	02		04		
6	A-103.4	Zoning Layout	01	02	03	04		
7	A-105.1	Fixtures Layout PSD	01	02	03	04		
8	A-105.2	Fixtures Layout	01	02	03	04		
9	A-106	Construction Layout	01	02	03	04		
10	A-107	Setting-Out Layout	01	02	03	04		
11	A-108	Flooring Layout	01	02	03	04		
12	A-109	RCP Layout	01	02	03	04		



SITE LOCATION: CFC THE PODIUM OFFICES - BUILDING P1 - SECOND FLOOR
TENANT GROSS AREA 330 SQM

A

102

List of Drawings

Project	Client	Design by	NOTES:				SHEET TITLE
Patchi New HQ CFC - Podium 2 Building P1			- THIS DRAWING IS COPY RIGHT PROTECTED AND CAN NOT BE REPRODUCED WITHOUT THE WRITTEN APPROVAL OF THE ARCHITECT. - ALL DIMENSIONS ARE IN CENTIMETERS UNLESS OTHERWISE MENTIONED. ALL DIMENSIONS MUST BE REVISED BY CONTRACTOR ON SITE.	04 22-02-2023 FOR REVIEW	03 21-02-2023 FOR REVIEW	02 20-02-2023 FOR REVIEW	List of Drawings
				Rev.	DATE	DESCRIPTION	A-102
				Concept Design Submission			
				CAD DWG file	102.Patchi-CFC-A-List of drawings		Date 21 . 02 . 2023
				Drawn by	JH		Rev. 04
				Checked by			Scale 1/50
				Sheet No.			

Reception




Workstations



Managers' Rooms

CEILING

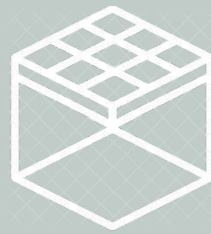

Meeting Room





A
103.1
Ref. Images


Project	Client	Design by
Patchi New HQ CFC - Podium 2 Building P1		

©Copyright 2018, FINE TOUCH CONTRACTORS, 11 Off Omar Ibn ELKhattab str.- Apart.603 - Ramu Buildings - Heliopolis 11341-Cairo - Egypt.

NOTES:		SHEET TITLE				
- THIS DRAWING IS COPY RIGHT PROTECTED AND CAN NOT BE REPRODUCED WITHOUT THE WRITTEN APPROVAL OF THE ARCHITECT.		Reference Images				
- ALL DIMENSIONS ARE IN CENTIMETERS UNLESS OTHERWISE MENTIONED. ALL DIMENSIONS MUST BE REVISED BY CONTRACTOR ON SITE.						
04	22-02-2023			FOR REVIEW		
03	21-02-2023			FOR REVIEW		
02	20-02-2023			FOR REVIEW		
01	13-02-2023			FOR REVIEW		
Rev.	DATE			DESCRIPTION		
Concept Design Submission		A-103.1				
CAD DWG file	103.Patchi-CFC-A-Ref. Images		Date	21. 02. 2023	Rev.	04
Drawn by	JH		Scale	1/50		
Checked by						
Sheet No.						

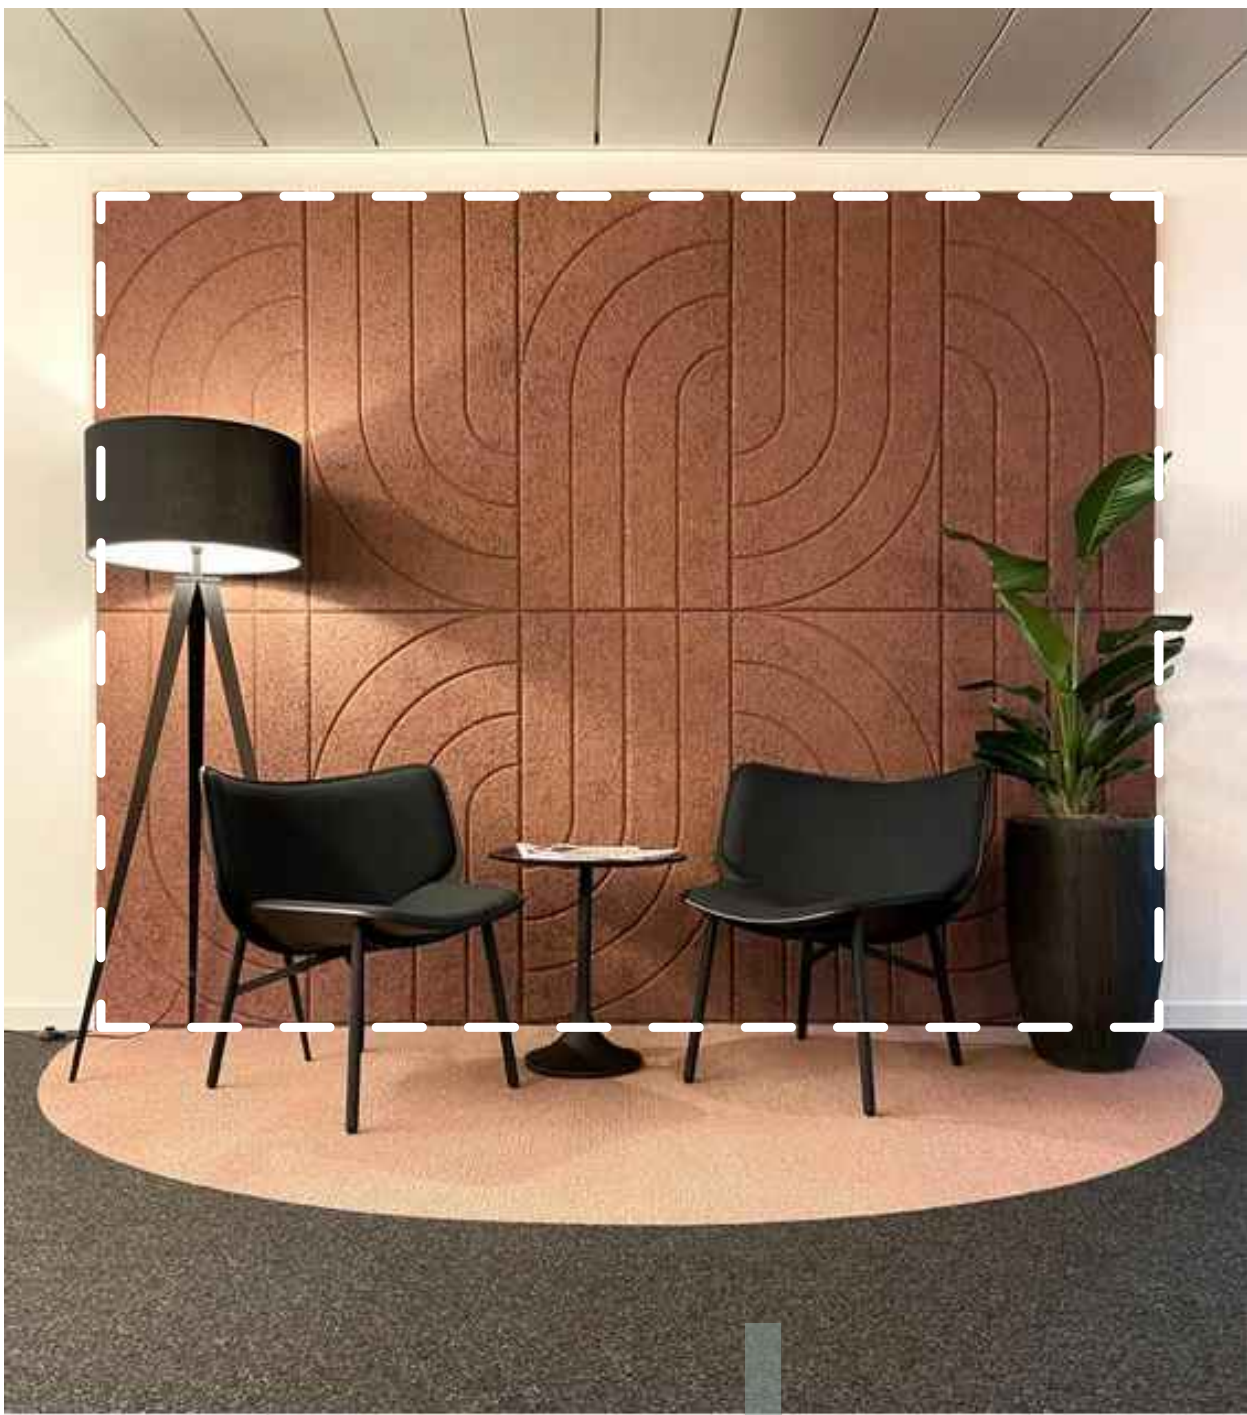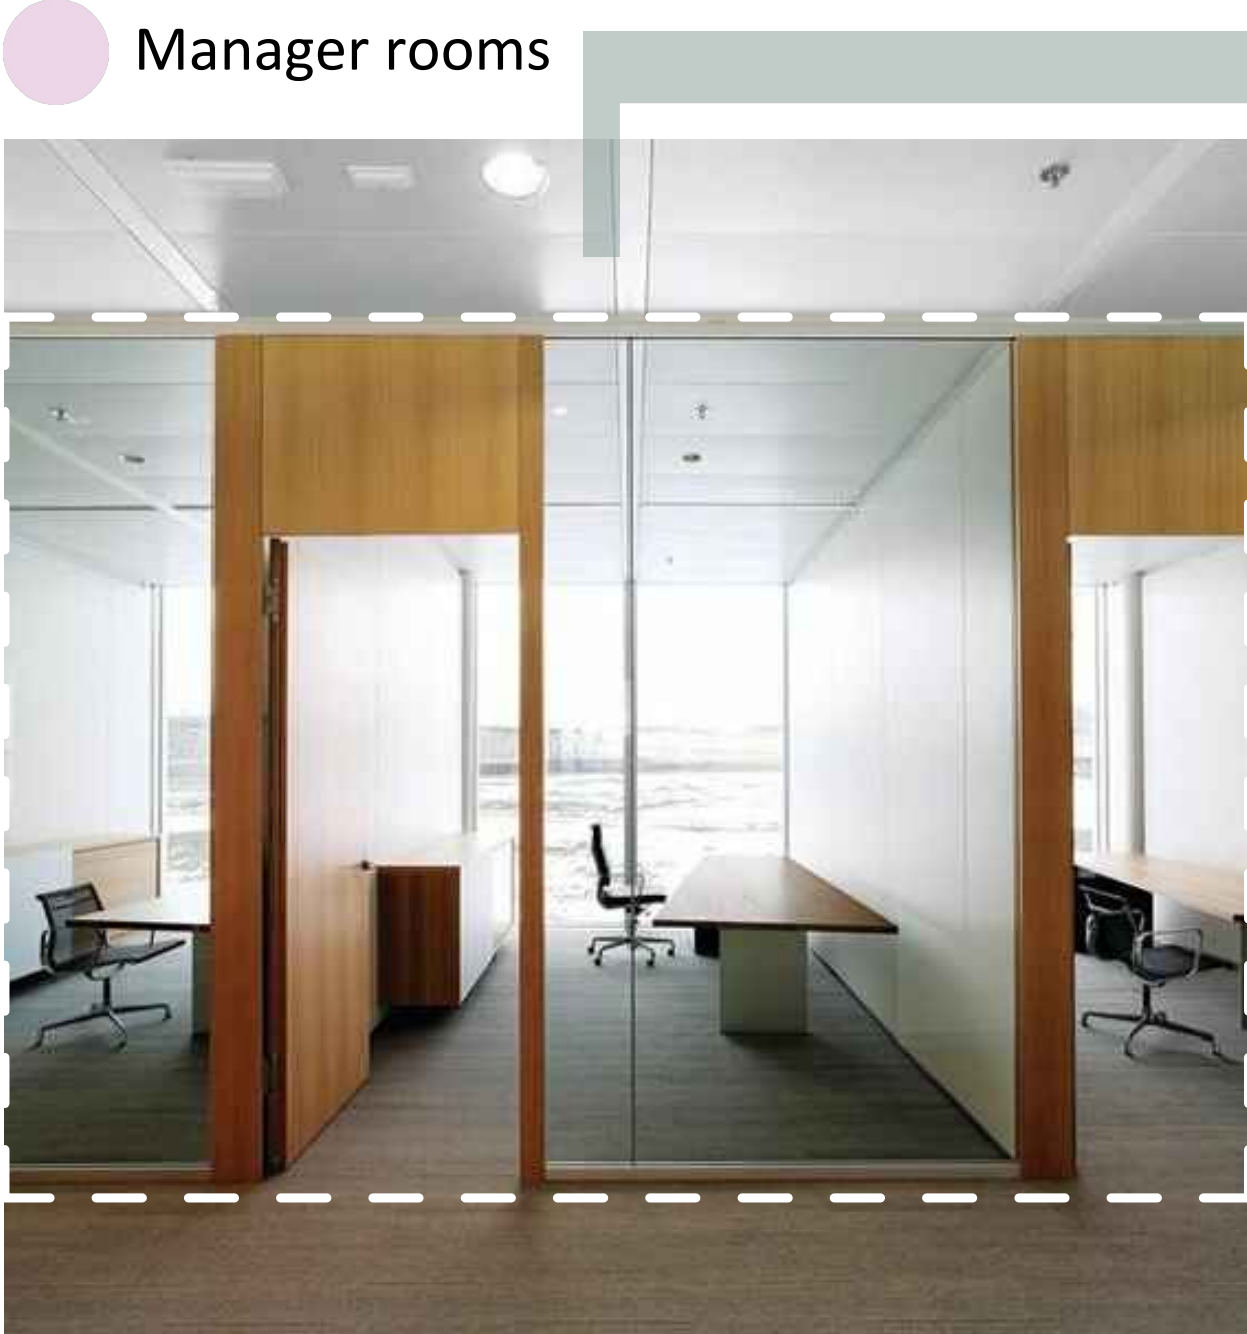

Workstations Area

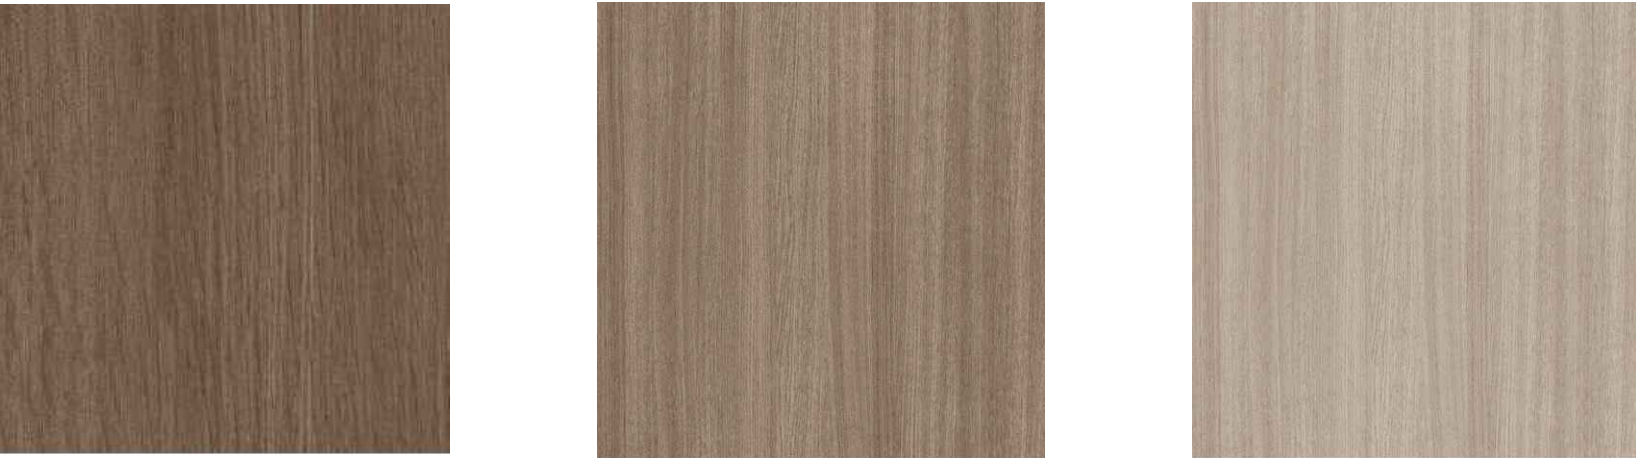

A
103.2 Ref. Images

Project	Client	Design by
Patchi New HQ CFC - Podium 2 Building P1		

© Copyright 2018, FINE TOUCH CONTRACTORS, 11 Off Omar Ibn ELKhattab str.- Apart.603 - Ramu Buildings - Heliopolis 11341-Cairo - Egypt.

NOTES:			SHEET TITLE	
- THIS DRAWING IS COPY RIGHT PROTECTED AND CAN NOT BE REPRODUCED WITHOUT THE WRITTEN APPROVAL OF THE ARCHITECT. - ALL DIMENSIONS ARE IN CENTIMETERS UNLESS OTHERWISE MENTIONED. ALL DIMENSIONS MUST BE REVISED BY CONTRACTOR ON SITE.			Reference Images	
Rev. DATE DESCRIPTION			A-103.2	
CAD DWG file			Date	21 . 02 . 2023
Drawn by			Rev.	04
Checked by			Scale	
Sheet No.			1/50	

Meeting Room




Workstations

FLOORING



Engineered Wood

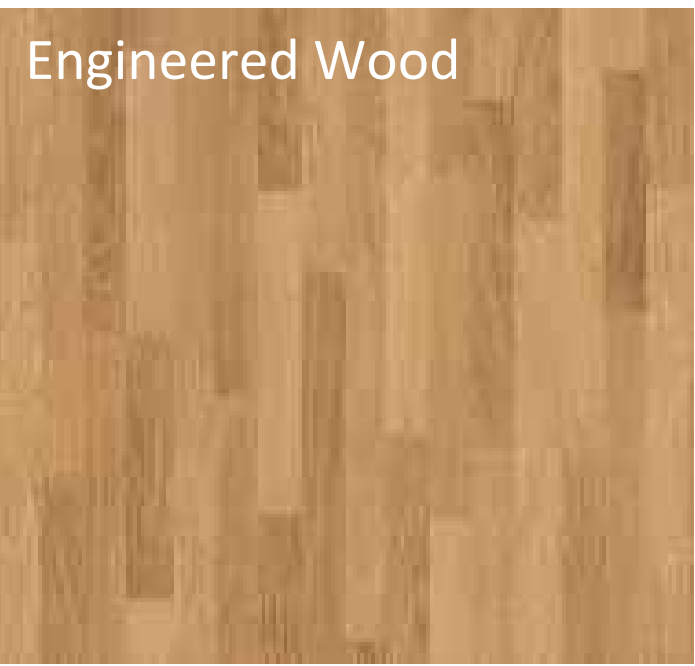

Reception

Pattern TBC



Corridor

Carpet tiles TBC



Workstations

Pattern TBC



Meeting Room

Porcelain tiles



Services

A
103.3

Ref. Images


Project	Client	Design by
Patchi New HQ CFC - Podium 2 Building P1		

© Copyright 2018, FINE TOUCH CONTRACTORS, 11 Off Omar Ibn ELKhattab str.- Apart.603 - Ramu Buildings - Heliopolis 11341-Cairo - Egypt.

NOTES:			SHEET TITLE	
- THIS DRAWING IS COPY RIGHT PROTECTED AND CAN NOT BE REPRODUCED WITHOUT THE WRITTEN APPROVAL OF THE ARCHITECT. - ALL DIMENSIONS ARE IN CENTIMETERS UNLESS OTHERWISE MENTIONED. ALL DIMENSIONS MUST BE REVISED BY CONTRACTOR ON SITE.			Reference Images	
Rev. DATE DESCRIPTION			A-103.3	
CAD DWG file 103.Patchi-CFC-A-Ref. Images			Date 21 . 02 . 2023	Rev. 04
Drawn by JH			Scale 1/50	
Checked by				
Sheet No.				





- Reception
- Manager Rooms x4
- Workstations 18PAX
- Elec. & IT Room
- Pantry
- Meeting Room x8
- Toilets
- Storage & Printing Room

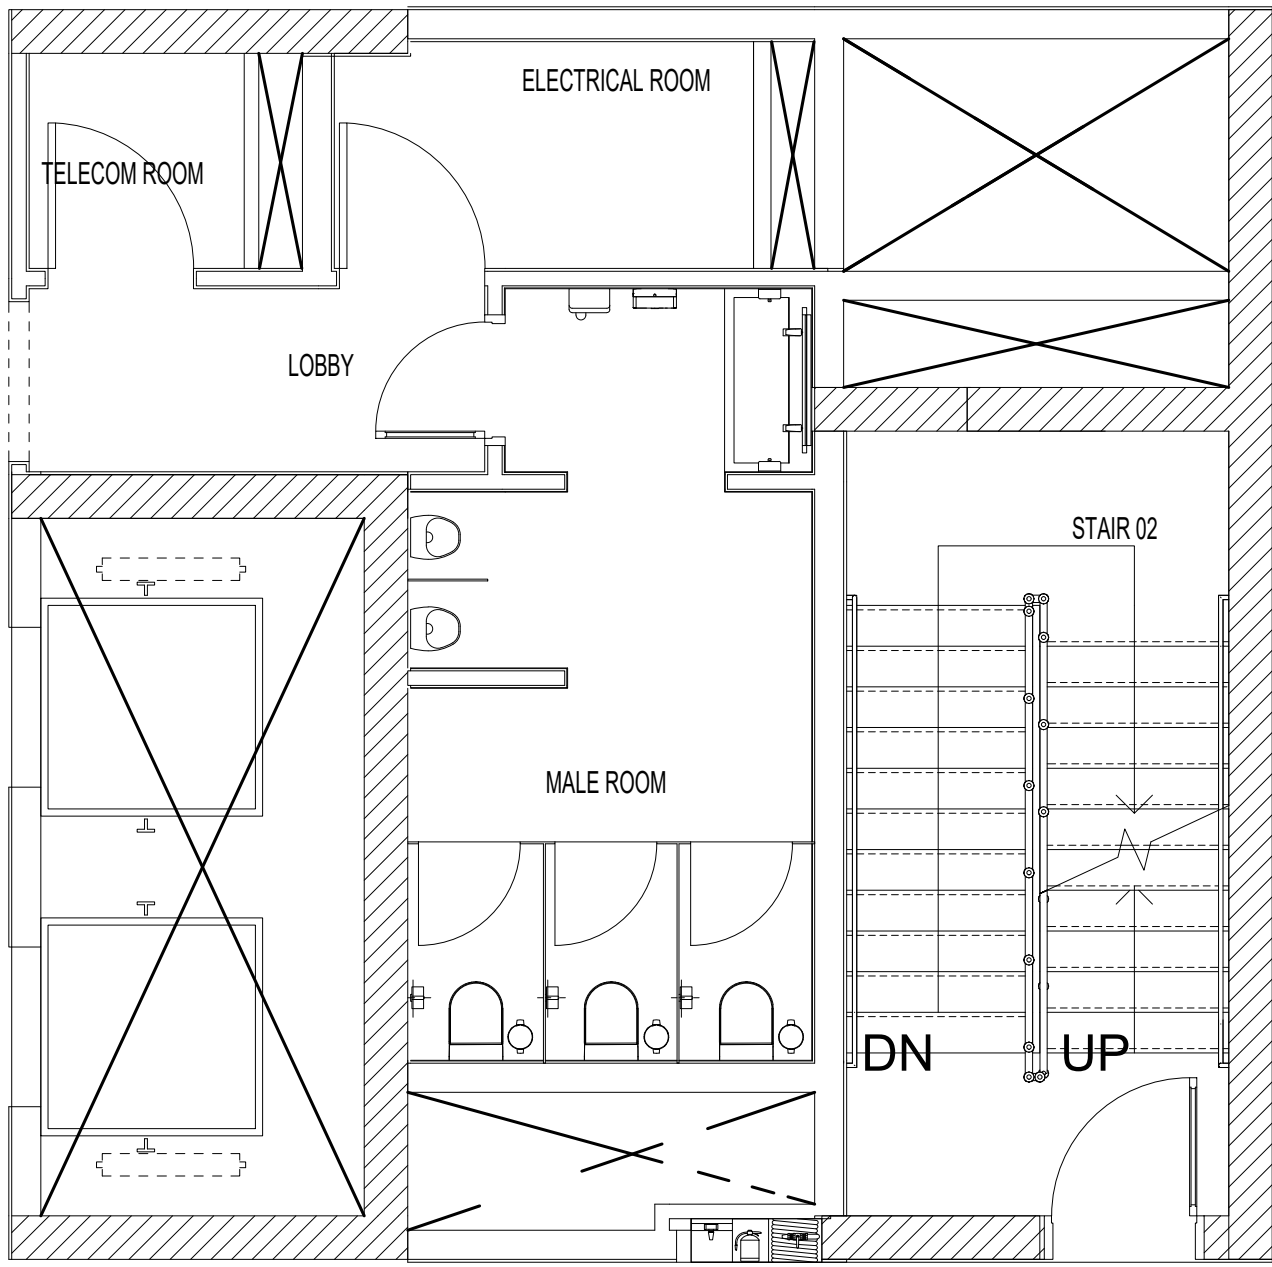

A
103.4


Zoning Layout
Second Floor

Project	Client	Design by	NOTES:	SHEET TITLE						
Patchi New HQ CFC - Podium 2 Building P1			- THIS DRAWING IS COPY RIGHT PROTECTED AND CAN NOT BE REPRODUCED WITHOUT THE WRITTEN APPROVAL OF THE ARCHITECT.							
			- ALL DIMENSIONS ARE IN CENTIMETERS UNLESS OTHERWISE MENTIONED. ALL DIMENSIONS MUST BE REVISED BY CONTRACTOR ON SITE.	04	22-02-2023	FOR REVIEW				
				03	21-02-2023	FOR REVIEW				
				02	20-02-2023	FOR REVIEW				
				01	13-02-2023	FOR REVIEW				
			Rev.	DATE	DESCRIPTION					
			Concept Design Submission							
			CAD DWG File	103_Patchi-CFC-A-Zoning						
			Drawn by	JH			Date	21 . 02 . 2023	Rev.	04
			Checked by				Scale	1/50		
Sheet No.										

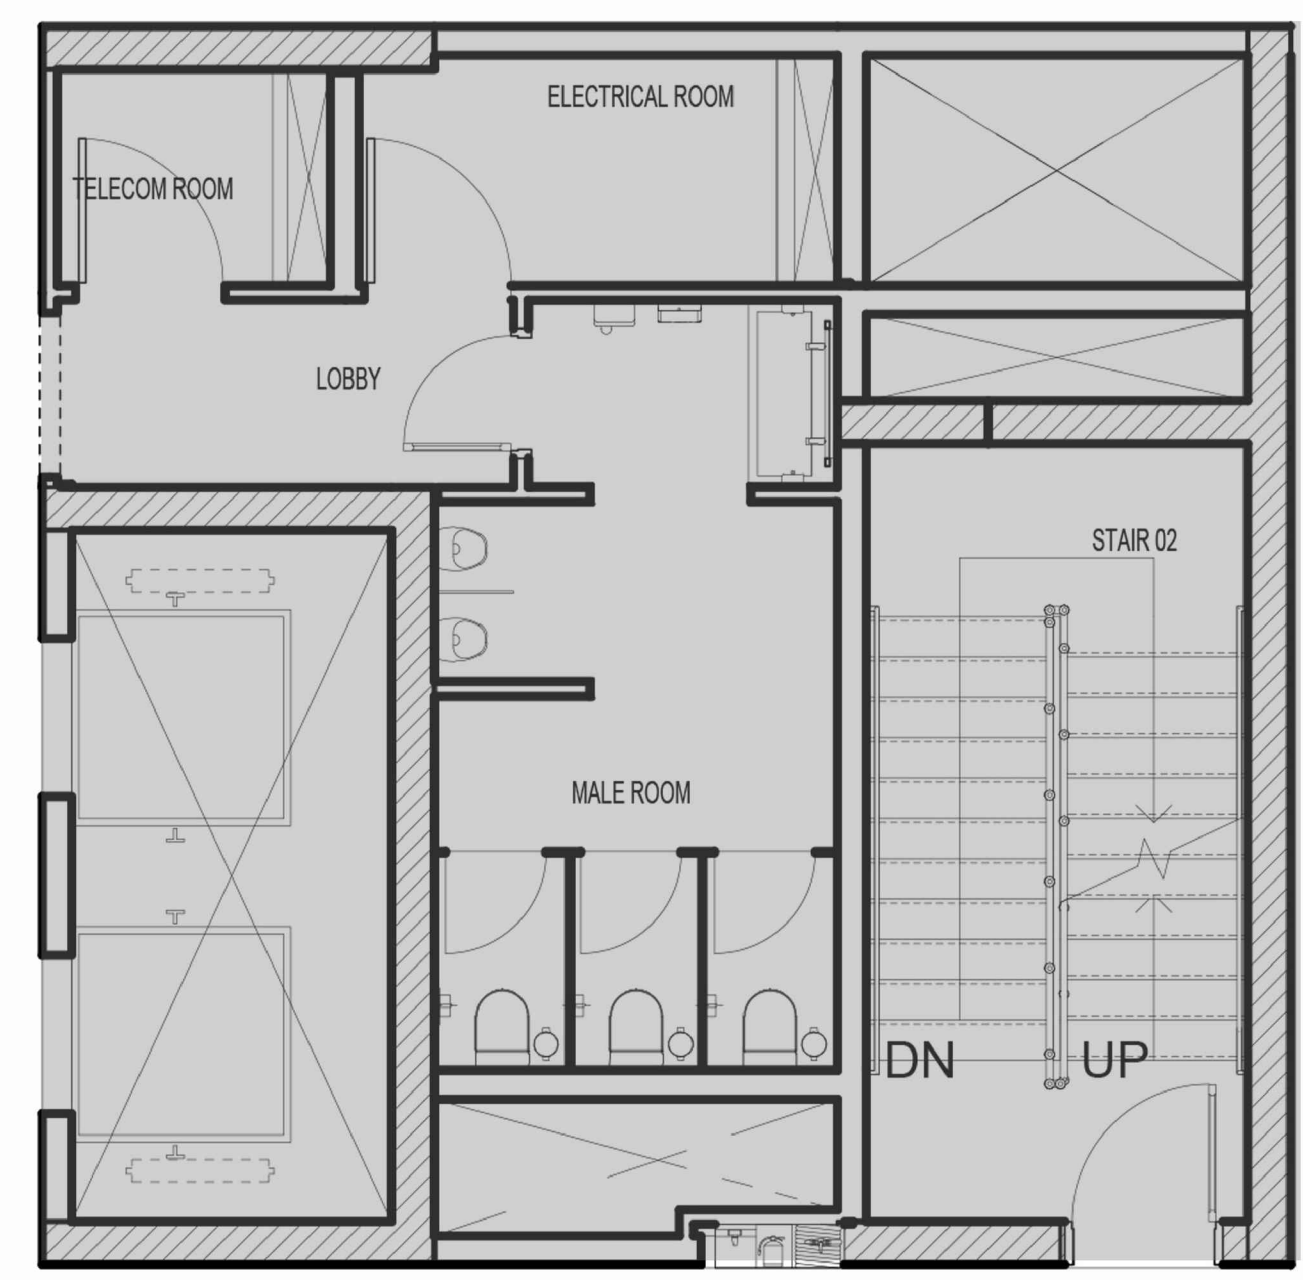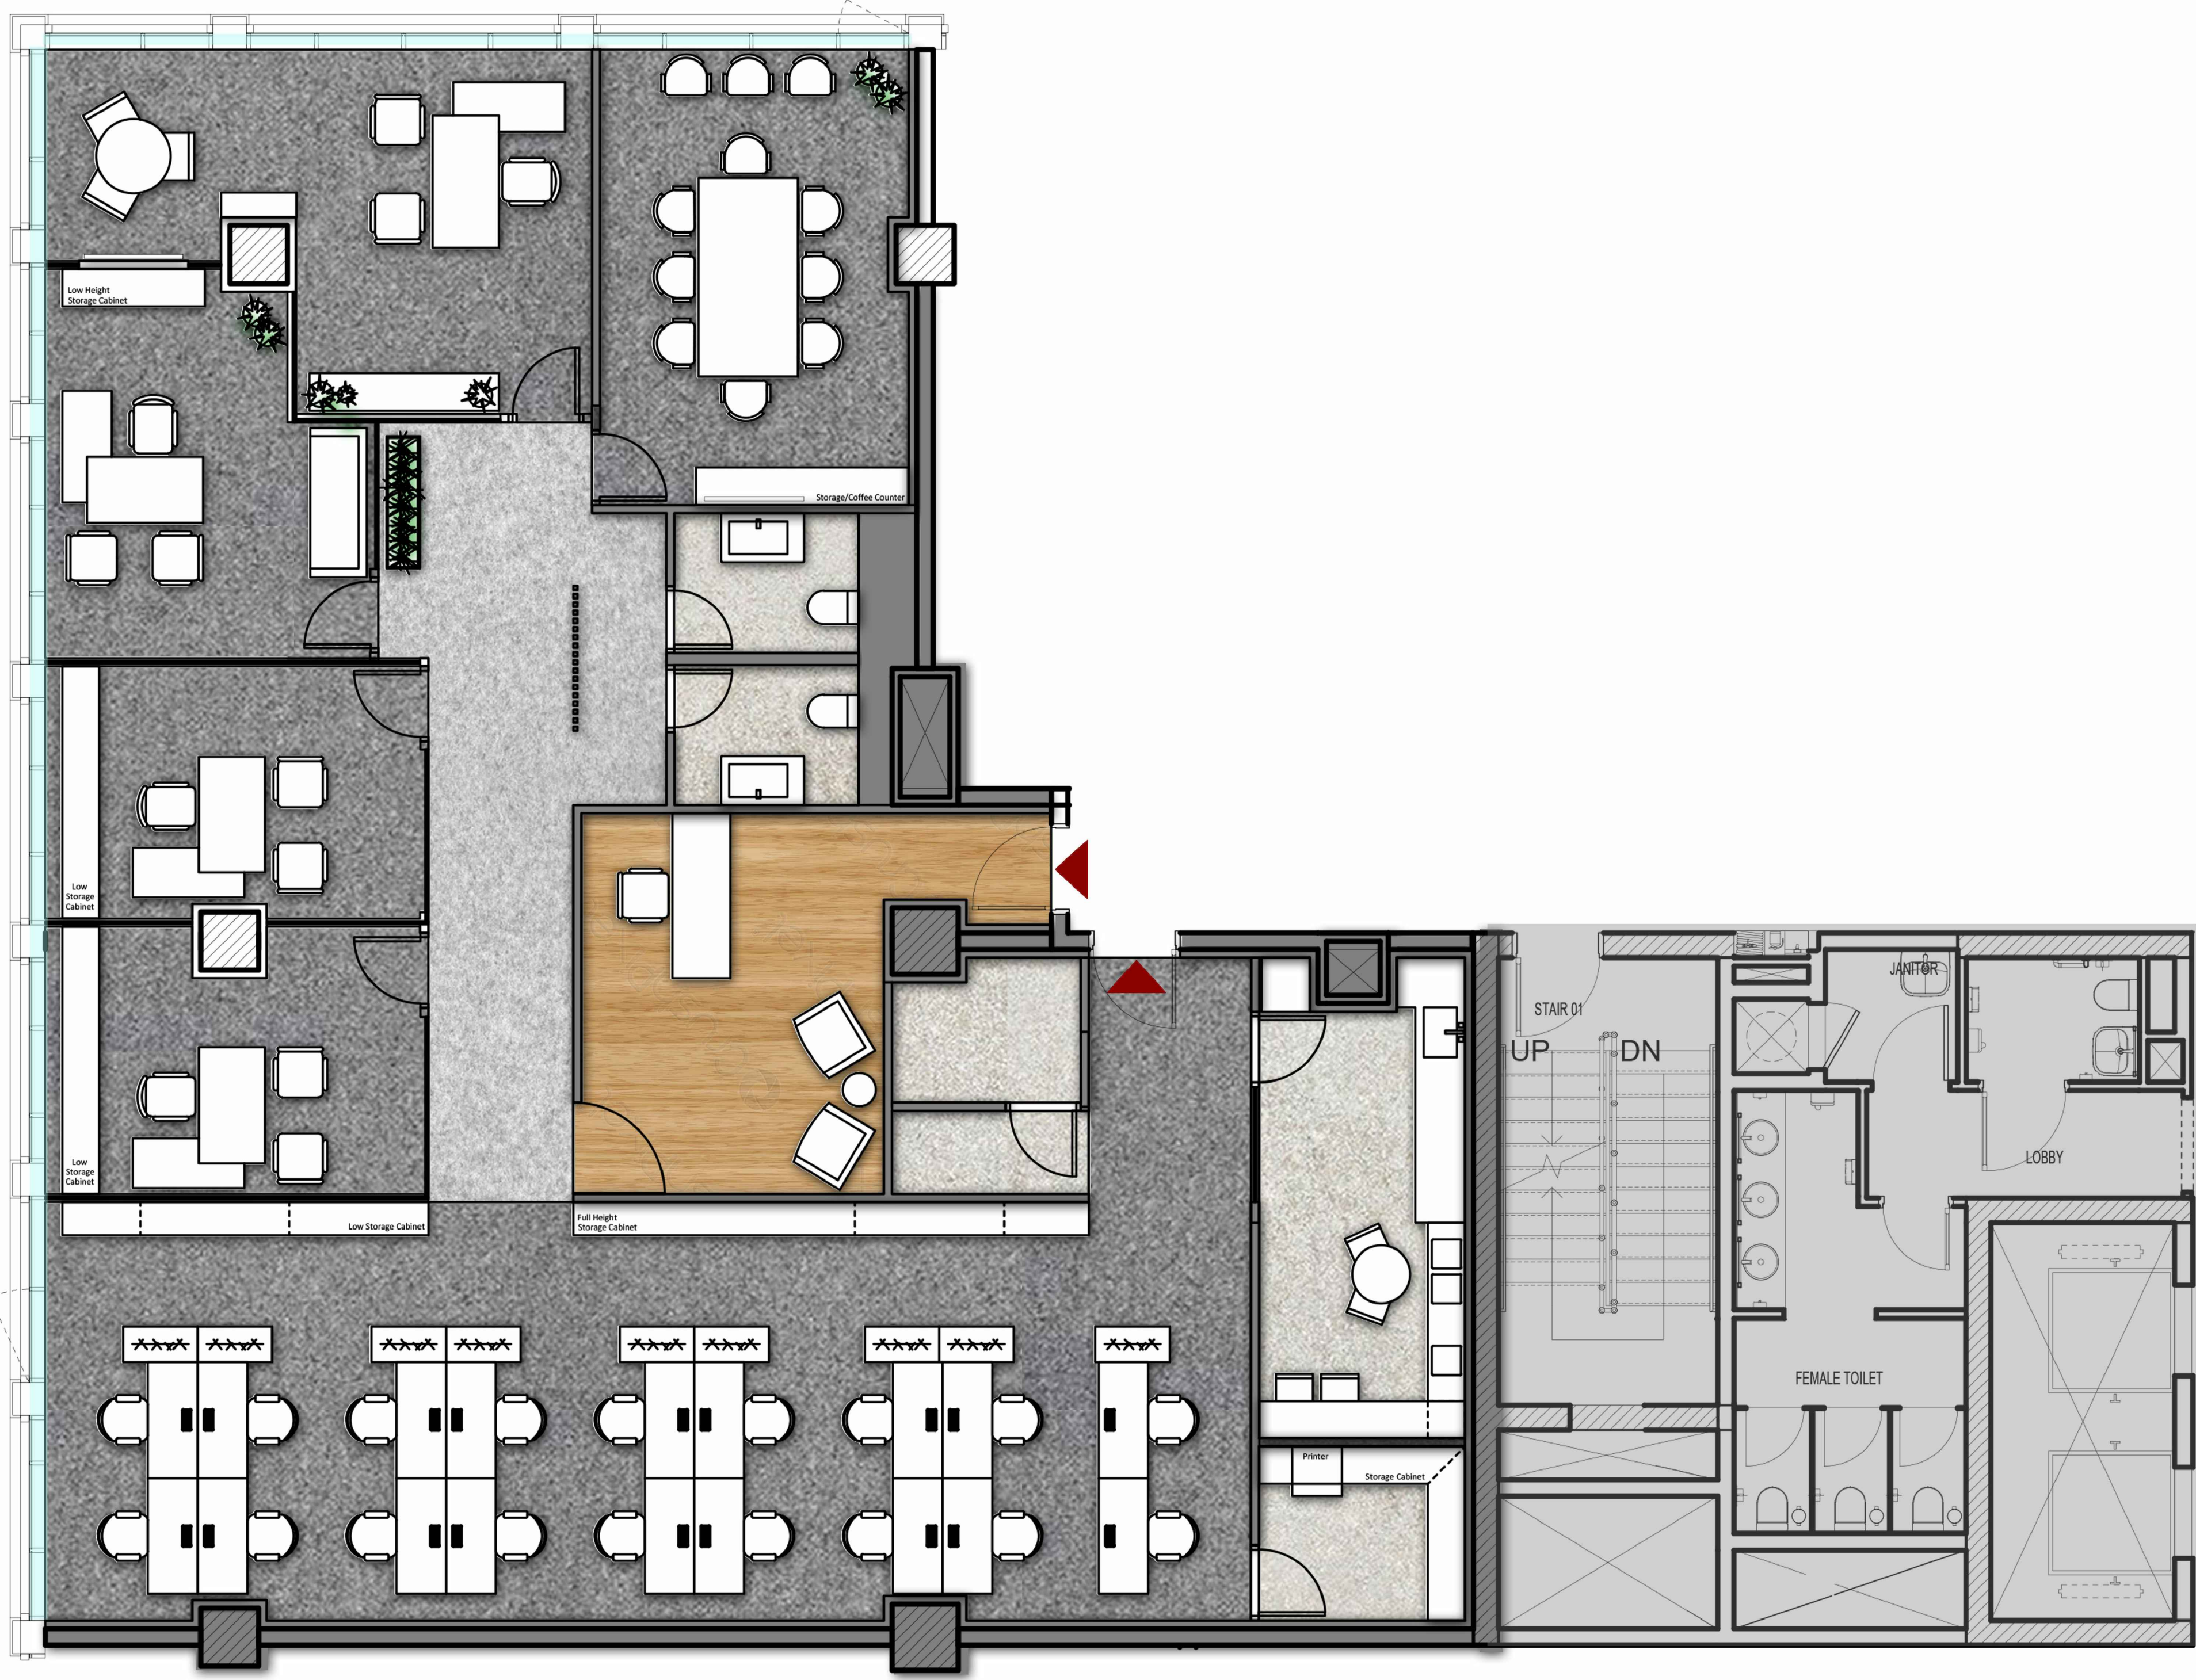


A
105.1
Fixtures Layout
Second Floor

Project	Client	Design by	NOTES:	SHEET TITLE					
Patchi New HQ CFC - Podium 2 Building P1			- THIS DRAWING IS COPY RIGHT PROTECTED AND CAN NOT BE REPRODUCED WITHOUT THE WRITTEN APPROVAL OF THE ARCHITECT. - ALL DIMENSIONS ARE IN CENTIMETERS UNLESS OTHERWISE MENTIONED. ALL DIMENSIONS MUST BE REVISED BY CONTRACTOR ON SITE.				Fixtures Layout		
				04	22-02-2023	FOR REVIEW			
				03	21-02-2023	FOR REVIEW			
				02	20-02-2023	FOR REVIEW			
				01	13-02-2023	FOR REVIEW			
				Rev.	DATE	DESCRIPTION			
				Concept Design Submission			A-105.1		
CAD DWG File:	105.Patchi-CFC-A-Fixtures			Date	21 . 02 . 2023	Rev.	04		
Drawn by	JH			Scale	1/50				
Checked by									
Sheet No.									

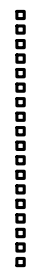


STAIR 01


P DN

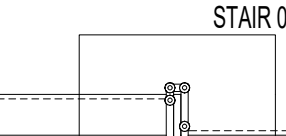

© Copyright 2018, FINE TOUCH CONTRACTORS, 11 Off Omar Ibn ELKhattab str.- Apart.603 - Ramu Buildings - Heliopolis 11341-Cairo - Egypt.

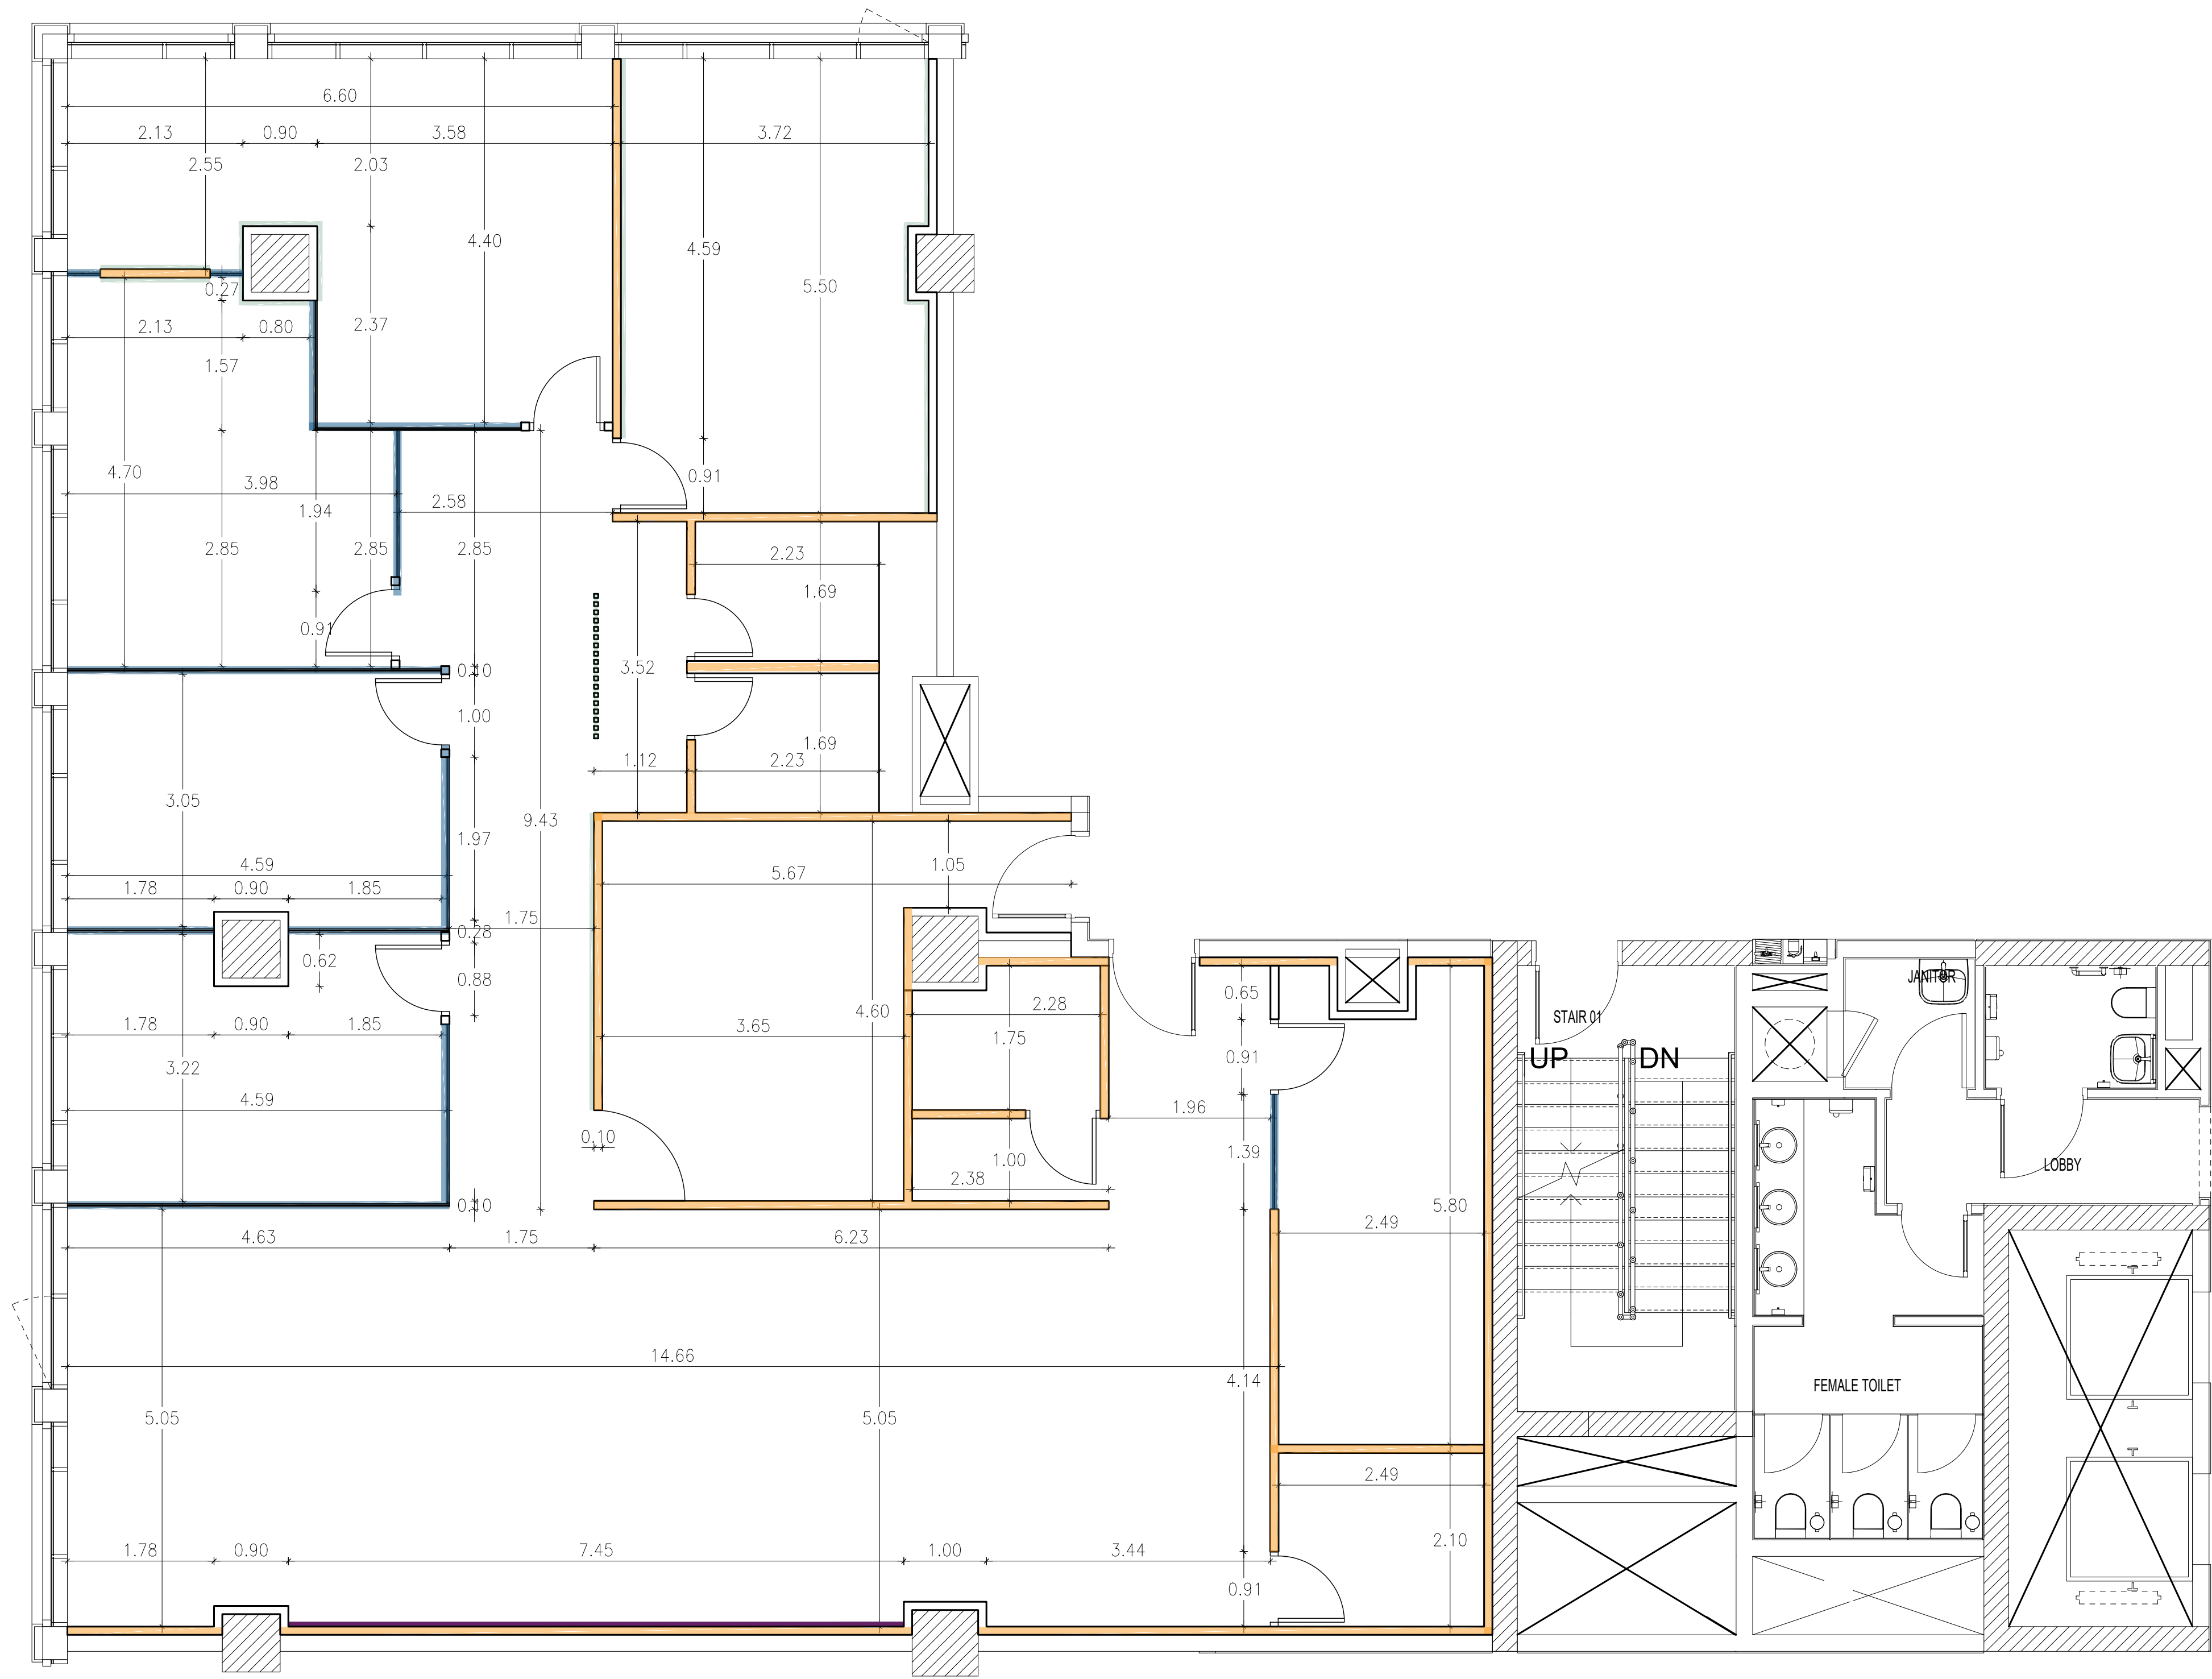


	DESCRIPTION
WF-01	10cm Gypsum board
WF-02	Double glazing glass partitions
WF-03	Wooden Cladding
WF-04	Acoustic panels


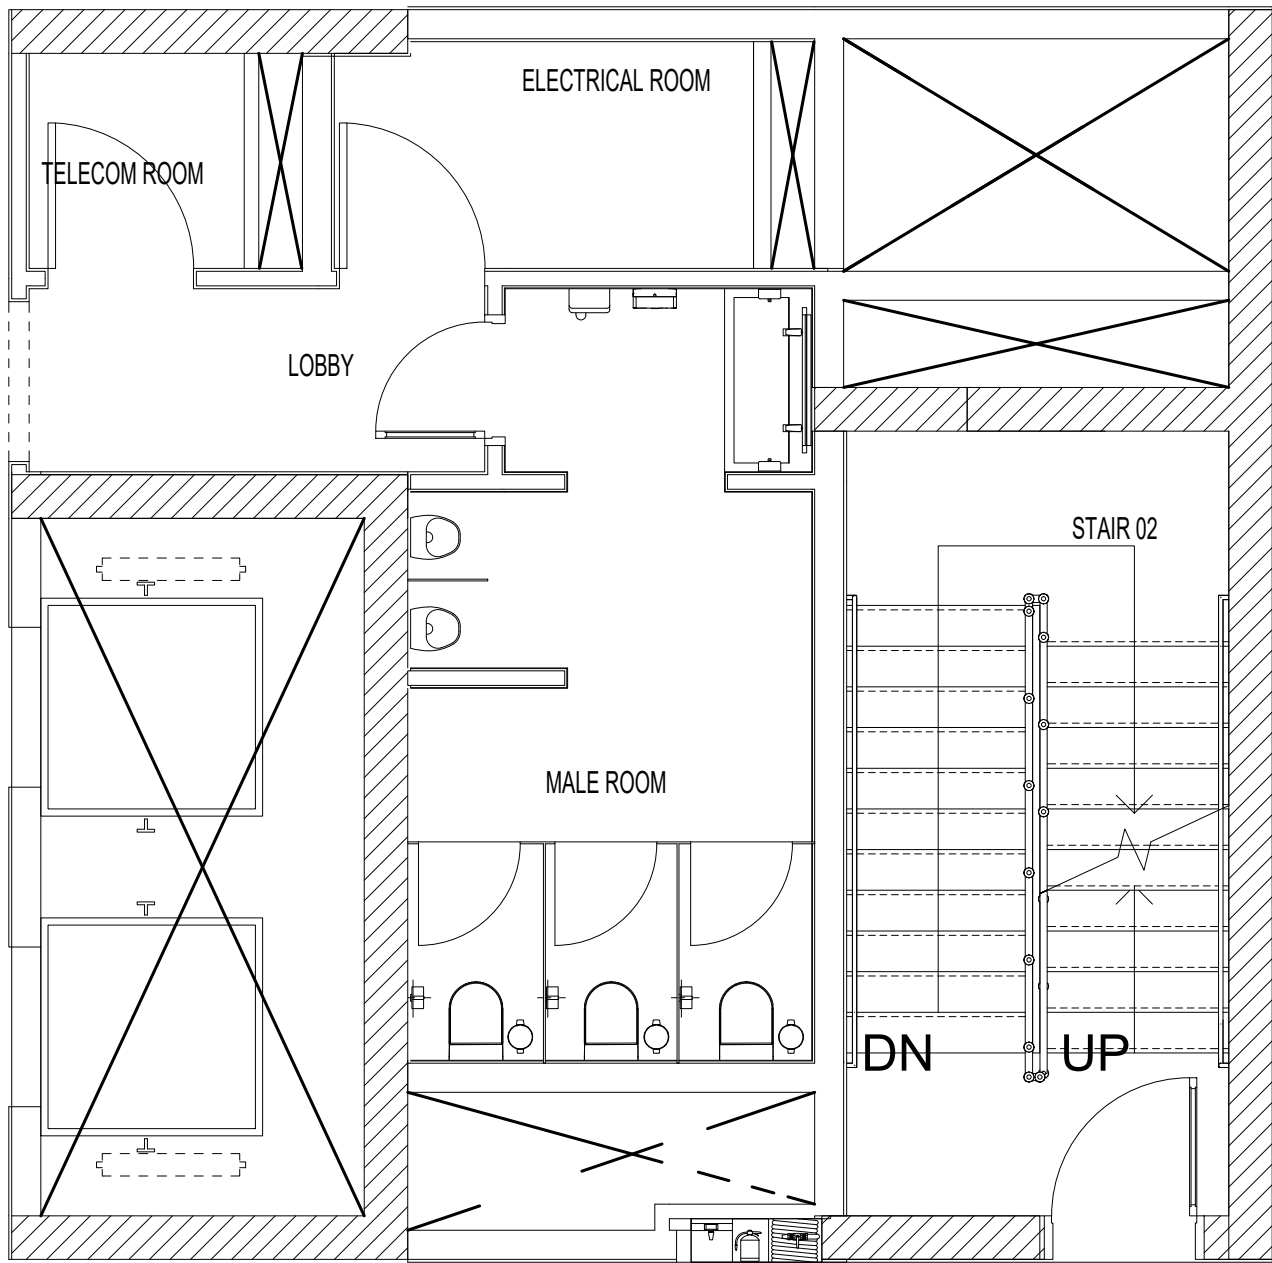


A

106


Construction Layout
Second Floor

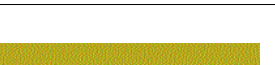Project	Client	Design by	NOTES:				SHEET TITLE			
Patchi New HQ CFC - Podium 2 Building P1			- THIS DRAWING IS COPY RIGHT PROTECTED AND CAN NOT BE REPRODUCED WITHOUT THE WRITTEN APPROVAL OF THE ARCHITECT. - ALL DIMENSIONS ARE IN CENTIMETERS UNLESS OTHERWISE MENTIONED. ALL DIMENSIONS MUST BE REVISED BY CONTRACTOR ON SITE.				Construction Layout			
			04	22-02-2023	FOR REVIEW		A-106			
			03	21-02-2023	FOR REVIEW					
			02	20-02-2023	FOR REVIEW					
			01	13-02-2023	FOR REVIEW					
Rev.	DATE	DESCRIPTION								
Concept Design Submission										
CAD DWG File		106.Patchi.CFC-A-Construction		Date	21 . 02 . 2023	Rev.	04			
Drawn by		JH		Scale 1/50						
Checked by										
Sheet No.										

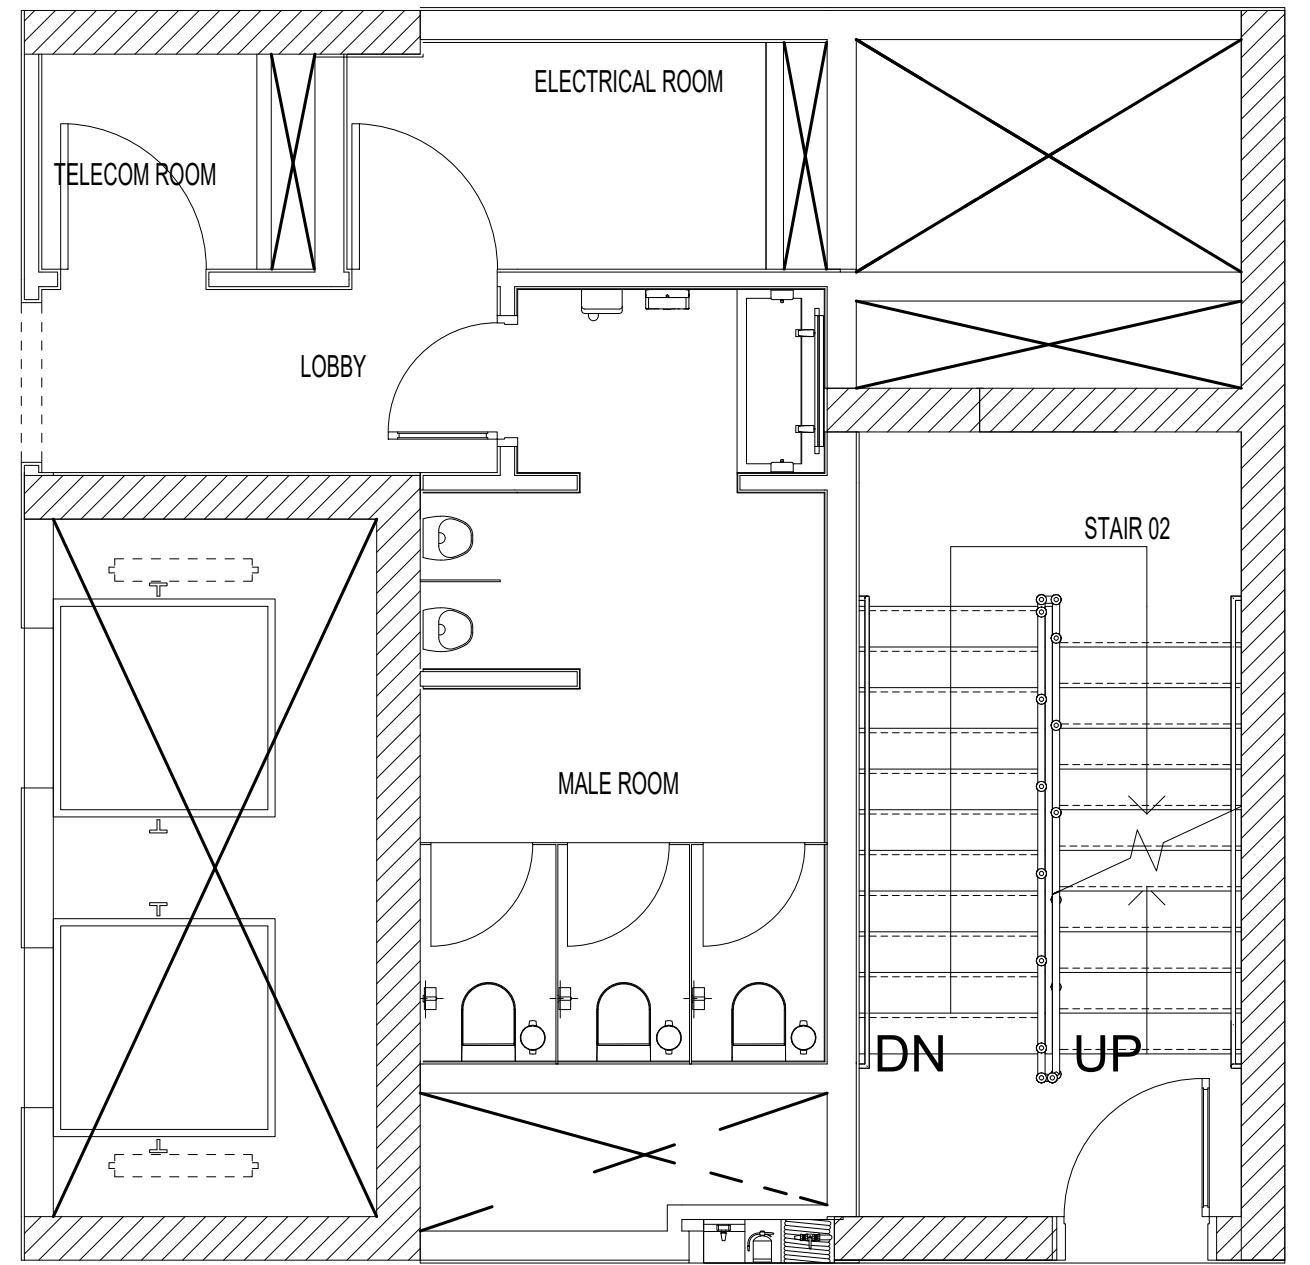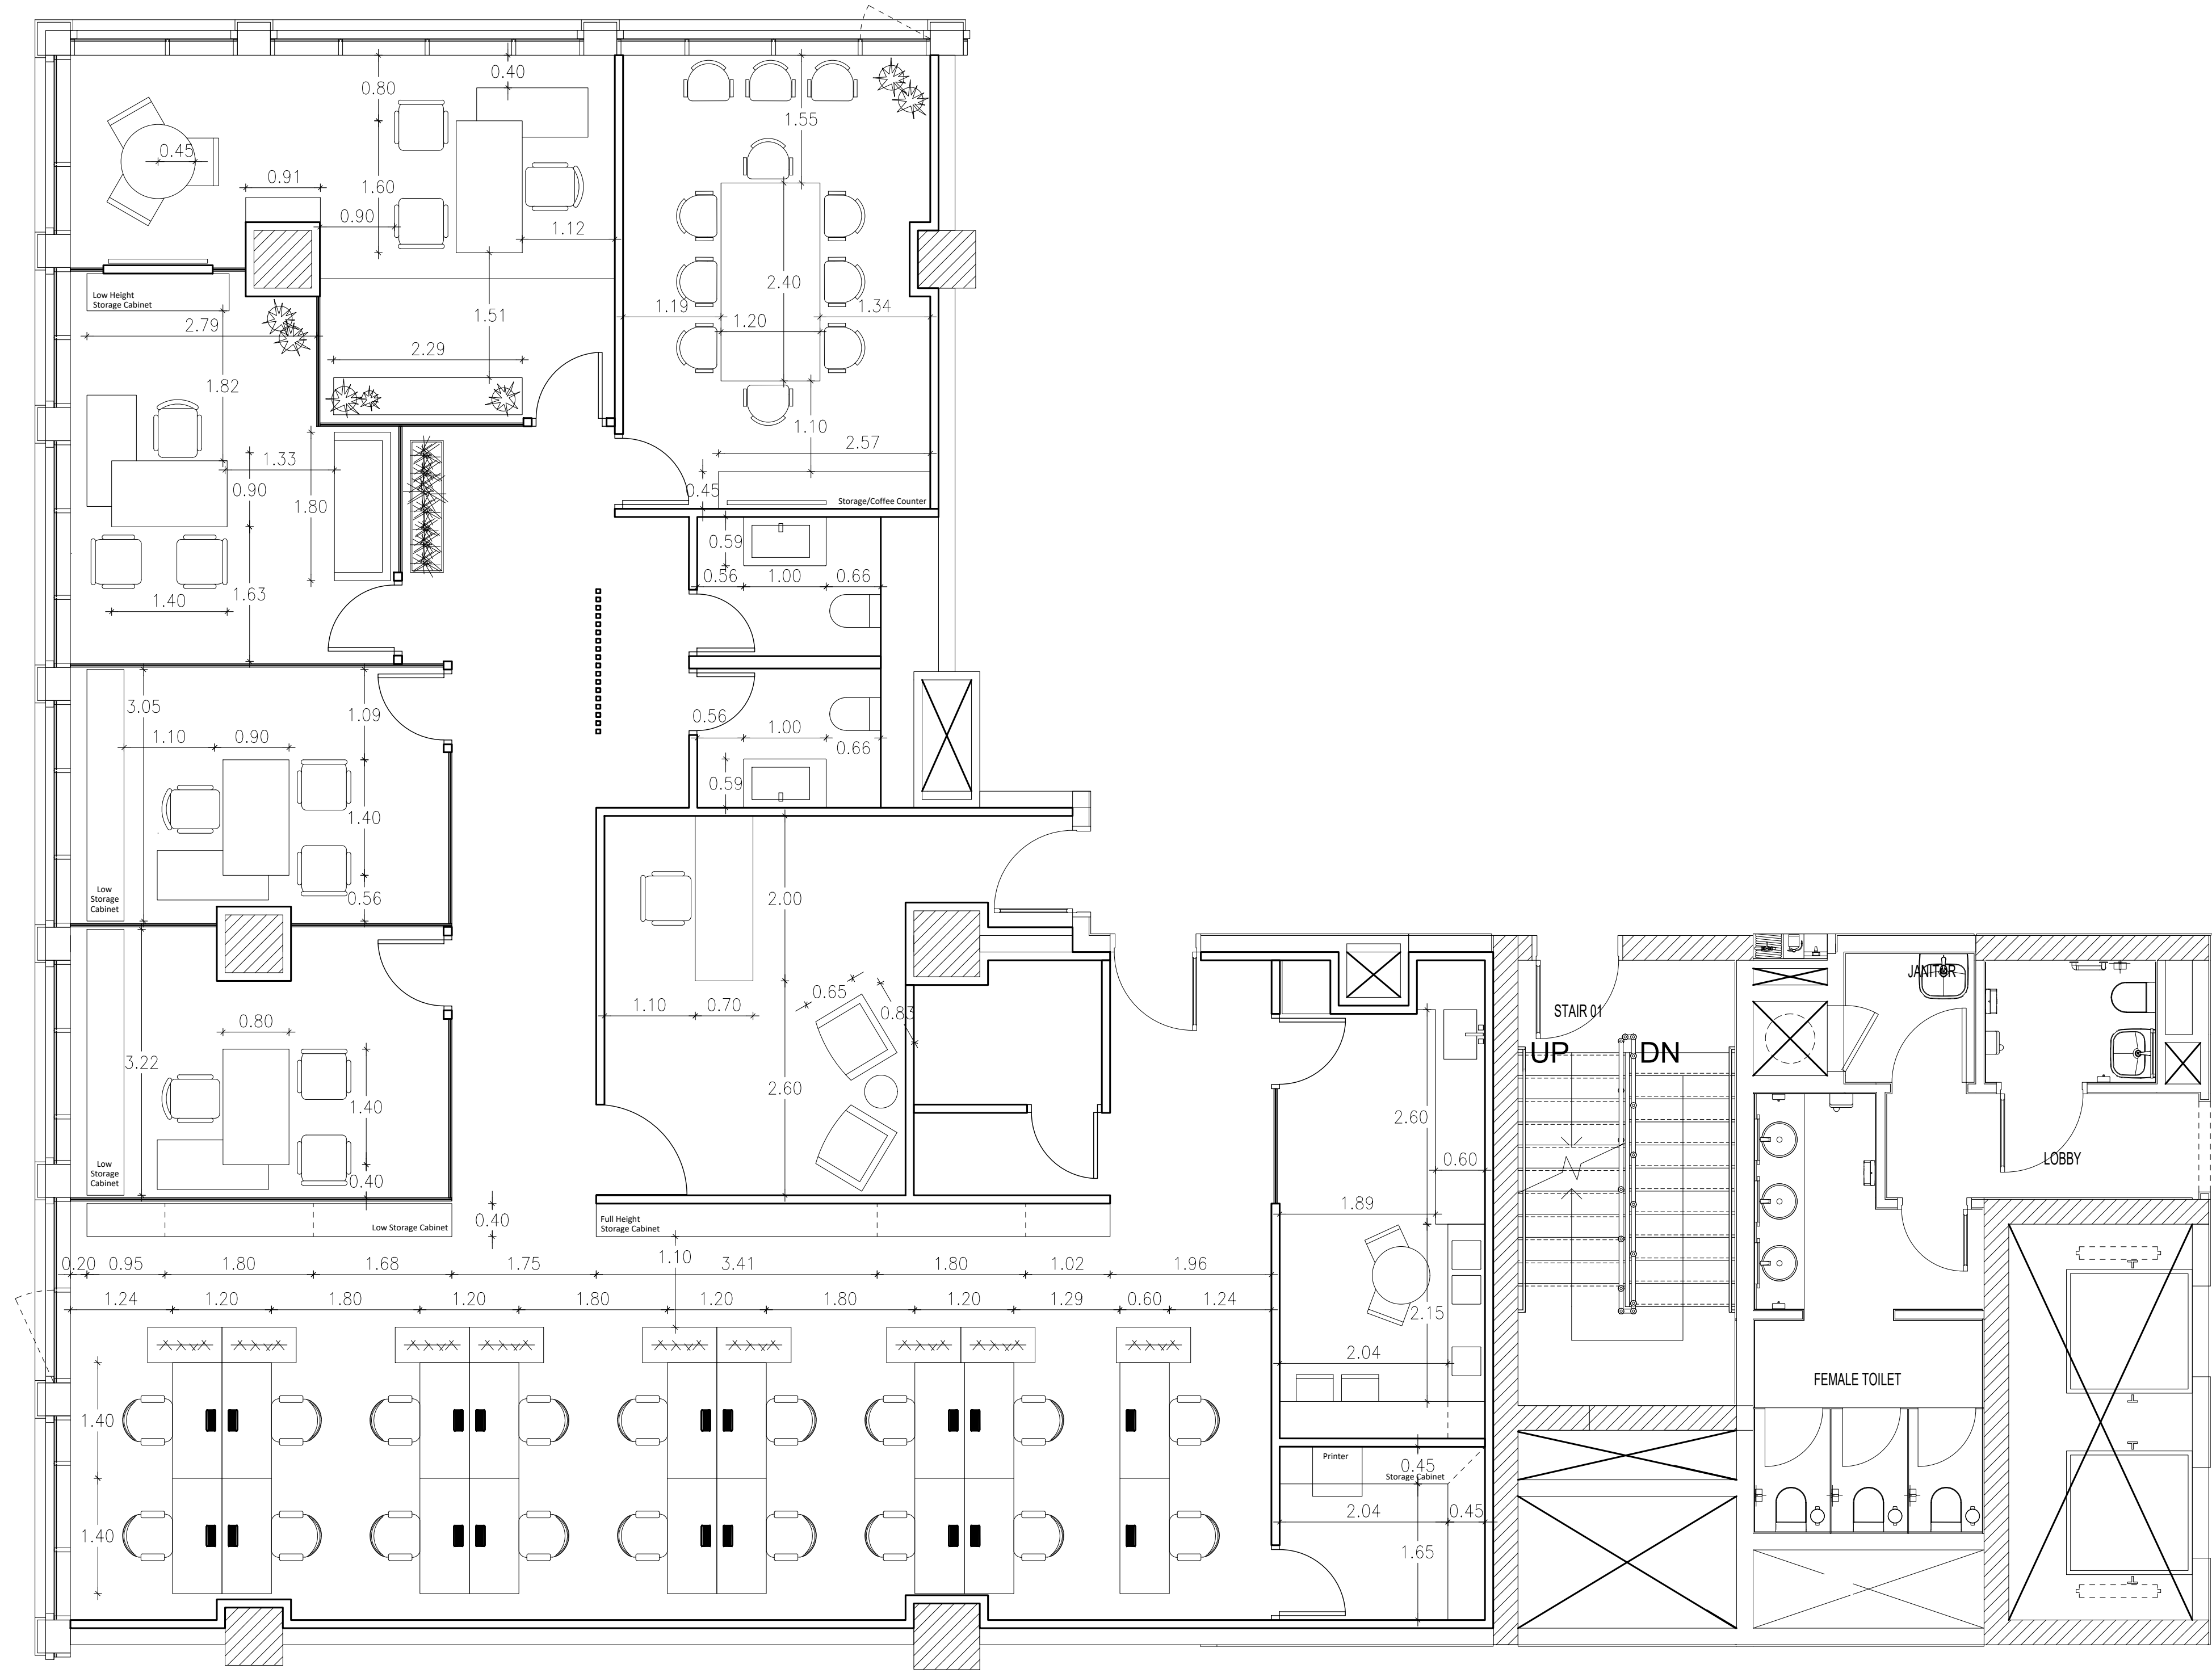


A
107 Setting Out Layout
Second Floor

Project	Client	Design by	NOTES:	SHEET TITLE				
Patchi New HQ CFC - Podium 2 Building P1			- THIS DRAWING IS COPY RIGHT PROTECTED AND CAN NOT BE REPRODUCED WITHOUT THE WRITTEN APPROVAL OF THE ARCHITECT.				Setting Out Layout	
			- ALL DIMENSIONS ARE IN CENTIMETERS UNLESS OTHERWISE MENTIONED. ALL DIMENSIONS MUST BE REVISED BY CONTRACTOR ON SITE.	04	22-02-2023	FOR REVIEW		
				03	21-02-2023	FOR REVIEW		
				02	20-02-2023	FOR REVIEW		
				01	13-02-2023	FOR REVIEW		
			Rev.	DATE	DESCRIPTION			
			Concept Design Submission			A-107		
CAD DWG File:	107.Patchi-CFC-A-Setting Out			Date	21 . 02 . 2023	Rev.	04	
Drawn by	JH							
Checked by				Scale	1/50			
Sheet No.								

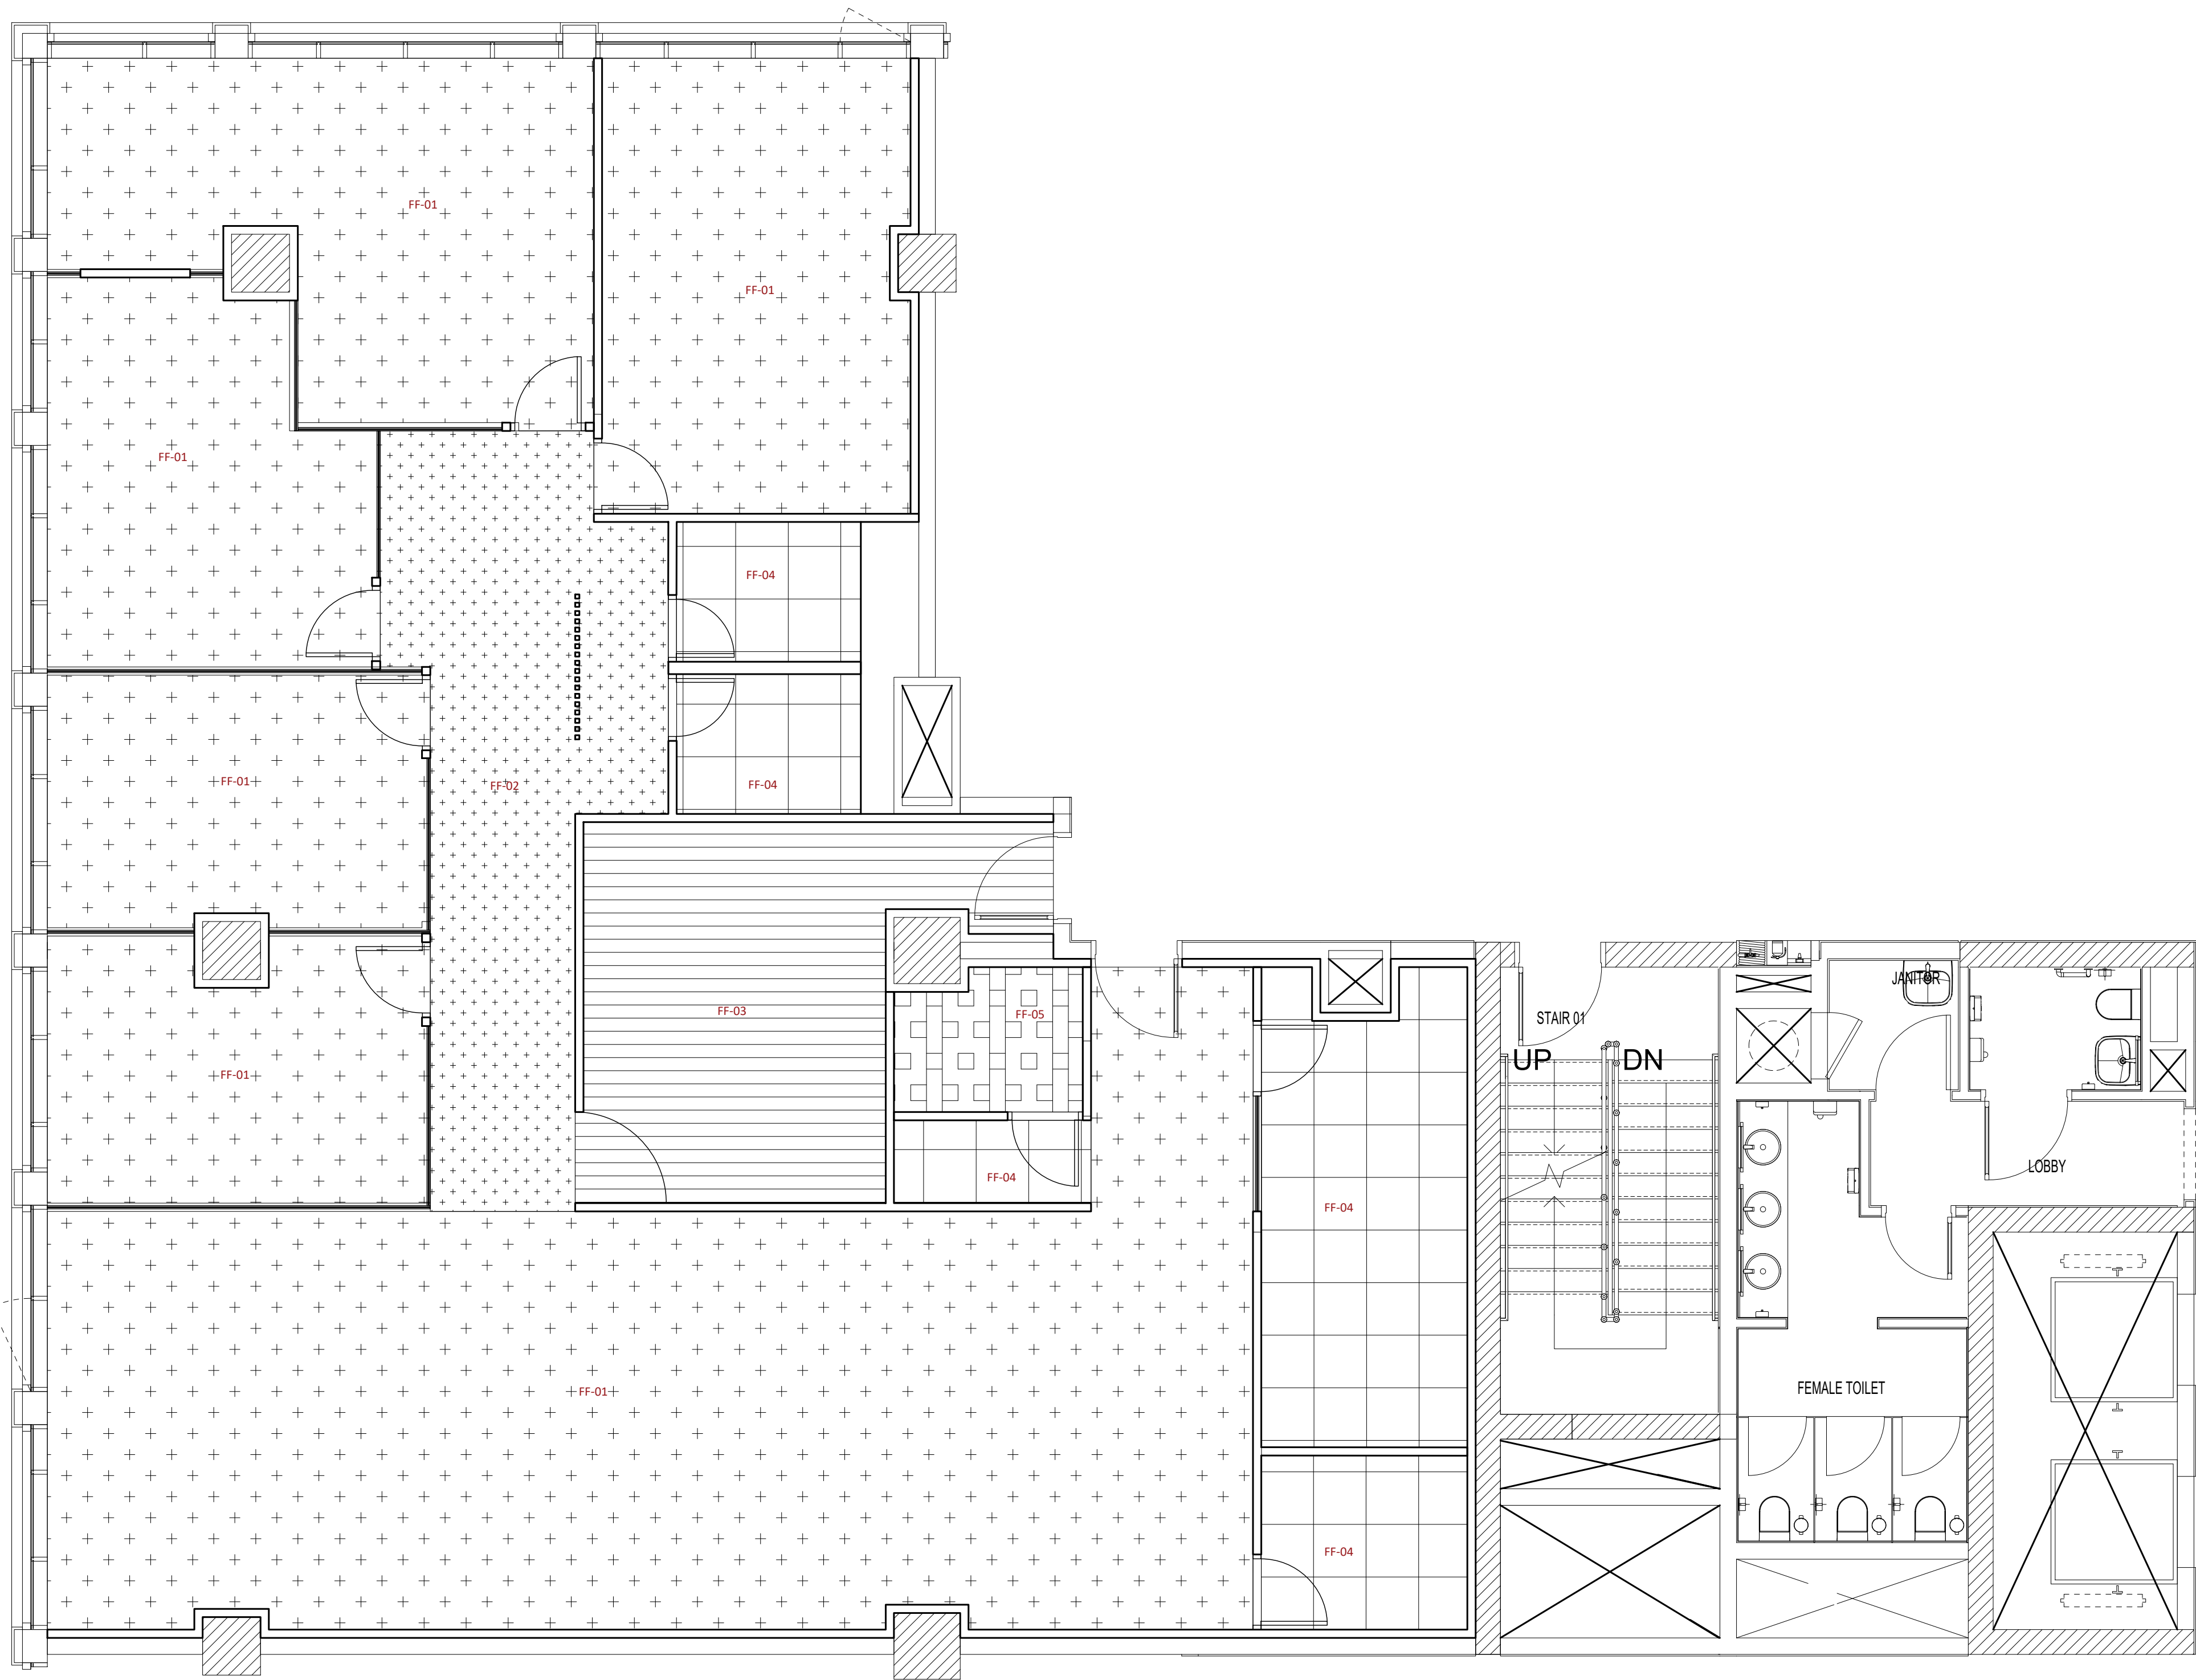

		DESCRIPTION	AREA
FF-01		Carpet Tiles Light Grey	165 SQM
FF-02		Colored Carpet Tiles - TBC	25 SQM
FF-03		Engineered Wood	20 SQM
FF-04		Porcelain Tiles	30 SQM
FF-05		Raised Floor	4 SQM

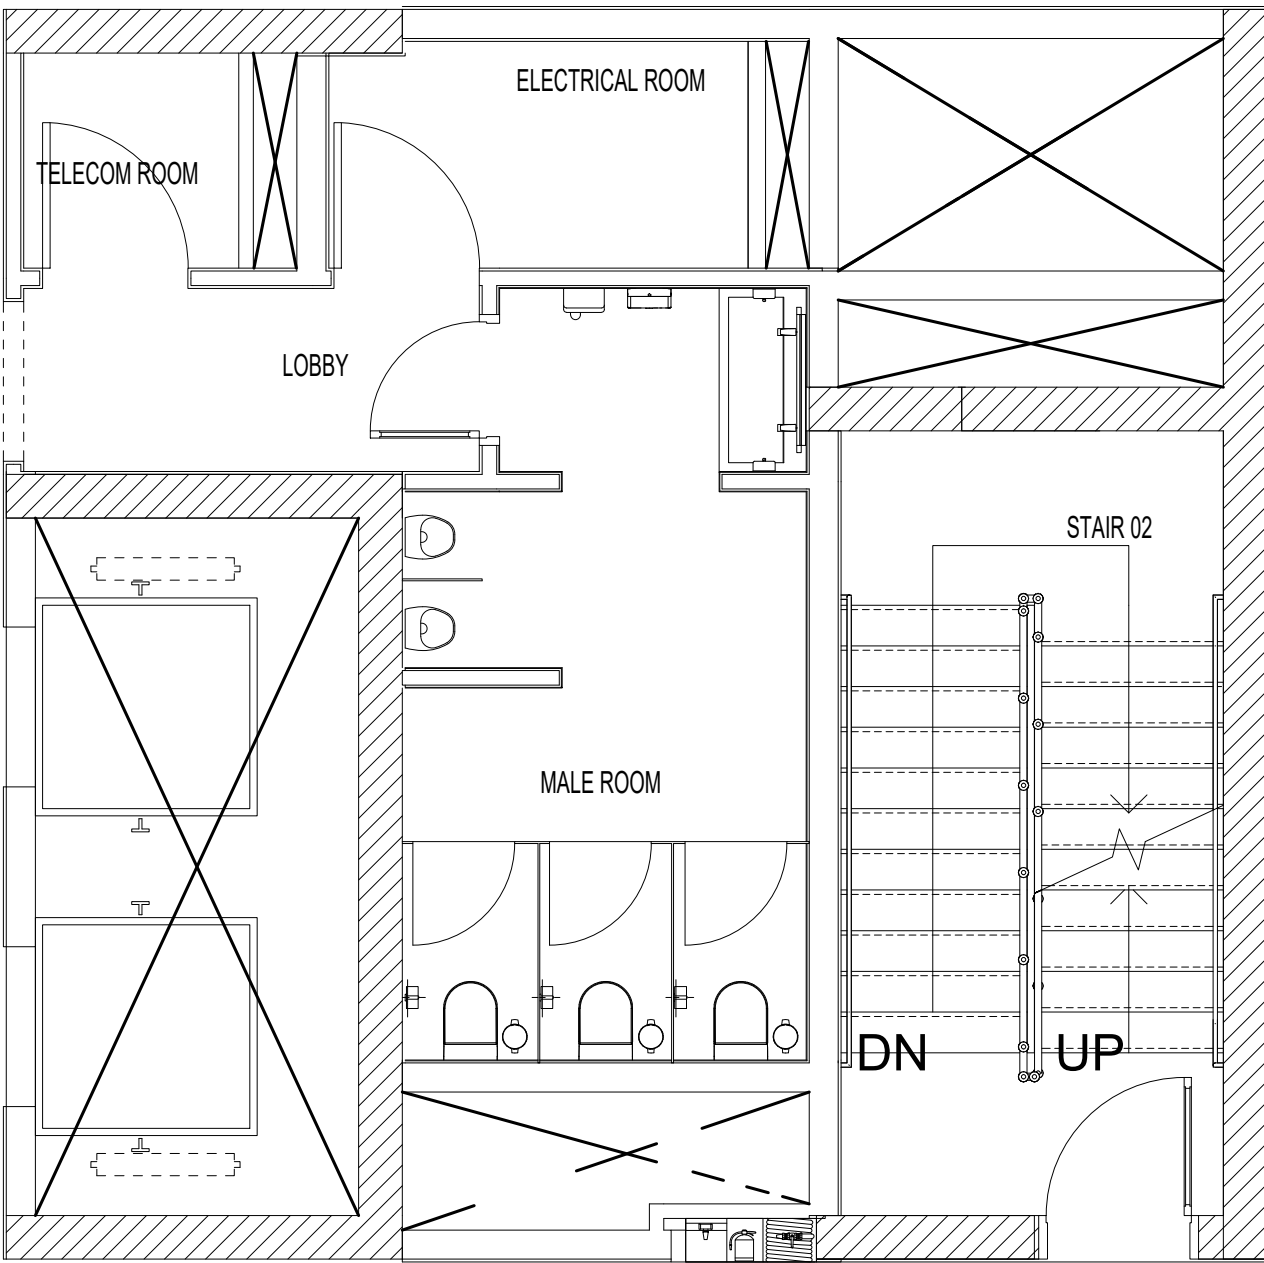

A


108

Flooring Layout
Second Floor


Project	Client	Design by
Patchi New HQ CFC - Podium 2 Building P1		

©Copyright 2018, FINE TOUCH CONTRACTORS, 11 Off Omar Ibn ELKhatTab str.- Apart.603 - Ramu Buildings - Heliopolis 11341- Cairo - Egypt.


NOTES:			SHEET TITLE	
- THIS DRAWING IS COPY RIGHT PROTECTED AND CAN NOT BE REPRODUCED WITHOUT THE WRITTEN APPROVAL OF THE ARCHITECT. - ALL DIMENSIONS ARE IN CENTIMETERS UNLESS OTHERWISE MENTIONED. ALL DIMENSIONS MUST BE REVISED BY CONTRACTOR ON SITE.			Flooring Layout	
			A-108	
			Date	21 . 02 . 2023
			Rev.	04
			Scale	1/50

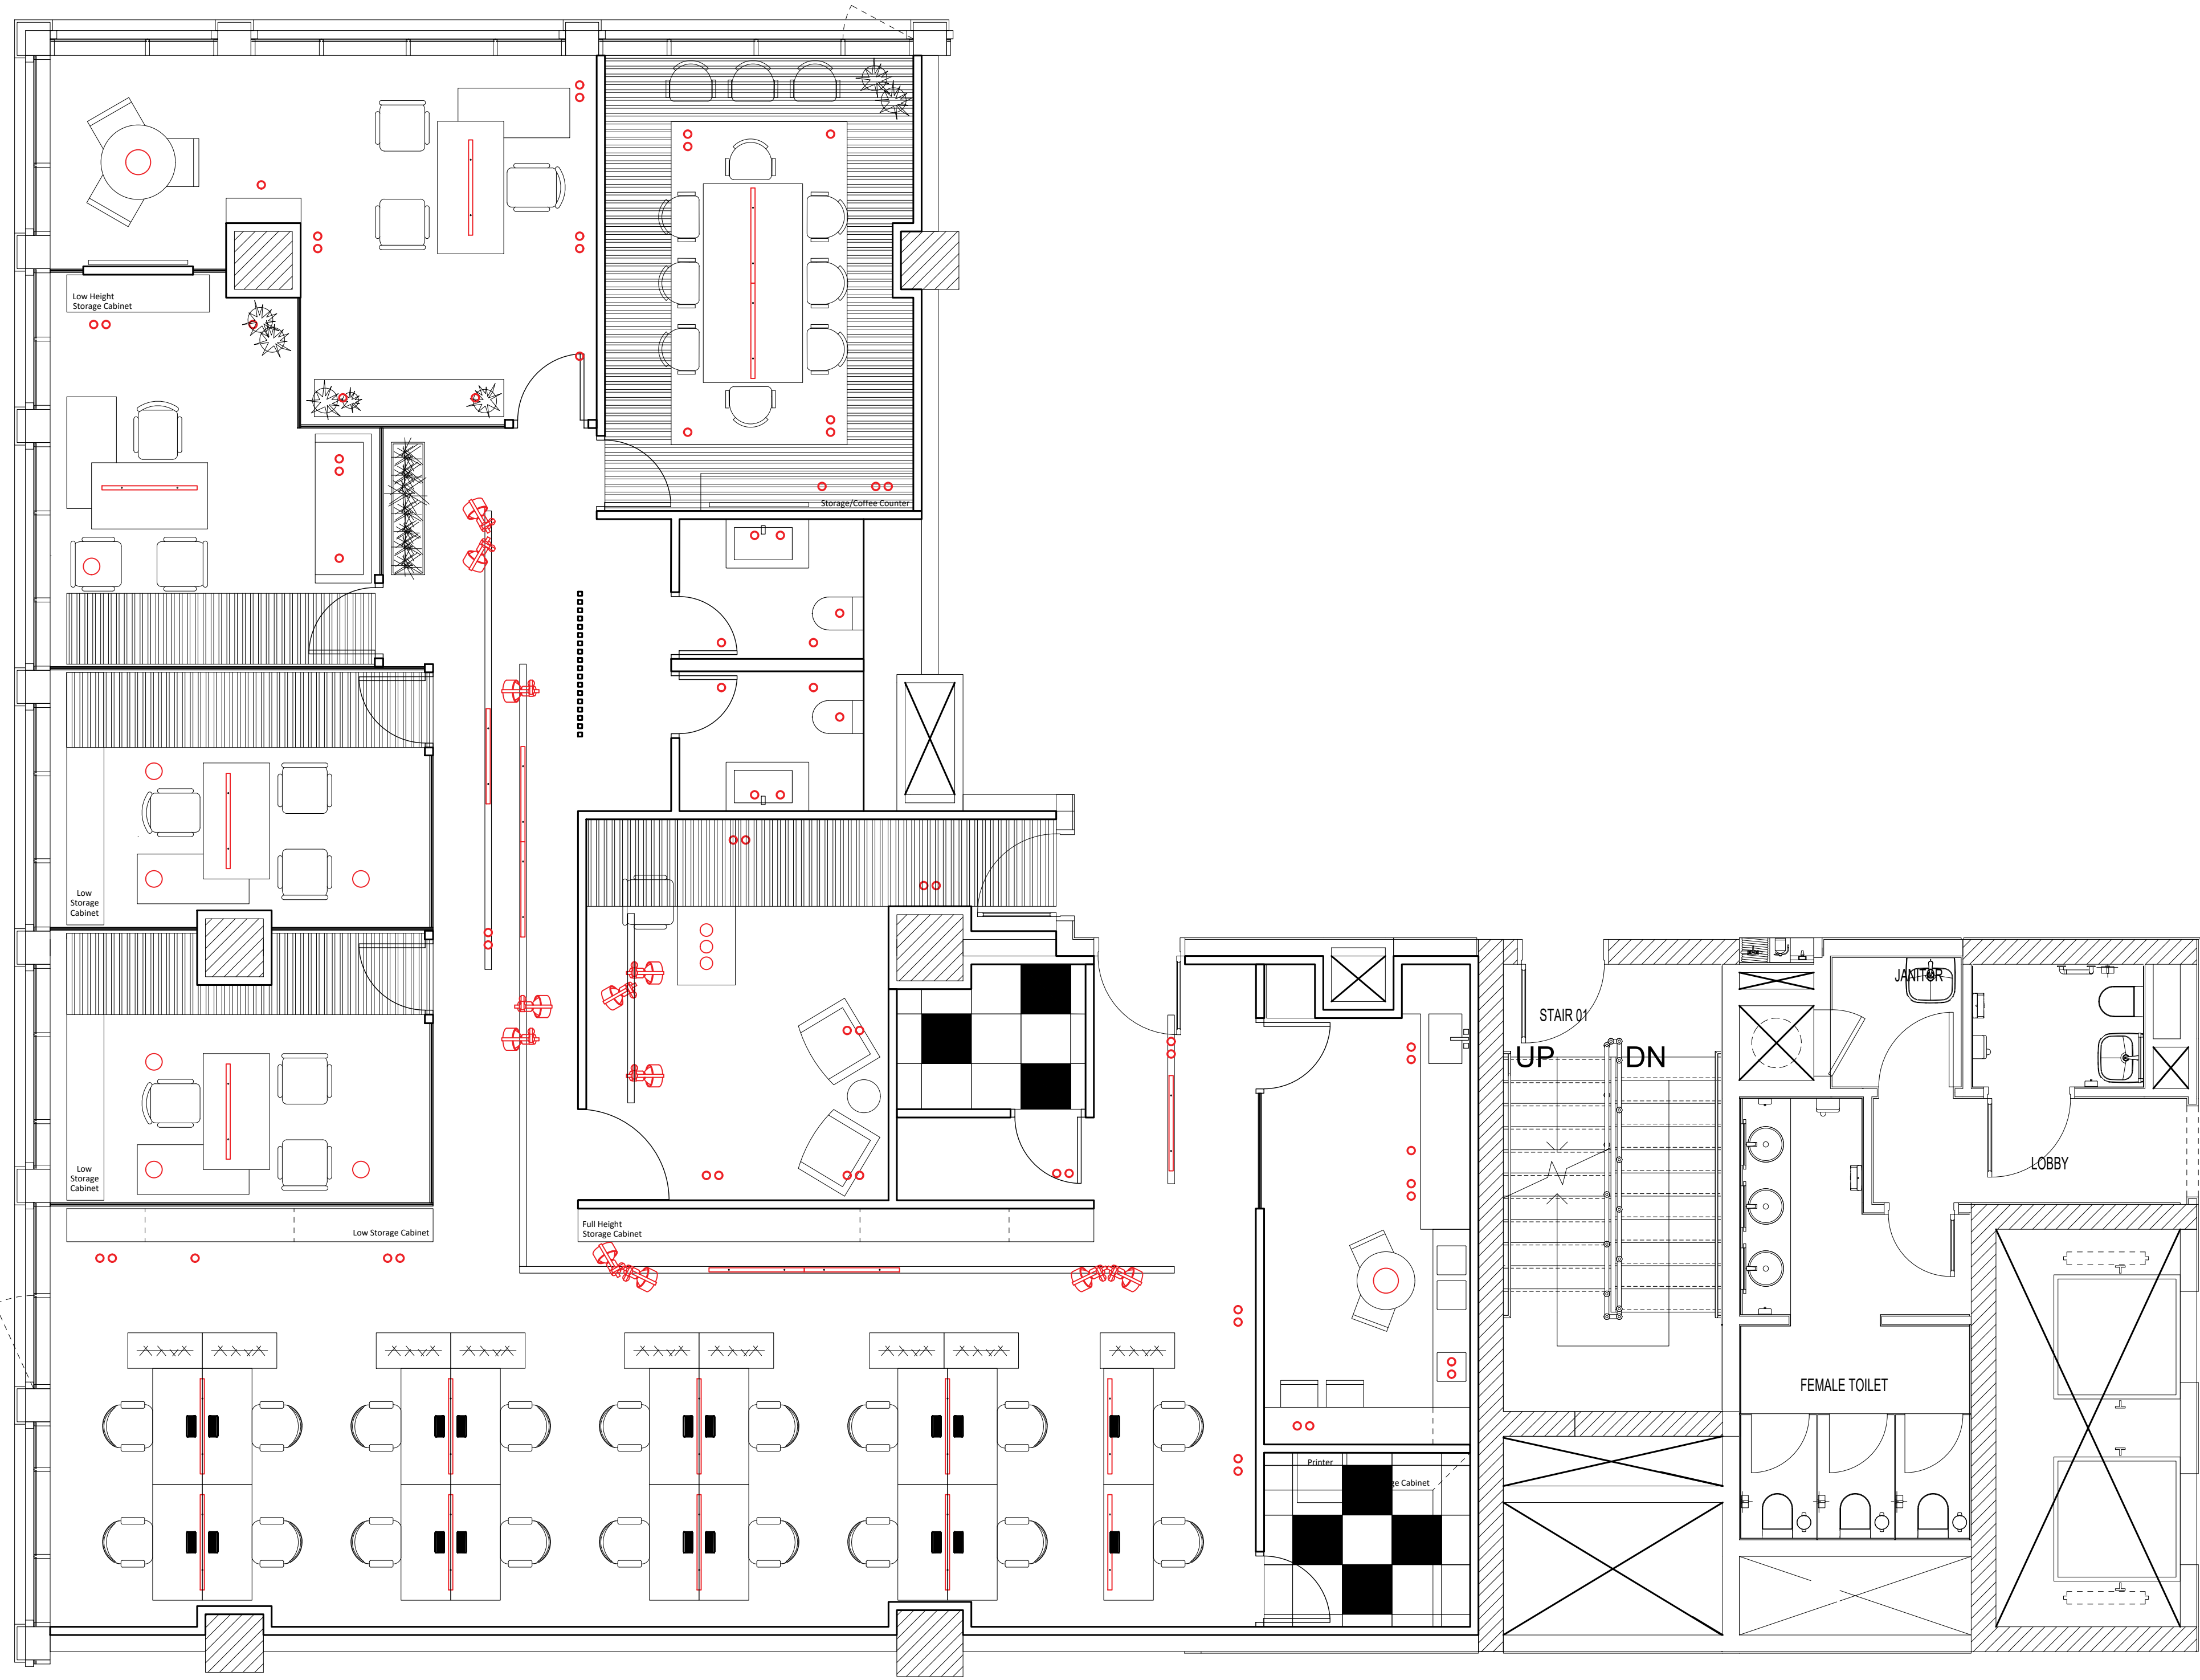

SYMBOL	DESCRIPTION	SYMBOL	DESCRIPTION
	Gypsum board ceiling		Ceiling mounted down light
	Wooden ceiling feature		Ceiling mounted spot light
			Linear Light
			Track Light

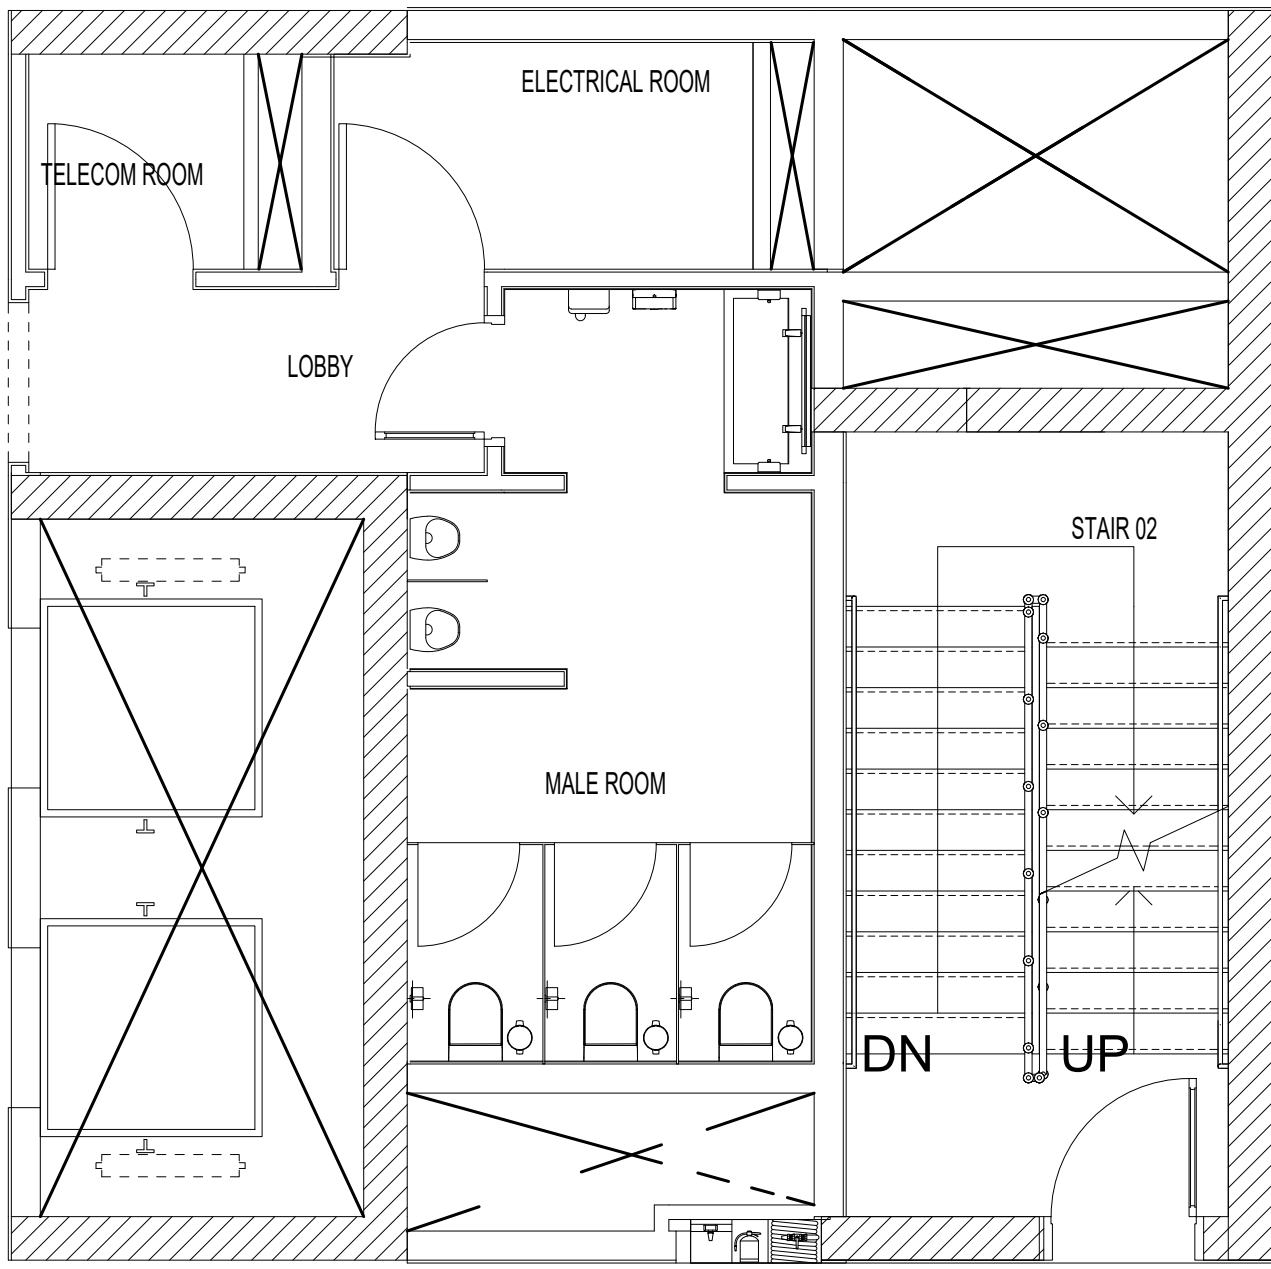

A
109
Reflected Ceiling Plan
Second Floor

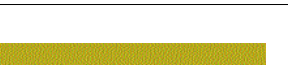Project	Client	Design by	NOTES:	SHEET TITLE				
Patchi New HQ CFC - Podium 2 Building P1			- THIS DRAWING IS COPY RIGHT PROTECTED AND CAN NOT BE REPRODUCED WITHOUT THE WRITTEN APPROVAL OF THE ARCHITECT.					
			- ALL DIMENSIONS ARE IN CENTIMETERS UNLESS OTHERWISE MENTIONED. ALL DIMENSIONS MUST BE REVISED BY CONTRACTOR ON SITE.	04	22-02-2023	FOR REVIEW	Reflected Ceiling Plan	
				03	21-02-2023	FOR REVIEW		
				02	20-02-2023	FOR REVIEW		
				01	13-02-2023	FOR REVIEW		
			Rev.	DATE	DESCRIPTION			
			Concept Design Submission					
			CAD DWG File			109.Patchi-CFC-A-RCP		
			Drawn by			JH		
			Checked by					
			Sheet No.					
			Date	21 . 02 . 2023	Rev.	04		
			Scale	1/50				